



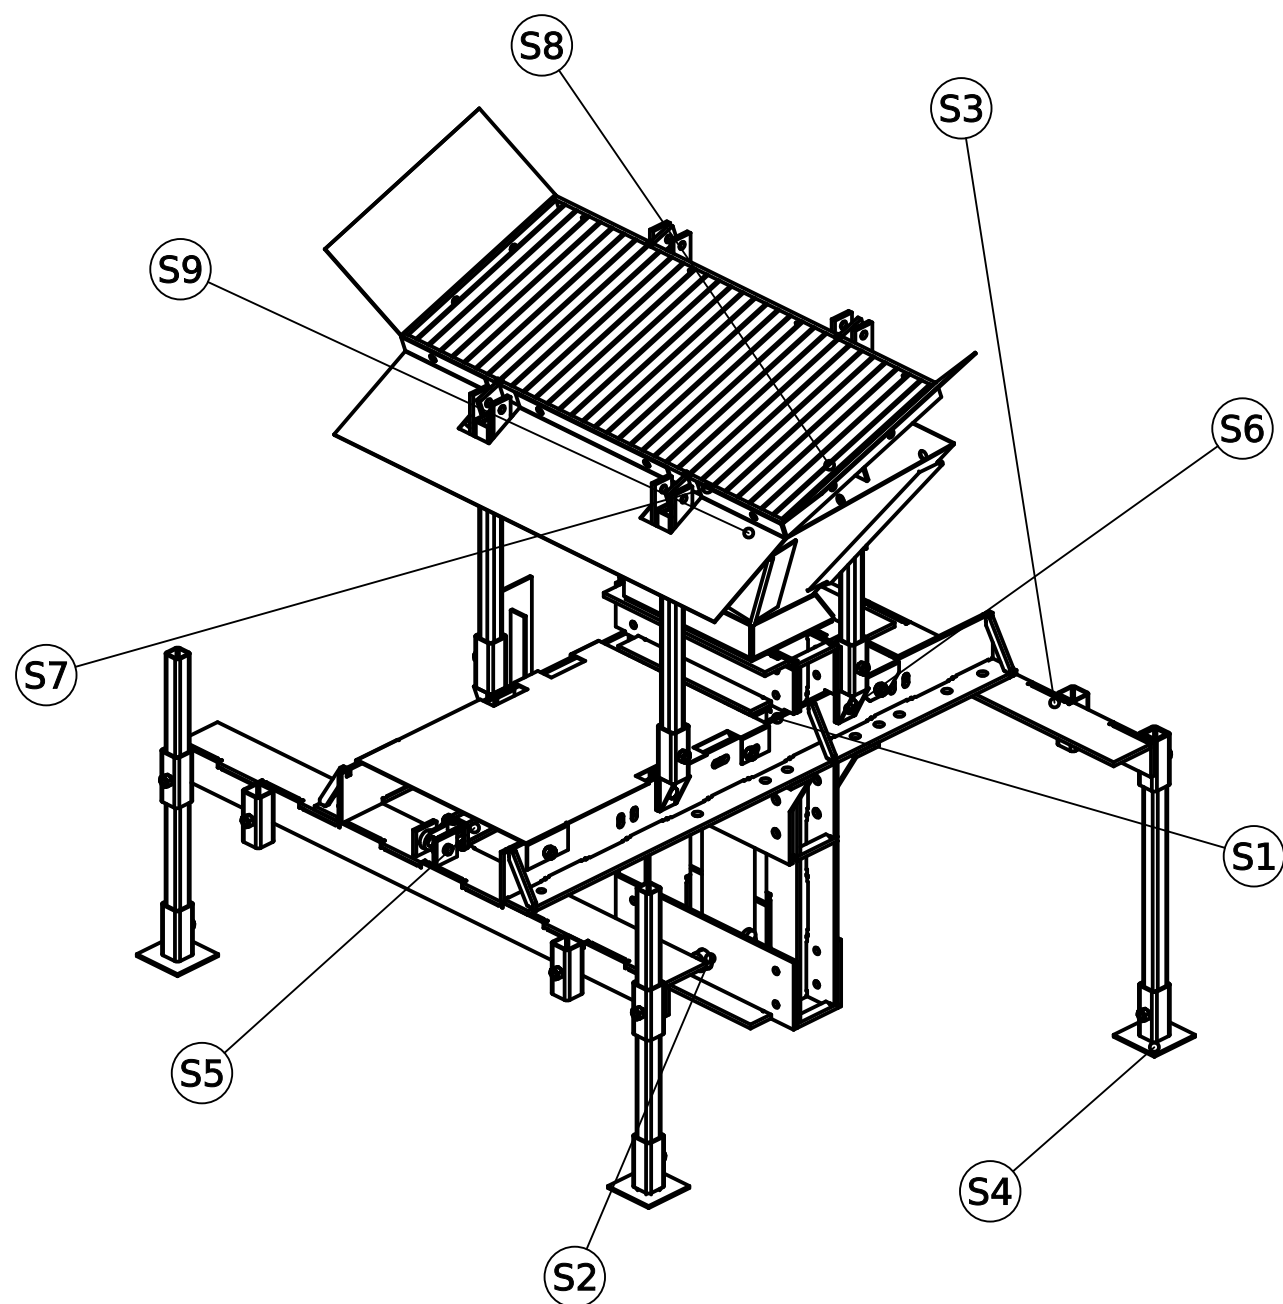

ISOMETRIC VIEW

- NOTES:
- 1. ALL DIMENSIONS IN INCHES. TOLERANCE $\pm 1/32$ UNLESS NOTED.
 - 2. BREAK SHARP EDGES, REMOVE BURRS.
 - 3. MATERIAL PER TITLE BLOCK. FILLET WELDS 1/4 UNLESS NOTED.
 - 4. FABRICATED STEEL ABOUT 1,790 LB.
 - 5. MODEL: OSE FULL_ASSEMBLY.STP, 01-001-00-6 CEB PRESS 6 MAIN ASSEMBLY.
 - 6. SHEETS 2-10: MODULES OF THE A-Z BUILD 1.0 MANUAL; THEN ONE SHEET PER OSE PART NUMBER.
 - 7. SOIL SHAKER AS BUILT IN THE A-Z MANUAL (ANGLE VERSION): SEE ../SHAKER.


S9	1	Controls	Module	109.0	OSEP6-P6-S9
S8	1	Soil Shaker	Module	91.7	OSEP6-P6-S8
S7	1	Grate	Module	198.0	OSEP6-P6-S7
S6	1	Hopper	Module	320.1	OSEP6-P6-S6
S5	1	Drawer	Module	241.1	OSEP6-P6-S5
S4	1	Feet and Legs	Module	100.5	OSEP6-P6-S4
S3	1	Arms	Module	407.3	OSEP6-P6-S3
S2	1	Press Cylinder and Foot	Module	166.2	OSEP6-P6-S2
S1	1	Main Frame	Module	477.7	OSEP6-P6-S1
Item	Qty	Title	Stock	lb ea	Drawing no.
Material		Qty	Scale	Units	Projection
See parts list		1	1:20	inch	
Created by		Approved by	Document type		Status
J. Clements III		-	Assembly drawing		Draft
Legal owner		Title		Identification number	Sheet
J. Clements III		OSE CEB Press 6		OSEP6-P6-00	1/94
CEB Project		General assembly		Rev A Date of issue 2026-10-04	

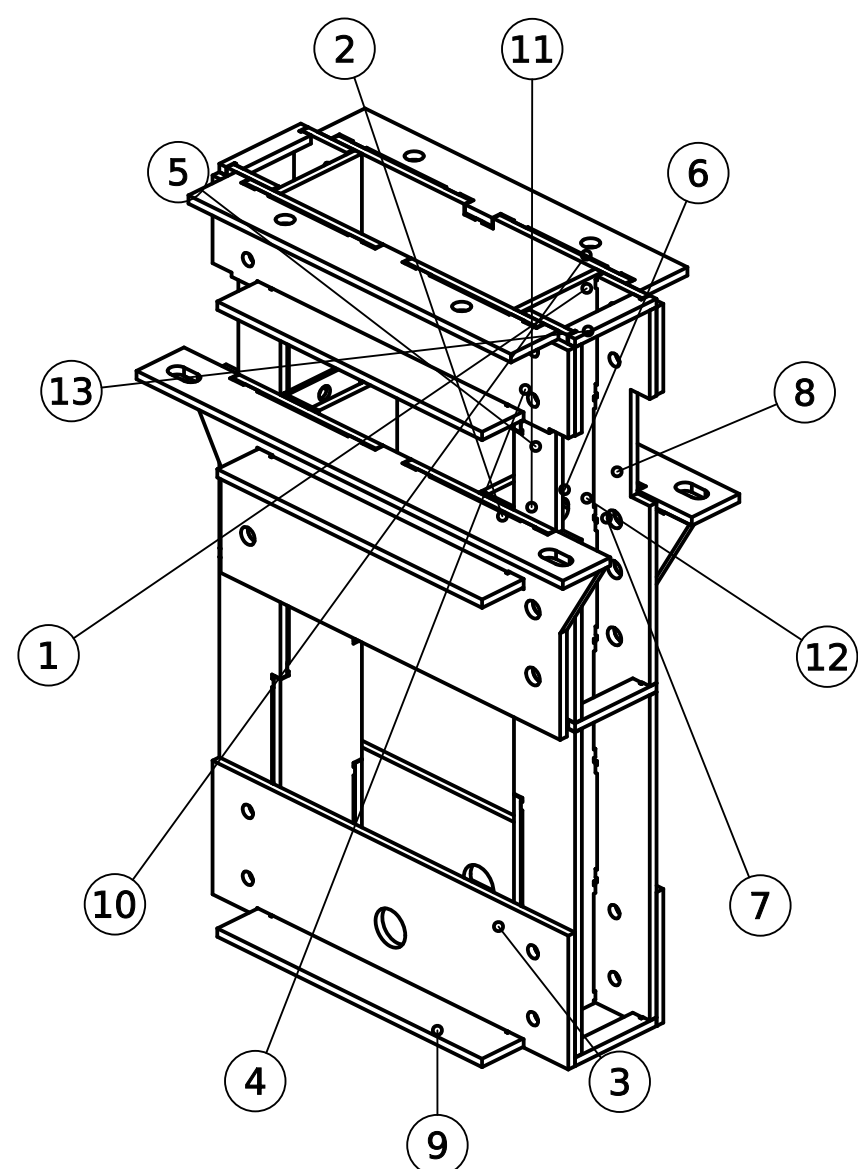

ISOMETRIC VIEW

- NOTES:
- 1. ALL DIMENSIONS IN INCHES. TOLERANCE $\pm 1/32$ UNLESS NOTED.
 - 2. BREAK SHARP EDGES, REMOVE BURRS.
 - 3. MATERIAL PER TITLE BLOCK. FILLET WELDS $1/4$ UNLESS NOTED.
 - 4. 40 FABRICATED PIECES, 13 PART NUMBERS.


13	6	Frame Channel Plate L-F13	1/2" plate, 1-1/4 x 6	1.0	OSEP6-P6-13
12	4	Compression Short Side Plat	1/4" plate, 2.600 x 9	1.3	OSEP6-P6-12
11	4	Compression Short Side Plat	1/4" plate, 2 x 6	0.8	OSEP6-P6-11
10	2	Frame Channel Plate L-F5	1/2" plate, 3-1/2 x 23-3/4	9.9	OSEP6-P6-10
9	6	Frame Base Plate L-F6	1/2" plate, 3-1/2 x 19-1/2	8.4	OSEP6-P6-09
8	2	Chamber Wall Plate L-F10	1/2" plate, 3-1/2 x 31.400	13.3	OSEP6-P6-08
7	2	Chamber Wall Plate L-F9	1/2" plate, 12 x 31.046	43.5	OSEP6-P6-07
6	4	Frame Round Bar L-F3	1/2" plate, 4-1/2 x 43-1/2	23.9	OSEP6-P6-06
5	2	Frame Channel Plate L-F4	1/2" plate, 6 x 43-1/2	32.9	OSEP6-P6-05
4	2	Main Frame - Dirt Blockers	1/2" plate, 2 x 5.900	1.7	OSEP6-P6-04
3	2	Main Frame Channel L-F2	1/2" plate, 8 x 26.200	28.8	OSEP6-P6-03
2	2	Short Side Channel L-F12	1/2" plate, 6 x 9	7.5	OSEP6-P6-02
1	2	Frame Channel L-F1	1/2" plate, 6 x 26.200	21.2	OSEP6-P6-01
Item	Qty	Title	Stock	lb ea	Drawing no.
Material		Qty	Scale	Units	Projection
See parts list		1	1:10	inch	
Created by		Approved by	Document type		Status
J. Clements III		-	Assembly drawing		Draft
Legal owner		Title		Identification number	Sheet
J. Clements III		Main Frame OSE CEB Press 6, module 1		OSEP6-P6-S1	2/94
CEB Project				Rev A	

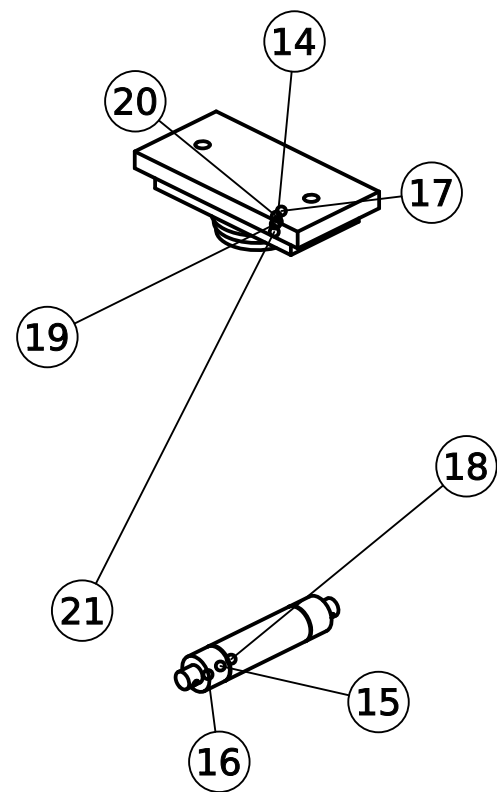

ISOMETRIC VIEW

- NOTES:
- 1. ALL DIMENSIONS IN INCHES. TOLERANCE $\pm 1/32$ UNLESS NOTED.
 - 2. BREAK SHARP EDGES, REMOVE BURRS.
 - 3. MATERIAL PER TITLE BLOCK. FILLET WELDS $1/4$ UNLESS NOTED.
 - 4. 9 FABRICATED PIECES, 8 PART NUMBERS.
 - 5. PURCHASED: 2X 01-166-01-0; 1X 01-187-00-0 PMC-21012


21	1	Cylinder Foot Plate L-O13	4-1/4 x 4-1/4 x 1/2 (see m	1.2	OSEP6-P6-21
20	1	Cylinder Foot Plate L-O12	4-3/4 x 4-3/4 x 1/2 (see m	1.7	OSEP6-P6-20
19	1	Cylinder Foot Plate L-O11	4-1/2 x 4-1/2 x 1/2 (see m	1.4	OSEP6-P6-19
18	1	1/4 X 2-1/2 Round Tube X 5-	1/4 X 2-1/2 ROUND TUBE X 5	3.9	OSEP6-P6-18
17	1	Upper Press Foot (AR300)	1 X 6 X 12 PLATE	20.2	OSEP6-P6-17
16	2	Main Frame - Horizontal Mem	TUBE, DOM 2" OD X 1.5" ID	1.0	OSEP6-P6-16
15	1	Main Frame - Cylinder Pin	1-1/2 ROUND BAR X 11	2.4	OSEP6-P6-15
14	1	Main Cylinder - Lower Press	FLAT BAR, FB1X4	13.9	OSEP6-P6-14
Item	Qty	Title	Stock	lb ea	Drawing no.
Material See parts list			Qty 1	Scale 1:10	Units inch
Created by J. Clements III			Approved by -	Document type Assembly drawing	Projection 
Legal owner J. Clements III CEB Project		Title Press Cylinder and Foot OSE CEB Press 6, module 2		Identification number OSEP6-P6-S2	
				Rev A	Date of issue 2026-10-04
				Sheet 3/94	

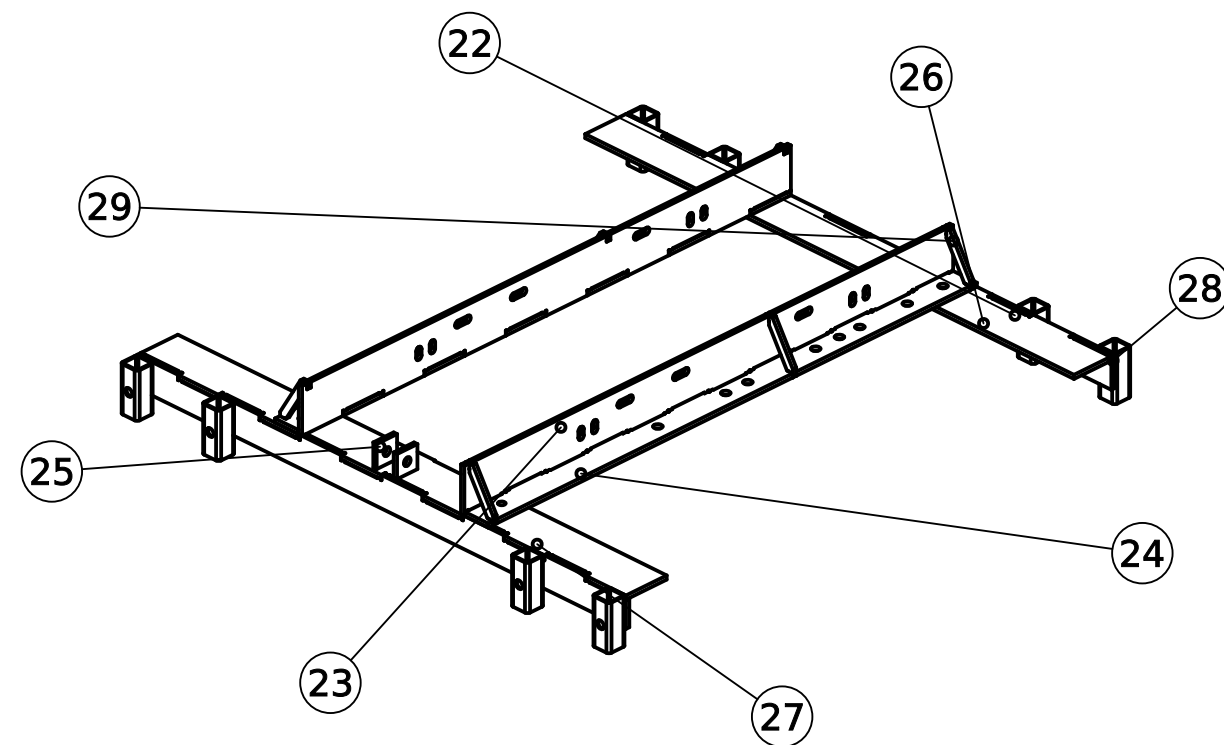

ISOMETRIC VIEW

- NOTES:
- 1. ALL DIMENSIONS IN INCHES. TOLERANCE $\pm 1/32$ UNLESS NOTED.
 - 2. BREAK SHARP EDGES, REMOVE BURRS.
 - 3. MATERIAL PER TITLE BLOCK. FILLET WELDS $1/4$ UNLESS NOTED.
 - 4. 24 FABRICATED PIECES, 8 PART NUMBERS.
 - 5. PURCHASED: 8X 211 - HEX NUT_AI_HNUT 0.7500-10-D-C


29	6	Primary Arm Plate L-A6	1/2" plate, 1.179 x 7.175	0.9	OSEP6-P6-29
28	8	Leg Holder Tube	3/16 X 2-1/2 SQUARE TUBE X	2.8	OSEP6-P6-28
27	1	Rear Secondary Arm Plate L-	1/2" plate, 6-1/8 x 72	57.4	OSEP6-P6-27
26	1	Rear Secondary Arm Plate L-	1/2" plate, 6 x 72	57.7	OSEP6-P6-26
25	2	Secondary Arms - Eye for 2n	1/2" plate, 3 x 3	1.2	OSEP6-P6-25
24	2	Primary Arm L-A1	1/2" plate, 4 x 72	36.5	OSEP6-P6-24
23	2	Primary Arm L-A2	1/2" plate, 5.966 x 72	56.3	OSEP6-P6-23
22	2	Secondary Arm L-A3	1/2" plate, 4 x 72	37.8	OSEP6-P6-22
Item	Qty	Title	Stock	lb ea	Drawing no.
Material		Qty	Scale	Units	Projection
See parts list		1	1:20	inch	
Created by		Approved by	Document type		Status
J. Clements III		-	Assembly drawing		Draft
Legal owner		Title		Identification number	Sheet
J. Clements III		Arms		OSEP6-P6-S3	4/94
CEB Project		OSE CEB Press 6, module 3		Rev A	
				Date of issue	
				2026-10-04	

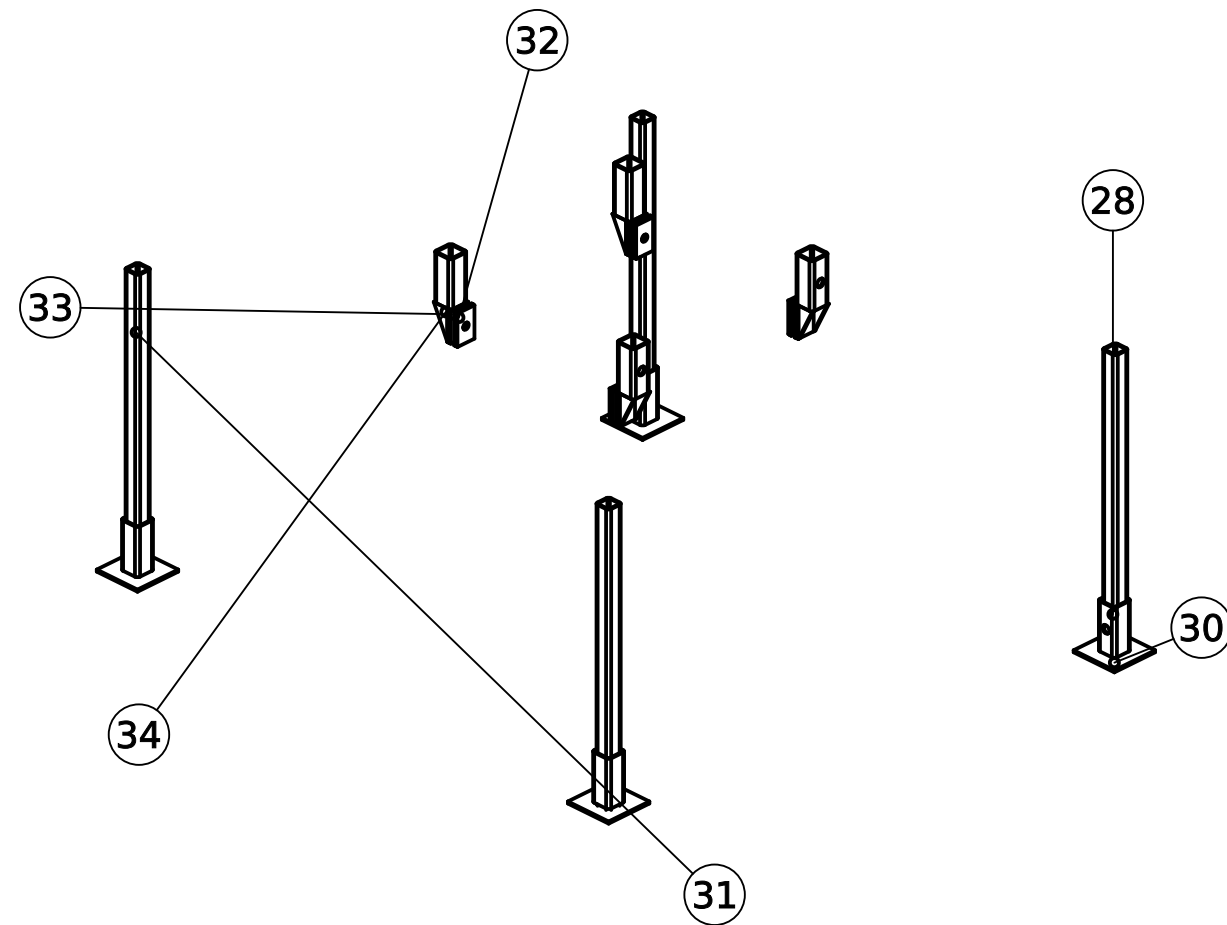

ISOMETRIC VIEW

NOTES:
1. ALL DIMENSIONS IN INCHES. TOLERANCE $\pm 1/32$ UNLESS NOTED.
2. BREAK SHARP EDGES, REMOVE BURRS.
3. MATERIAL PER TITLE BLOCK. FILLET WELDS $1/4$ UNLESS NOTED.
4. 40 FABRICATED PIECES, 6 PART NUMBERS.
5. PURCHASED: 8X 211 - HEX NUT_AI_HNUT 0.7500-10-D-C; 4X HEX BOLT_AI_2_HBOLT 0.7500-10X3


34	8	Support Holder Plate L-Q15	1/4" plate, 2 x 4	0.3	OSEP6-P6-34		
33	8	Support Holder Plate L-Q9	1/4" plate, 2-1/2 x 4	0.7	OSEP6-P6-33		
32	8	Support Holder Part 01-247	1/4" plate, 2-9/16 x 4	0.7	OSEP6-P6-32		
31	4	Leg	3/16 X 2 SQUARE TUBE X 36	13.0	OSEP6-P6-31		
30	4	Foot Plate L-Q17	1/4" plate, 6 x 6	2.6	OSEP6-P6-30		
28	8	Leg Holder Tube	3/16 X 2-1/2 SQUARE TUBE X	2.8	OSEP6-P6-28		
Item	Qty	Title	Stock	lb ea	Drawing no.		
Material See parts list			Qty 1	Scale 1:20	Units inch	Projection 	
Created by J. Clements III		Approved by -		Document type Assembly drawing		Status Draft	
Legal owner J. Clements III CEB Project		Title Feet and Legs OSE CEB Press 6, module 4			Identification number OSEP6-P6-S4		Sheet 5/94
					Rev A	Date of issue 2026-10-04	

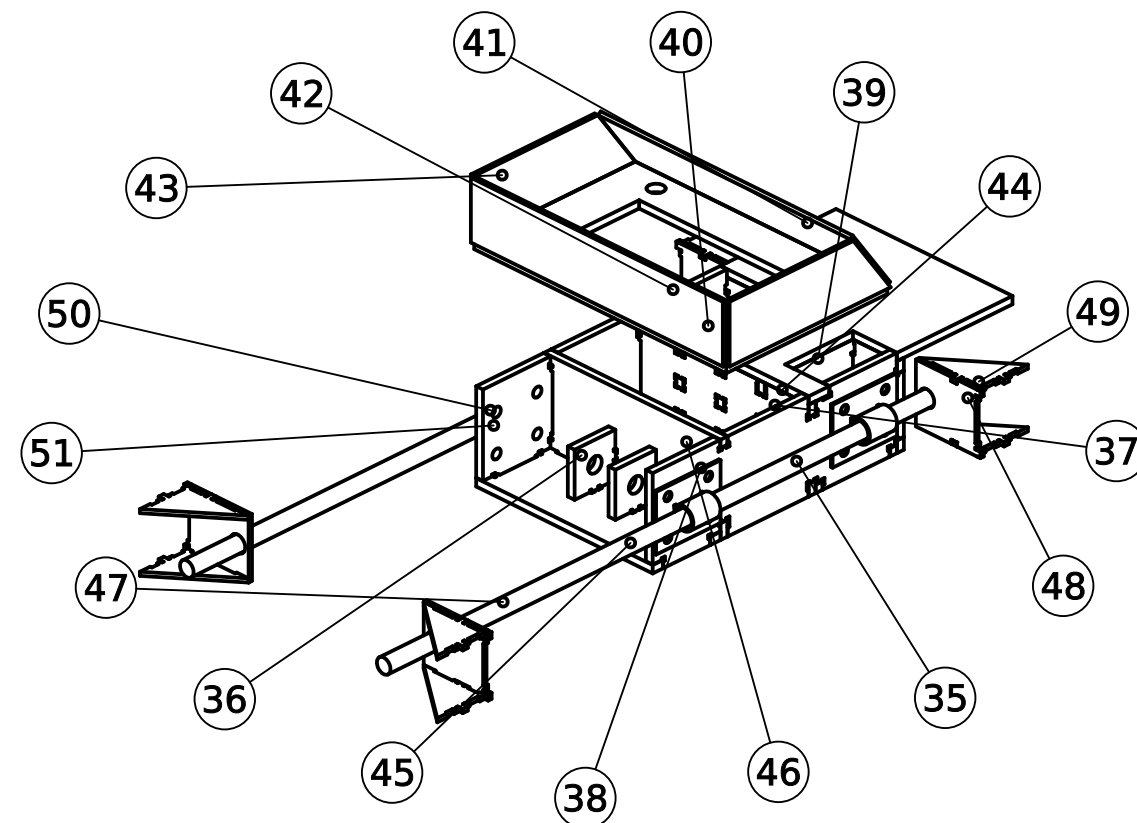

ISOMETRIC VIEW

NOTES:
1. ALL DIMENSIONS IN INCHES. TOLERANCE $\pm 1/32$ UNLESS NOTED.
2. BREAK SHARP EDGES, REMOVE BURRS.
3. MATERIAL PER TITLE BLOCK. FILLET WELDS 1/4 UNLESS NOTED.
4. 40 FABRICATED PIECES, 17 PART NUMBERS.
5. PURCHASED: 8X .5 HN; 2X 01-102-01-0; 1X 01-185-00-0 - 25TL14-112; 4X 01-230-00-0 L-Q10; 12X 01-231-00-0 L-H7; 4X 01-233-00-0; 4X 5700K14; 4X 5700K14_2


51	4	Part 01-286	round / tube, 1-1/2 dia x	0.3	OSEP6-P6-51
50	4	Plate L-H19	1/8" plate, 3-3/4 x 4-3/4	0.5	OSEP6-P6-50
49	8	Shaft Support Plate L-Q12	1/4" plate, 2.763 x 5.701	0.5	OSEP6-P6-49
48	4	Shaft Support Plate L-Q11	1/4" plate, 4 x 4-3/4	1.2	OSEP6-P6-48
47	2	Drawer Guide Rod	1IN ROUND BAR X 48IN	9.8	OSEP6-P6-47
46	1	Drawer Plate L-D6	1/2" plate, 6 x 13	10.1	OSEP6-P6-46
45	1	Drawer Plate L-D8	1/2" plate, 5 x 13	8.3	OSEP6-P6-45
44	3	Drawer Plate L-D4	1/2" plate, 5-1/2 x 7	4.6	OSEP6-P6-44
43	2	Saddle Plate L-Q4	1/4" plate, 3-7/8 x 11.863	2.9	OSEP6-P6-43
42	1	Saddle Plate L-Q3	1/4" plate, 3-7/8 x 18.558	5.1	OSEP6-P6-42
41	1	Saddle Plate L-Q5	1/4" plate, 4-3/4 x 18.558	6.2	OSEP6-P6-41
40	1	Saddle Plate L-F8	1/2" plate, 11.863 x 18.55	19.3	OSEP6-P6-40
39	1	Soil Loading Drawer - Roof	1/2" plate, 13 x 15	23.0	OSEP6-P6-39
38	2	Drawer Side L-D2	1/2" plate, 6 x 18-1/2	14.6	OSEP6-P6-38
37	2	Soil Loading Drawer - Verti	1/2" plate, 5-1/2 x 13	8.7	OSEP6-P6-37
36	2	Soil Loading Drawer - Tongu	1/2" plate, 3-1/2 x 3-1/2	1.2	OSEP6-P6-36
35	1	Soil Loading Drawer - Press	1/2" plate, 6 x 13	9.6	OSEP6-P6-35
Item	Qty	Title	Stock	lb ea	Drawing no.
Material		Qty	Scale	Units	Projection
See parts list		1	1:10	inch	
Created by		Approved by	Document type		Status
J. Clements III		-	Assembly drawing		Draft
Legal owner		Title		Identification number	Sheet
J. Clements III		Drawer		OSEP6-P6-S5	6/94
CEB Project		OSE CEB Press 6, module 5		Rev A Date of issue 2026-10-04	

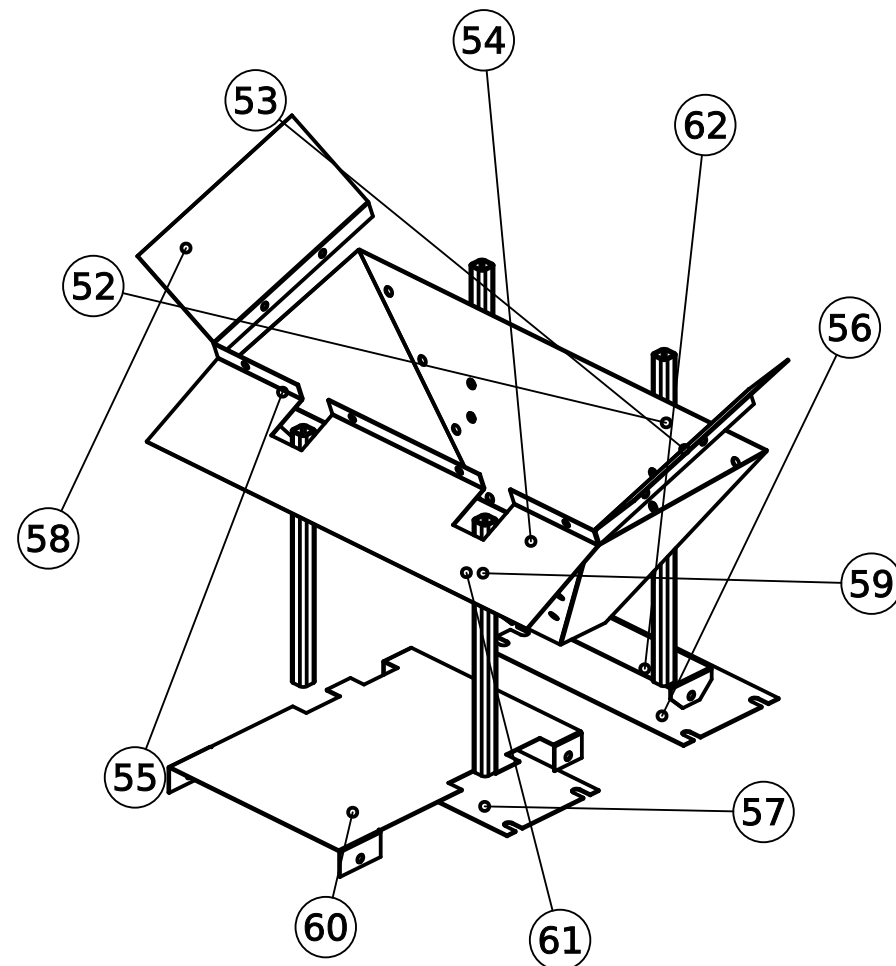

ISOMETRIC VIEW

NOTES:
1. ALL DIMENSIONS IN INCHES. TOLERANCE $\pm 1/32$ UNLESS NOTED.
2. BREAK SHARP EDGES, REMOVE BURRS.
3. MATERIAL PER TITLE BLOCK. FILLET WELDS $1/4$ UNLESS NOTED.
4. 15 FABRICATED PIECES, 11 PART NUMBERS.
5. PURCHASED: 4X 01-066-00-0_2; 8X 01-066-00-0_3; 6X 211 - HEX NUT_AI_HNUT
0.7500-10-D-C


62	1	Guard L-H10	1/8" sheet, bent, 31.1 x 6	6.4	OSEP6-P6-62		
61	1	Front Soil Deflector L-H4	1/8" sheet, bent, 56.0 x 1	25.6	OSEP6-P6-61		
60	1	Guard L-H12	1/8" sheet, bent, 35.6 x 3	32.2	OSEP6-P6-60		
59	2	Grate Support Tube	3/16 X 2 SQUARE TUBE X 38	13.5	OSEP6-P6-59		
58	2	Side Soil Deflector L-H5	1/8" sheet, bent, 23.0 x 1	11.9	OSEP6-P6-58		
57	1	Dirt Keeper Plate L-H8	1/8" plate, 13-1/2 x 30	14.1	OSEP6-P6-57		
56	1	Brick Holder Plate L-H9	1/8" plate, 14 x 30	14.6	OSEP6-P6-56		
55	2	Hopper Side Sheet L-H1	1/8" plate, 23-5/16 x 38.2	19.6	OSEP6-P6-55		
54	1	Hopper Sheet L-H3	1/8" plate, 31 x 53.741	36.2	OSEP6-P6-54		
53	1	Hopper Sheet L-H2	1/8" plate, 30 x 60	38.2	OSEP6-P6-53		
52	2	Hopper Support	SQUARE TUBE, HSS2X2X1/4.	17.4	OSEP6-P6-52		
Item	Qty	Title	Stock	lb ea	Drawing no.		
Material See parts list			Qty 1	Scale 1:20	Units inch	Projection 	
Created by J. Clements III		Approved by -		Document type Assembly drawing		Status Draft	
Legal owner J. Clements III CEB Project		Title Hopper OSE CEB Press 6, module 6			Identification number OSEP6-P6-S6 Rev A Date of issue 2026-10-04		Sheet 7/94

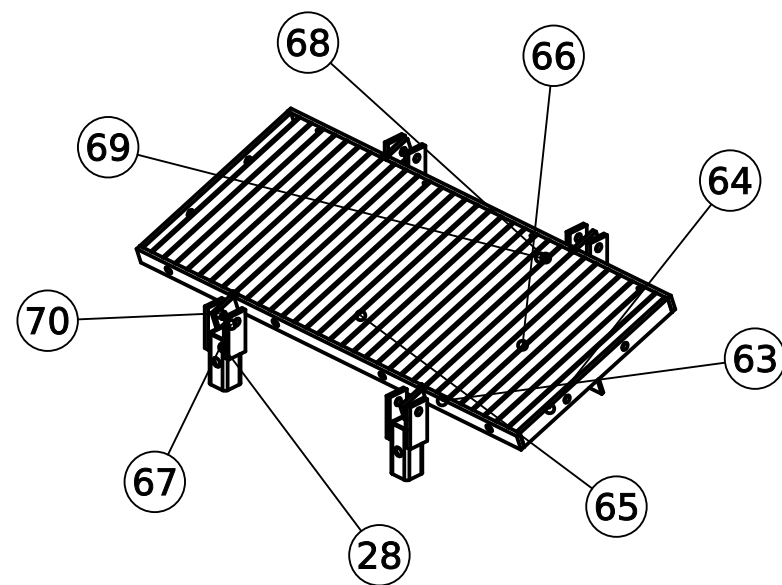

ISOMETRIC VIEW

- NOTES:
- 1. ALL DIMENSIONS IN INCHES. TOLERANCE $\pm 1/32$ UNLESS NOTED.
 - 2. BREAK SHARP EDGES, REMOVE BURRS.
 - 3. MATERIAL PER TITLE BLOCK. FILLET WELDS $1/4$ UNLESS NOTED.
 - 4. 54 FABRICATED PIECES, 9 PART NUMBERS.
 - 5. PURCHASED: 4X 211 - HEX NUT_AI_HNUT 0.7500-10-D-C


70	4	Grate Plate L-G3	1/2" plate, 2 x 3	0.8	OSEP6-P6-70
69	1	Rear Grate Hinge Plate L-Q1	1/4" plate, 2-1/2 x 24.276	4.3	OSEP6-P6-69
68	1	Rear Grate Hinge Plate L-Q1	1/4" plate, 6 x 29.276	12.5	OSEP6-P6-68
67	8	Grate Bracket Plate L-O7	1/2" plate, 2-1/2 x 5	1.7	OSEP6-P6-67
66	1	Soil Grate - Cross piece	FLAT BAR, FB1/4X2	7.9	OSEP6-P6-66
65	31	Grate Rod	ROUND BAR, RB1/2	3.3	OSEP6-P6-65
64	2	Grate Angle L-G1	1/2" plate, 2 x 23	6.4	OSEP6-P6-64
63	2	Grate Side L-G2	1/2" plate, 2-1/4 x 56	15.6	OSEP6-P6-63
28	4	Leg Holder Tube	3/16 X 2-1/2 SQUARE TUBE X	2.8	OSEP6-P6-28
Item	Qty	Title	Stock	lb ea	Drawing no.
Material		Qty	Scale	Units	Projection
See parts list		1	1:20	inch	
Created by		Approved by	Document type		Status
J. Clements III		-	Assembly drawing		Draft
Legal owner		Title		Identification number	Sheet
J. Clements III		Grate		OSEP6-P6-S7	8/94
CEB Project		OSE CEB Press 6, module 7		Rev A	
				Date of issue	
				2026-10-04	

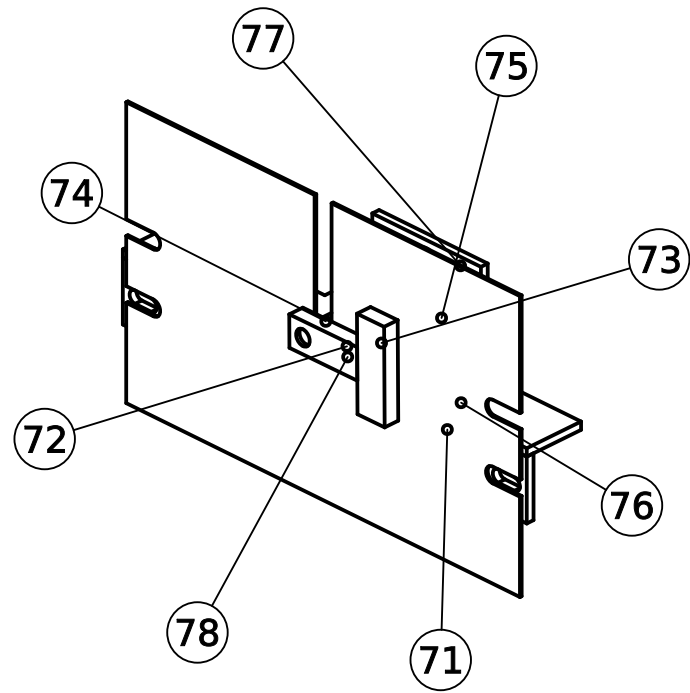

ISOMETRIC VIEW

NOTES:
1. ALL DIMENSIONS IN INCHES. TOLERANCE $\pm 1/32$ UNLESS NOTED.
2. BREAK SHARP EDGES, REMOVE BURRS.
3. MATERIAL PER TITLE BLOCK. FILLET WELDS $1/4$ UNLESS NOTED.
4. 8 FABRICATED PIECES, 8 PART NUMBERS.
5. PURCHASED: 2X 01-078-00-0; 1X 01-085-00-0; 1X 01-191-00-0; 1X 204 - SS-4-SAE-7_4_2; 1X 205 - SS-8-T_3; 2X 206 - MALE HEX NIPPLE, NPT_SS-8-HN_1_2; 1X 207 - SS-4-SAE-7_4_3; 1X 208 - SS-8-RB-4 ...


78	1	Shaker Frame Plate L-O5	1/2" plate, 4 x 7	2.2	OSEP6-P6-78
77	1	Shaker Frame Plate L-O4	1/2" plate, 3-1/2 x 8	2.6	OSEP6-P6-77
76	1	Shaker Frame Plate L-O3	1/2" plate, 8 x 29-3/4	20.9	OSEP6-P6-76
75	1	Shaker Motor Guard L-H6	1/8" plate, 18 x 29	17.8	OSEP6-P6-75
74	1	Shaker Shaft	ROUND BAR, RB1	1.6	OSEP6-P6-74
73	1	Soil Shaker - Hammer	FLAT BAR, FB1X2	3.4	OSEP6-P6-73
72	1	Soil Shaker - Hammer	1 X 2 FLAT X 5	2.6	OSEP6-P6-72
71	1	Shaker Mount Plate L-O2	1/2" plate, 4 x 29-3/4	16.5	OSEP6-P6-71
Item	Qty	Title	Stock	lb ea	Drawing no.
Material See parts list			Qty 1	Scale 1:10	Units inch
Created by J. Clements III			Approved by -	Document type Assembly drawing	Projection 
Legal owner J. Clements III CEB Project			Title Soil Shaker OSE CEB Press 6, module 8		Status Draft
			Identification number OSEP6-P6-S8		9/94
			Rev A	Date of issue 2026-10-04	

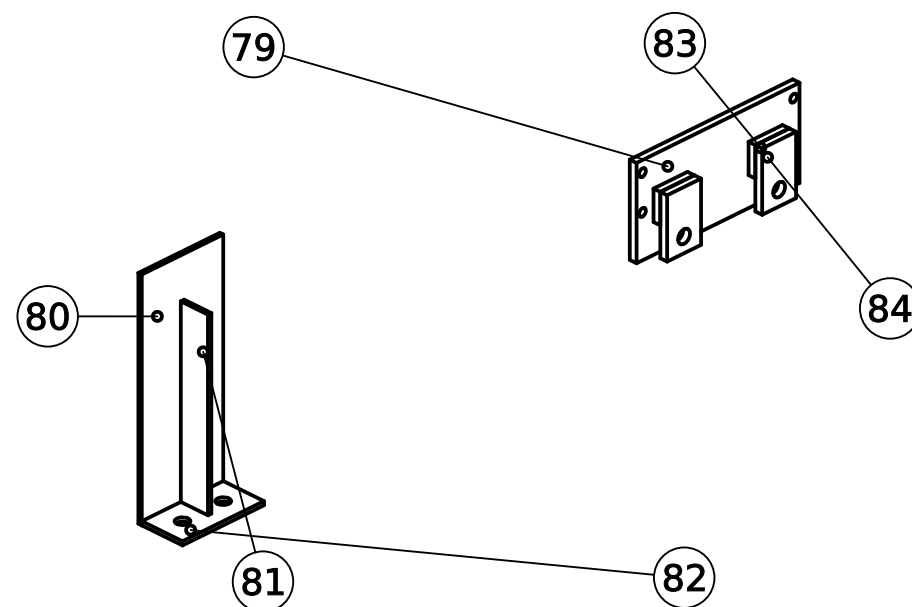

ISOMETRIC VIEW

NOTES:
1. ALL DIMENSIONS IN INCHES. TOLERANCE $\pm 1/32$ UNLESS NOTED.
2. BREAK SHARP EDGES, REMOVE BURRS.
3. MATERIAL PER TITLE BLOCK. FILLET WELDS 1/4 UNLESS NOTED.
4. 8 FABRICATED PIECES, 6 PART NUMBERS.
5. PURCHASED: 2X 211 - HEX NUT_AI_HNUT 0.7500-10-D-C; 4X 212 - .313-18 X; 2X 213 - HYVAIR-D05S-2C-12D-35 SOLENOID; 2X 214 - DAMANAD05S033S MOUNTING BRACKET; 1X 215 - DAMAN-AD05S033S VALVE BLOCK; 1X 216 - HYVAIR-D05S-2H-12D-35 SOLENOID


84	2	Valve Bracket Plate L-O8	1/2" plate, 2-1/2 x 3.966	1.3	OSEP6-P6-84
83	2	Valve Bracket Plate L-O9	1/2" plate, 2 x 2-1/2	0.7	OSEP6-P6-83
82	1	Controller Mount - Bottom p	1/4" plate, 3 x 6	1.2	OSEP6-P6-82
81	1	Controller Mount Back L-Q8	1/4" plate, 2 x 12	1.7	OSEP6-P6-81
80	1	Controller Plate L-Q6	1/4" plate, 6 x 15	6.4	OSEP6-P6-80
79	1	Valve Plate L-O1	1/2" plate, 6 x 12	10.1	OSEP6-P6-79
Item	Qty	Title	Stock	lb ea	Drawing no.
Material		Qty	Scale	Units	Projection
See parts list		1	1:10	inch	
Created by		Approved by	Document type		Status
J. Clements III		-	Assembly drawing		Draft
Legal owner		Title		Identification number	Sheet
J. Clements III		Controls		OSEP6-P6-S9	10/94
CEB Project		OSE CEB Press 6, module 9		Rev A	
				Date of issue	
				2026-10-04	

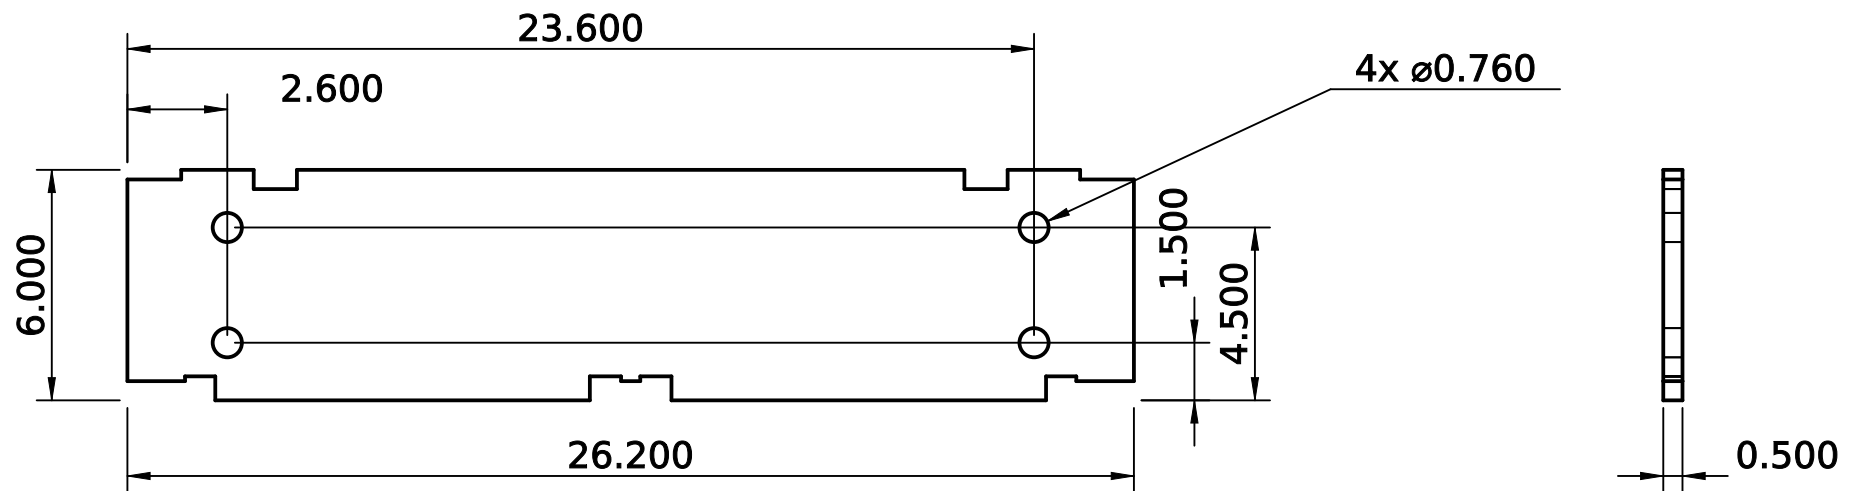

NOTES:

1. ALL DIMENSIONS IN INCHES. TOLERANCE $\pm 1/32$ UNLESS NOTED.
2. BREAK SHARP EDGES, REMOVE BURRS.
3. MATERIAL PER TITLE BLOCK. FILLET WELDS $1/4$ UNLESS NOTED.
4. OSE 01-014-00-0 / WELDMENT 001-0014, IN FRAME CHANNEL ASSEMBLY. USED IN: MAIN FRAME 2.
5. DXF LIBRARY L-F1: 26.200 X 6 X $1/2$ - MATCHES THE MODEL.
6. OSE 2015 WELDMENT REDRAW MAKES IT FROM CHANNEL, C6X13, STEEL INSTEAD.
7. GEOMETRY FROM OSE FULL_ASSEMBLY.STP (CEB PRESS 6); TITLE BLOCKS OF OSE'S 2D SET SAY 'CEB PRESS 5'.


Material 1/2" plate, 6 x 26.200		Qty 2	Scale 1:5	Units inch	Projection 
Created by J. Clements III		Approved by -		Document type Detail drawing	Status Draft
Legal owner J. Clements III CEB Project	Title Frame Channel L-F1 OSE CEB Press 6 (a-z Build 1.0)			Identification number OSEP6-P6-01	Sheet 11/94
				Rev A	

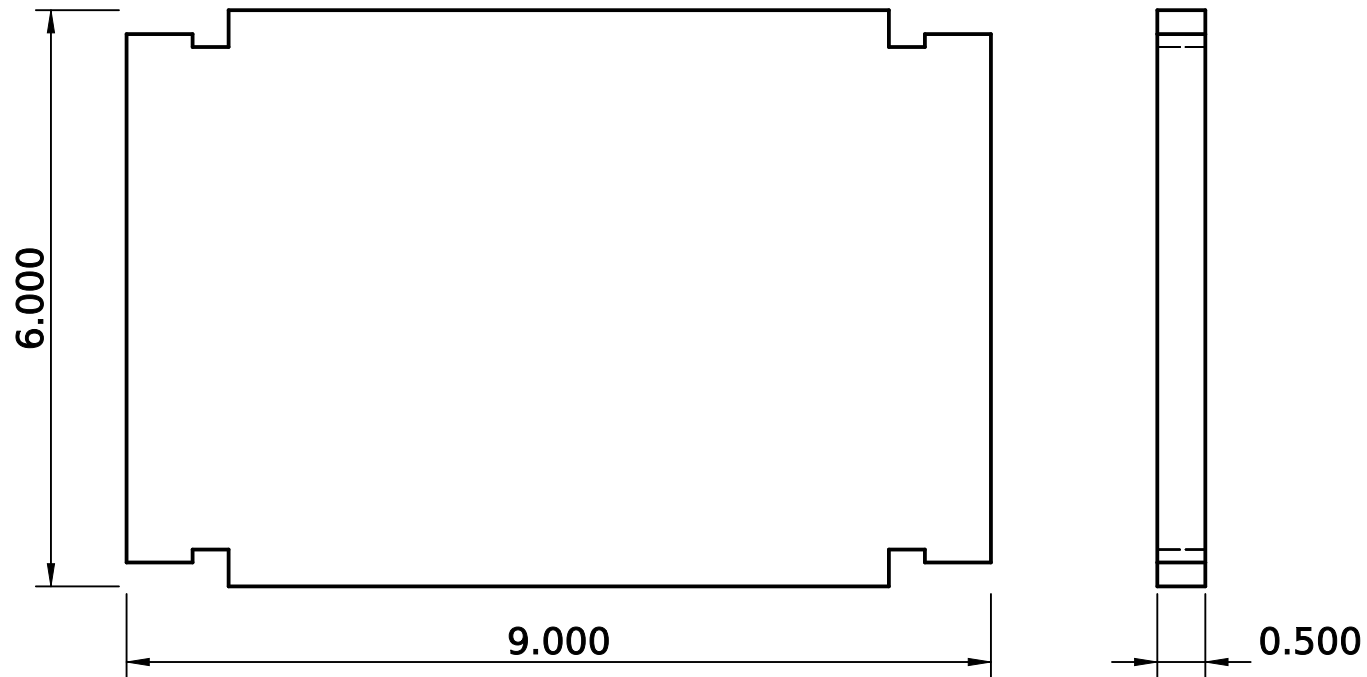

NOTES:

1. ALL DIMENSIONS IN INCHES. TOLERANCE $\pm 1/32$ UNLESS NOTED.
2. BREAK SHARP EDGES, REMOVE BURRS.
3. MATERIAL PER TITLE BLOCK. FILLET WELDS $1/4$ UNLESS NOTED.
4. OSE 01-034-00-0 / WELDMENT 001-0034, IN COMP SHORT SIDE ASSEMBLY. USED IN: MAIN FRAME 2.
5. DXF LIBRARY L-F12: 9 X 6 X $1/2$ - MATCHES THE MODEL.
6. OSE 2015 WELDMENT REDRAW MAKES IT FROM CHANNEL, C6X13, STEEL INSTEAD.
7. GEOMETRY FROM OSE FULL_ASSEMBLY.STP (CEB PRESS 6); TITLE BLOCKS OF OSE'S 2D SET SAY 'CEB PRESS 5'.


Material 1/2" plate, 6 x 9		Qty 2	Scale 1:2	Units inch	Projection 	
Created by J. Clements III		Approved by -		Document type Detail drawing	Status Draft	
Legal owner J. Clements III CEB Project	Title Short Side Channel L-F12 OSE CEB Press 6 (a-z Build 1.0)			Identification number OSEP6-P6-02		Sheet 12/94
				Rev A	Date of issue 2026-10-04	

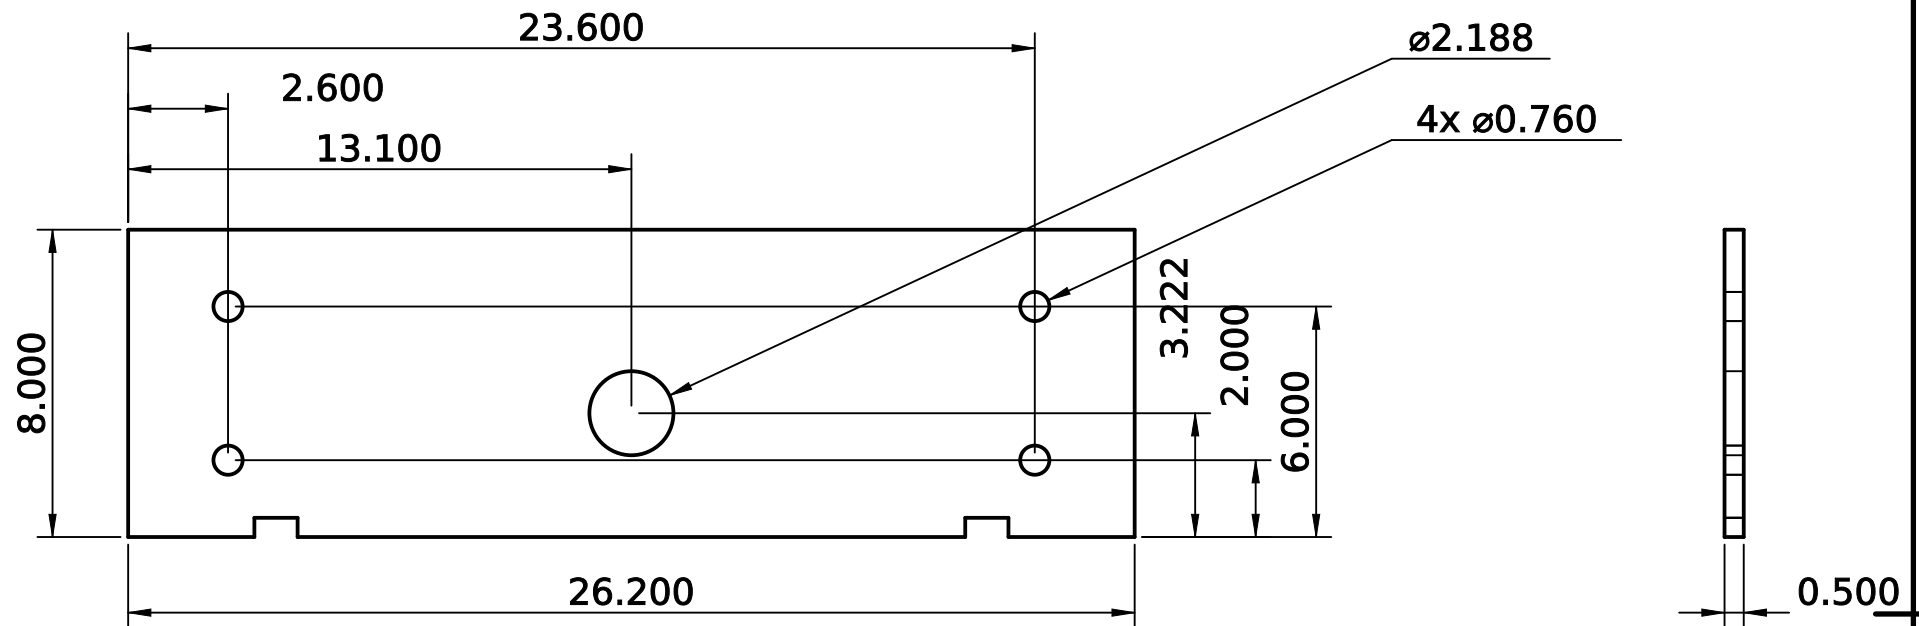

NOTES:

1. ALL DIMENSIONS IN INCHES. TOLERANCE $\pm 1/32$ UNLESS NOTED.
2. BREAK SHARP EDGES, REMOVE BURRS.
3. MATERIAL PER TITLE BLOCK. FILLET WELDS $1/4$ UNLESS NOTED.
4. OSE 01-041-00-0 / WELDMENT 001-0041, IN FRAME BASE WELDMENT. USED IN: MAIN FRAME 2.
5. DXF LIBRARY L-F2: 26.200 X 8 X $1/2$ - MATCHES THE MODEL.
6. OSE 2015 WELDMENT REDRAW MAKES IT FROM CHANNEL, C6X13, STEEL INSTEAD.
7. GEOMETRY FROM OSE FULL_ASSEMBLY.STP (CEB PRESS 6); TITLE BLOCKS OF OSE'S 2D SET SAY 'CEB PRESS 5'.


Material 1/2" plate, 8 x 26.200		Qty 2	Scale 1:5	Units inch	Projection 
Created by J. Clements III		Approved by -	Document type Detail drawing		Status Draft
Legal owner J. Clements III CEB Project	Title Main Frame Channel L-F2 OSE CEB Press 6 (a-z Build 1.0)			Identification number OSEP6-P6-03	Sheet 13/94
			Rev A	Date of issue 2026-10-04	

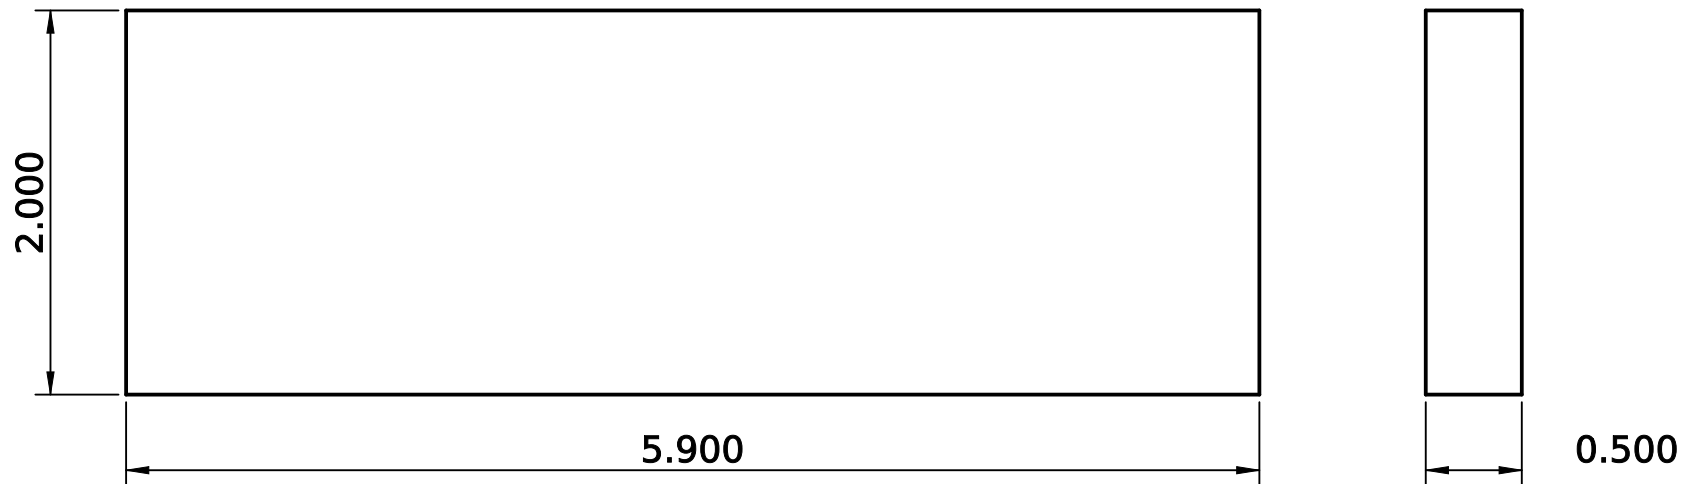

NOTES:

1. ALL DIMENSIONS IN INCHES. TOLERANCE $\pm 1/32$ UNLESS NOTED.
2. BREAK SHARP EDGES, REMOVE BURRS.
3. MATERIAL PER TITLE BLOCK. FILLET WELDS $1/4$ UNLESS NOTED.
4. OSE 01-107-00-0, IN FRAME CHANNEL ASSEMBLY. USED IN: MAIN FRAME 2.
5. DXF LIBRARY L-F7: 5.900 X 2 X $1/2$ - MATCHES THE MODEL.
6. GEOMETRY FROM OSE FULL_ASSEMBLY.STP (CEB PRESS 6); TITLE BLOCKS OF OSE'S 2D SET SAY 'CEB PRESS 5'.


Material 1/2" plate, 2 x 5.900		Qty 2	Scale 1:1	Units inch	Projection 	
Created by J. Clements III		Approved by -		Document type Detail drawing	Status Draft	
Legal owner J. Clements III CEB Project	Title Main Frame - Dirt Blockers L-F7 OSE CEB Press 6 (a-z Build 1.0)			Identification number OSEP6-P6-04		Sheet 14/94
				Rev A	Date of issue 2026-10-04	

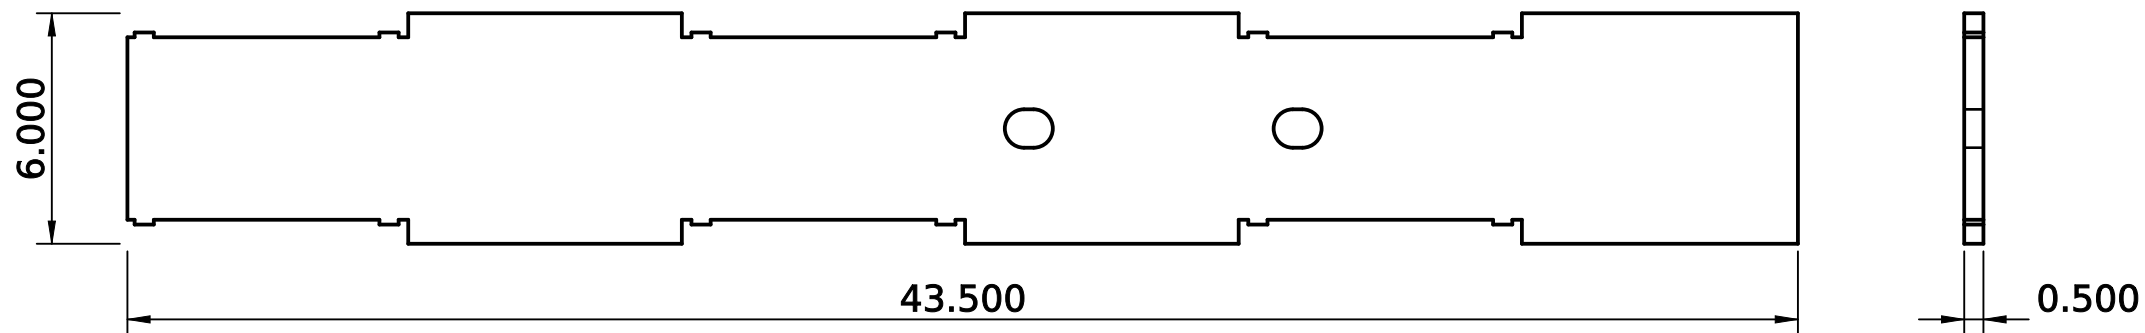

NOTES:

1. ALL DIMENSIONS IN INCHES. TOLERANCE $\pm 1/32$ UNLESS NOTED.
2. BREAK SHARP EDGES, REMOVE BURRS.
3. MATERIAL PER TITLE BLOCK. FILLET WELDS $1/4$ UNLESS NOTED.
4. OSE 01-115-00-0, IN FRAME CHANNEL ASSEMBLY. USED IN: MAIN FRAME 2.
5. DXF LIBRARY L-F4: 43-1/2 X 6 X 1/2 - MATCHES THE MODEL.
6. GEOMETRY FROM OSE FULL_ASSEMBLY.STP (CEB PRESS 6); TITLE BLOCKS OF OSE'S 2D SET SAY 'CEB PRESS 5'.


Material 1/2" plate, 6 x 43-1/2		Qty 2	Scale 1:5	Units inch	Projection 	
Created by J. Clements III		Approved by -		Document type Detail drawing	Status Draft	
Legal owner J. Clements III CEB Project	Title Frame Channel Plate L-F4 OSE CEB Press 6 (a-z Build 1.0)			Identification number OSEP6-P6-05		Sheet 15/94
				Rev A	Date of issue 2026-10-04	

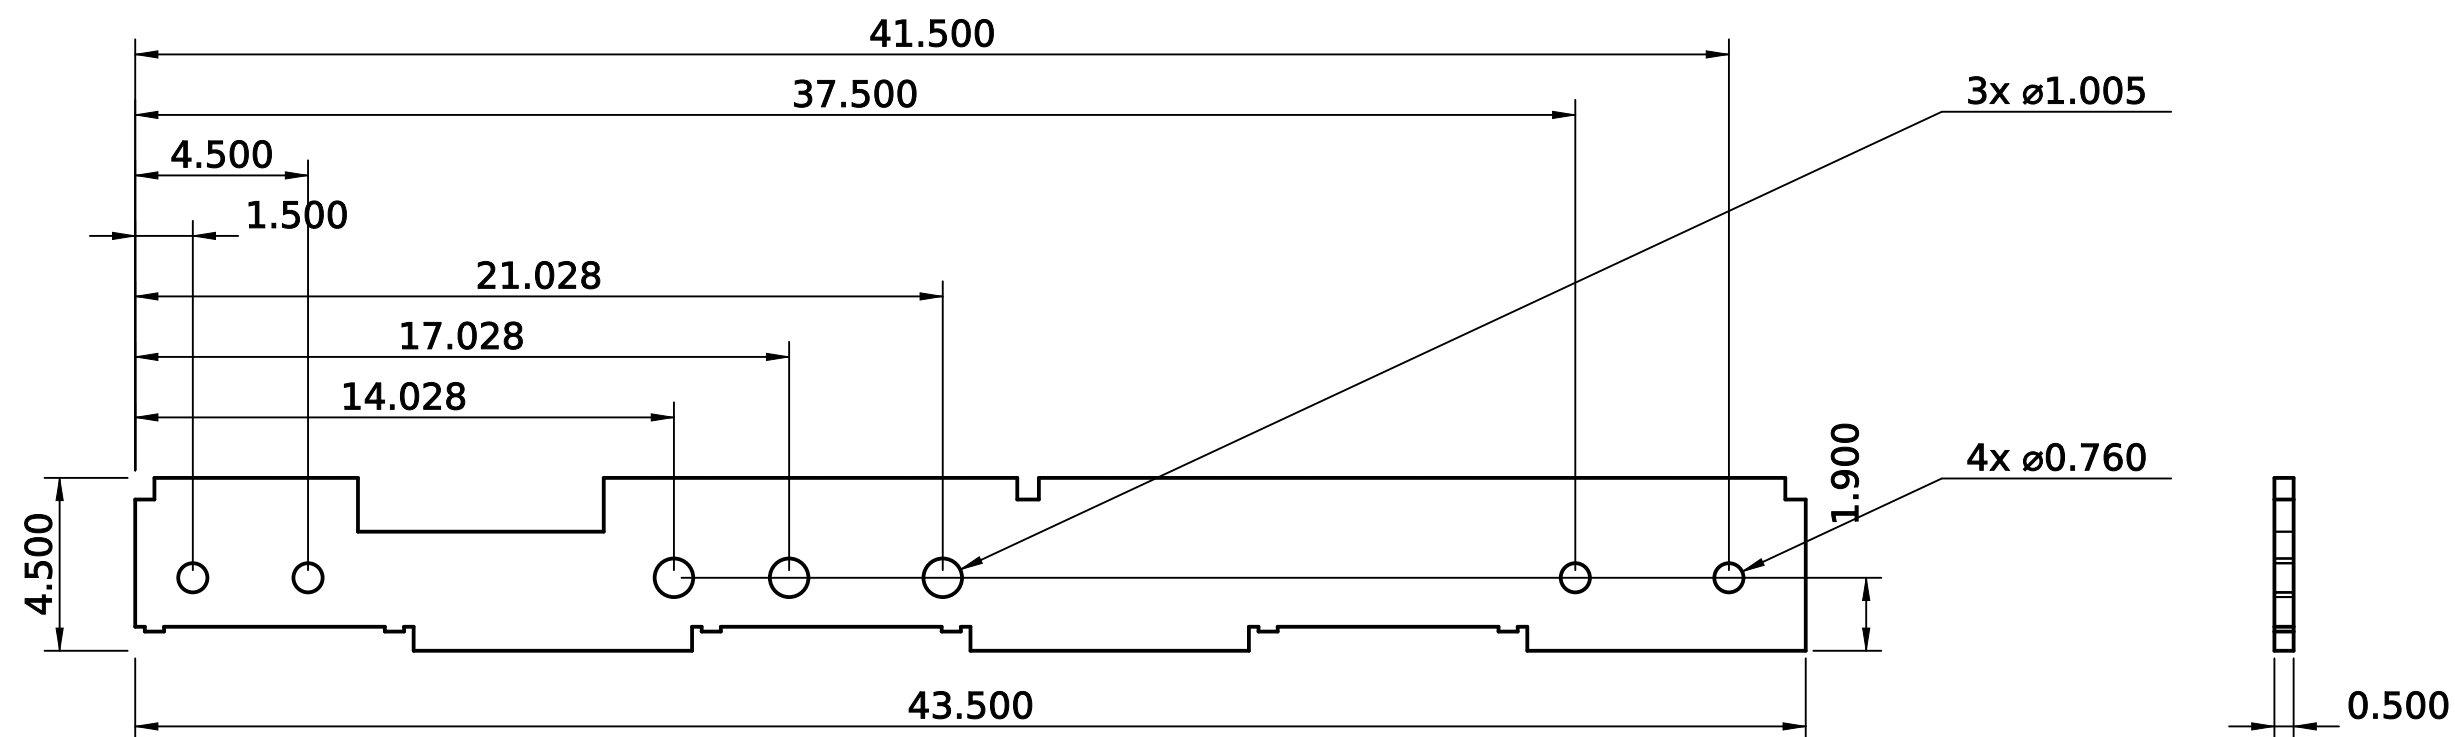

NOTES:

1. ALL DIMENSIONS IN INCHES. TOLERANCE $\pm 1/32$ UNLESS NOTED.
2. BREAK SHARP EDGES, REMOVE BURRS.
3. MATERIAL PER TITLE BLOCK. FILLET WELDS $1/4$ UNLESS NOTED.
4. OSE 01-120-00-0 / WELDMENT 001-0120, IN FRAME CHANNEL ASSEMBLY. USED IN: MAIN FRAME 4.
5. DXF LIBRARY L-F3: 43-1/2 X 4-1/2 X 1/2 - MATCHES THE MODEL.
6. OSE 2015 WELDMENT REDRAW MAKES IT FROM ROUND BAR, STEEL, RB1-1/2 INSTEAD.
7. GEOMETRY FROM OSE FULL_ASSEMBLY.STP (CEB PRESS 6); TITLE BLOCKS OF OSE'S 2D SET SAY 'CEB PRESS 5'.


Material 1/2" plate, 4-1/2 x 43-1/2		Qty 4	Scale 1:5	Units inch	Projection
Created by J. Clements III		Approved by -		Document type Detail drawing	Status Draft
Legal owner J. Clements III CEB Project		Title Frame Round Bar L-F3 OSE CEB Press 6 (a-z Build 1.0)		Identification number OSEP6-P6-06	Sheet 16/94
				Rev A	Date of issue 2026-10-04

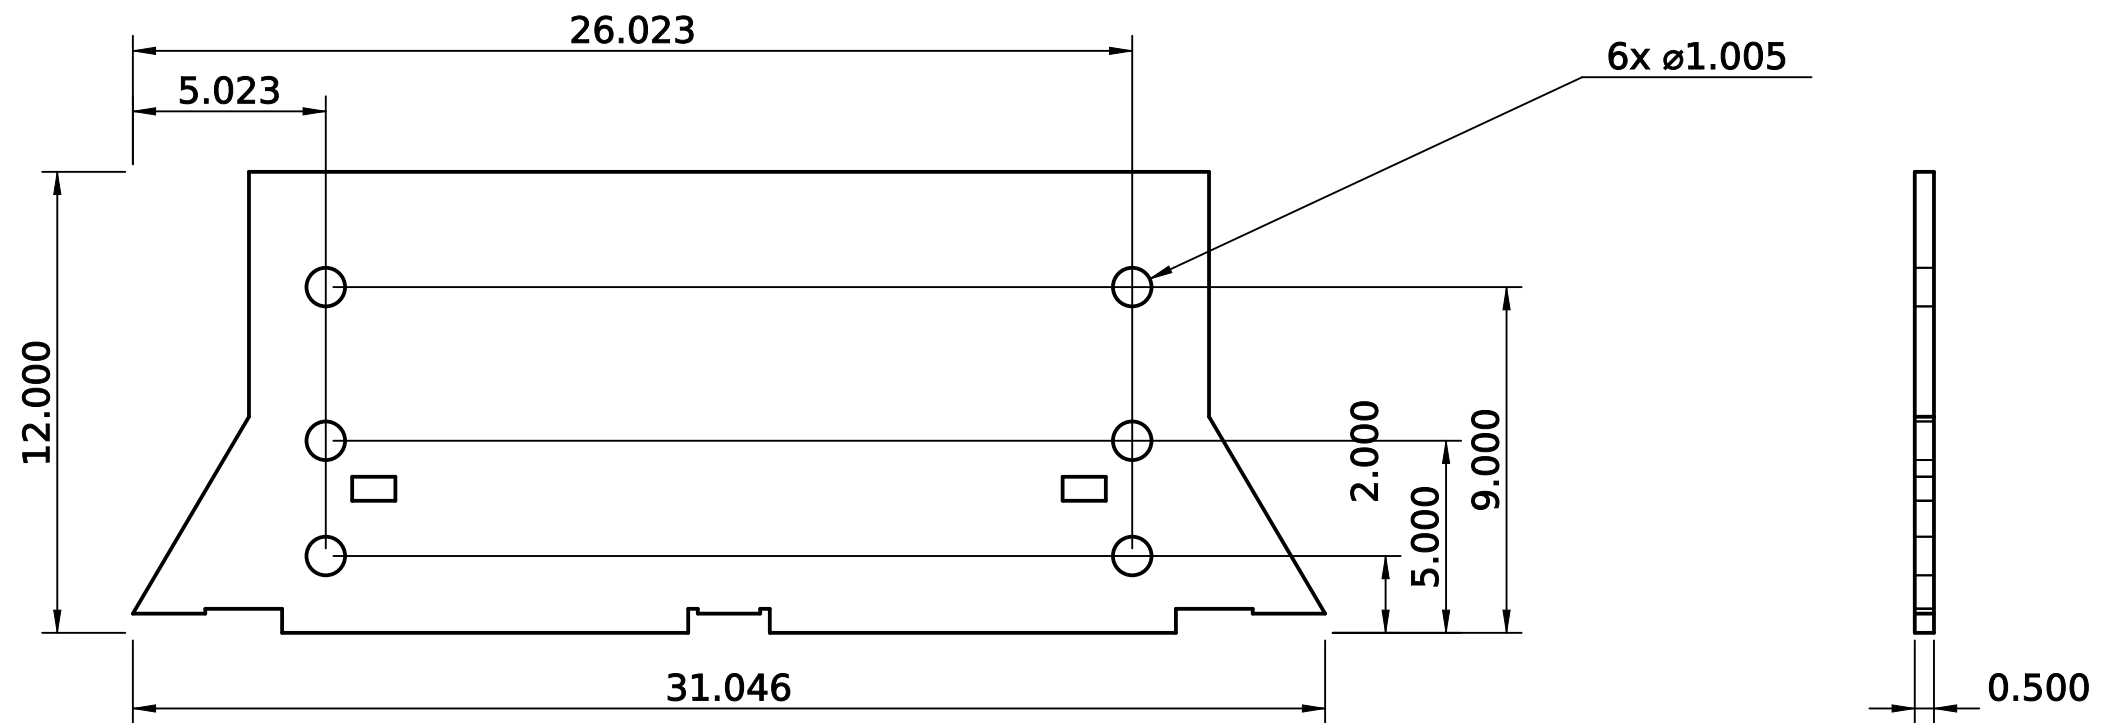

NOTES:

1. ALL DIMENSIONS IN INCHES. TOLERANCE $\pm 1/32$ UNLESS NOTED.
2. BREAK SHARP EDGES, REMOVE BURRS.
3. MATERIAL PER TITLE BLOCK. FILLET WELDS $1/4$ UNLESS NOTED.
4. OSE 01-122-00-0, IN CHAMBER WALL ASSEMBLY. USED IN: MAIN FRAME 2.
5. DXF LIBRARY L-F9: 31.046 X 12 X $1/2$ - MATCHES THE MODEL.
6. GEOMETRY FROM OSE FULL_ASSEMBLY.STP (CEB PRESS 6); TITLE BLOCKS OF OSE'S 2D SET SAY 'CEB PRESS 5'.


Material 1/2" plate, 12 x 31.046		Qty 2	Scale 1:5	Units inch	Projection 
Created by J. Clements III		Approved by -		Document type Detail drawing	
Legal owner J. Clements III CEB Project		Title Chamber Wall Plate L-F9 OSE CEB Press 6 (a-z Build 1.0)		Identification number OSEP6-P6-07	Sheet 17/94
				Rev A	Date of issue 2026-10-04

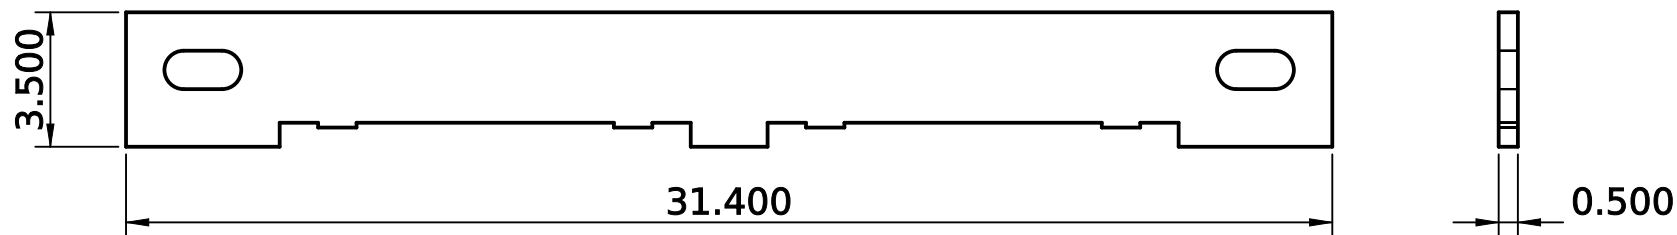

NOTES:

1. ALL DIMENSIONS IN INCHES. TOLERANCE $\pm 1/32$ UNLESS NOTED.
2. BREAK SHARP EDGES, REMOVE BURRS.
3. MATERIAL PER TITLE BLOCK. FILLET WELDS $1/4$ UNLESS NOTED.
4. OSE 01-123-00-0, IN CHAMBER WALL ASSEMBLY. USED IN: MAIN FRAME 2.
5. DXF LIBRARY L-F10: 31.400 X 3-1/2 X 1/2 - MATCHES THE MODEL.
6. GEOMETRY FROM OSE FULL_ASSEMBLY.STP (CEB PRESS 6); TITLE BLOCKS OF OSE'S 2D SET SAY 'CEB PRESS 5'.


Material 1/2" plate, 3-1/2 x 31.400		Qty 2	Scale 1:5	Units inch	Projection 
Created by J. Clements III		Approved by -		Document type Detail drawing	Status Draft
Legal owner J. Clements III CEB Project	Title Chamber Wall Plate L-F10 OSE CEB Press 6 (a-z Build 1.0)			Identification number OSEP6-P6-08	Sheet 18/94
				Rev A	

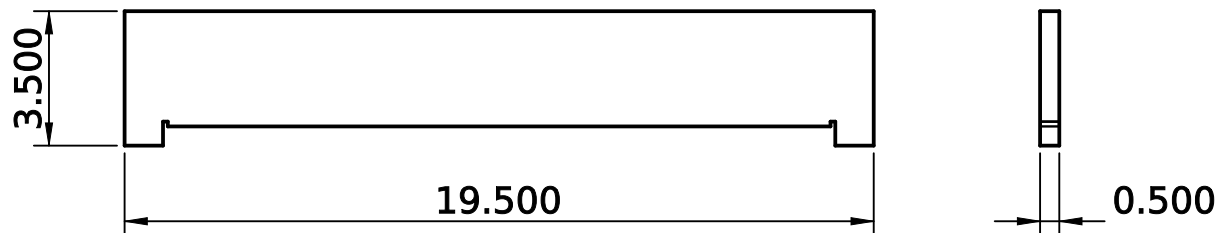

NOTES:

1. ALL DIMENSIONS IN INCHES. TOLERANCE $\pm 1/32$ UNLESS NOTED.
2. BREAK SHARP EDGES, REMOVE BURRS.
3. MATERIAL PER TITLE BLOCK. FILLET WELDS $1/4$ UNLESS NOTED.
4. OSE 01-124-00-0, IN CHAMBER WALL ASSEMBLY, FRAME BASE WELDMENT, FRAME CHANNEL ASSEMBLY. USED IN: MAIN FRAME 6.
5. DXF LIBRARY L-F6: $19-1/2 \times 3-1/2 \times 1/2$ - MATCHES THE MODEL.
6. GEOMETRY FROM OSE FULL_ASSEMBLY.STP (CEB PRESS 6); TITLE BLOCKS OF OSE'S 2D SET SAY 'CEB PRESS 5'.


Material 1/2" plate, 3-1/2 x 19-1/2		Qty 6	Scale 1:5	Units inch	Projection 	
Created by J. Clements III		Approved by -		Document type Detail drawing	Status Draft	
Legal owner J. Clements III CEB Project	Title Frame Base Plate L-F6 OSE CEB Press 6 (a-z Build 1.0)			Identification number OSEP6-P6-09		Sheet 19/94
				Rev A	Date of issue 2026-10-04	

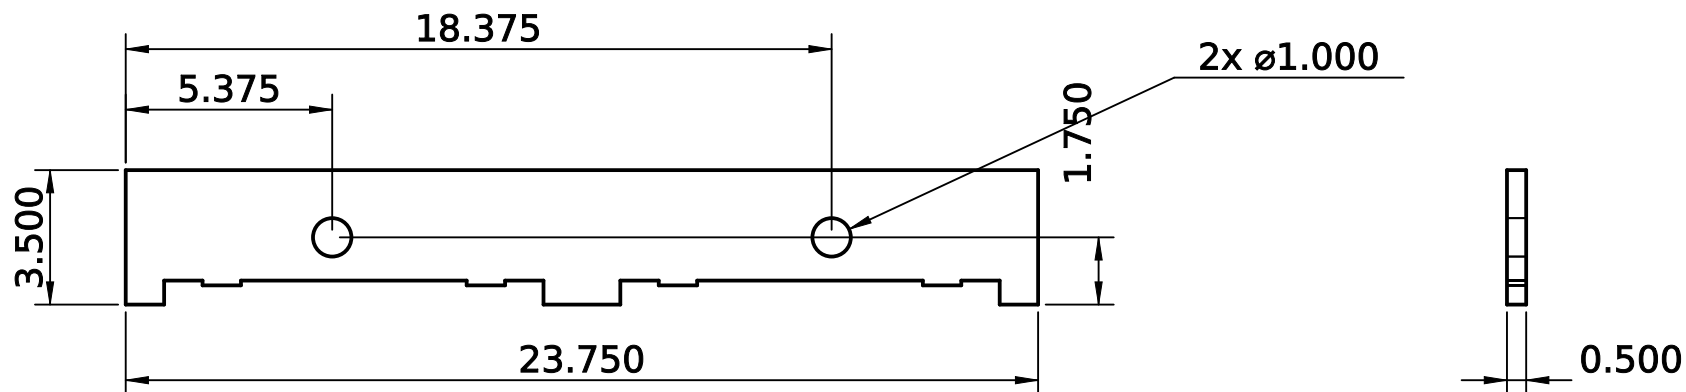

NOTES:

1. ALL DIMENSIONS IN INCHES. TOLERANCE $\pm 1/32$ UNLESS NOTED.
2. BREAK SHARP EDGES, REMOVE BURRS.
3. MATERIAL PER TITLE BLOCK. FILLET WELDS $1/4$ UNLESS NOTED.
4. OSE 01-131-00-0, IN FRAME CHANNEL ASSEMBLY. USED IN: MAIN FRAME 2.
5. DXF LIBRARY L-F5: $23-3/4 \times 3-1/2 \times 1/2$ - MATCHES THE MODEL.
6. GEOMETRY FROM OSE FULL_ASSEMBLY.STP (CEB PRESS 6); TITLE BLOCKS OF OSE'S 2D SET SAY 'CEB PRESS 5'.


Material 1/2" plate, 3-1/2 x 23-3/4		Qty 2	Scale 1:5	Units inch	Projection 
Created by J. Clements III		Approved by -	Document type Detail drawing		Status Draft
Legal owner J. Clements III CEB Project		Title Frame Channel Plate L-F5 OSE CEB Press 6 (a-z Build 1.0)		Identification number OSEP6-P6-10	Sheet 20/94
				Rev A	
				Date of issue 2026-10-04	

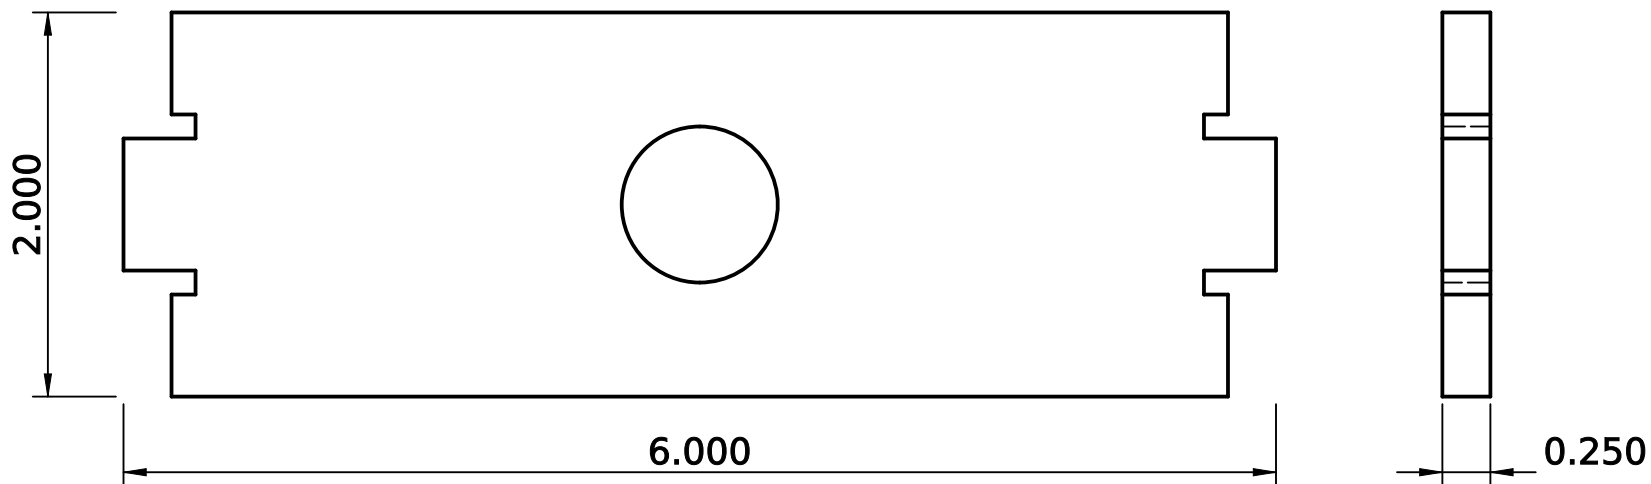

NOTES:

1. ALL DIMENSIONS IN INCHES. TOLERANCE $\pm 1/32$ UNLESS NOTED.
2. BREAK SHARP EDGES, REMOVE BURRS.
3. MATERIAL PER TITLE BLOCK. FILLET WELDS 1/4 UNLESS NOTED.
4. OSE 01-171-00-0, IN COMP SHORT SIDE ASSEMBLY. USED IN: MAIN FRAME 4.
5. L-Q2 NOT FOUND IN THE ORIGINAL DXF LIBRARIES.
6. GEOMETRY FROM OSE FULL_ASSEMBLY.STP (CEB PRESS 6); TITLE BLOCKS OF OSE'S 2D SET SAY 'CEB PRESS 5'.


Material 1/4" plate, 2 x 6		Qty 4	Scale 1:1	Units inch	Projection 
Created by J. Clements III		Approved by -	Document type Detail drawing		Status Draft
Legal owner J. Clements III CEB Project	Title Compression Short Side Plate L-Q2 OSE CEB Press 6 (a-z Build 1.0)			Identification number OSEP6-P6-11	Sheet 21/94
				Rev A Date of issue 2026-10-04	

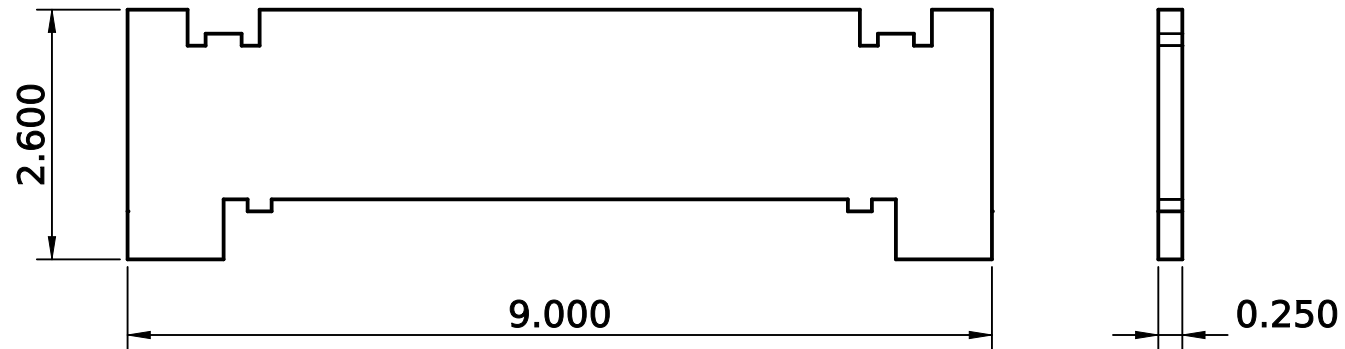

NOTES:

1. ALL DIMENSIONS IN INCHES. TOLERANCE $\pm 1/32$ UNLESS NOTED.
2. BREAK SHARP EDGES, REMOVE BURRS.
3. MATERIAL PER TITLE BLOCK. FILLET WELDS $1/4$ UNLESS NOTED.
4. OSE 01-172-00-0, IN COMP SHORT SIDE ASSEMBLY. USED IN: MAIN FRAME 4.
5. DXF LIBRARY L-Q1: 9 X 2.600 X $1/4$ - MATCHES THE MODEL.
6. GEOMETRY FROM OSE FULL_ASSEMBLY.STP (CEB PRESS 6); TITLE BLOCKS OF OSE'S 2D SET SAY 'CEB PRESS 5'.


Material 1/4" plate, 2.600 x 9		Qty 4	Scale 1:2	Units inch	Projection 
Created by J. Clements III		Approved by -		Document type Detail drawing	Status Draft
Legal owner J. Clements III CEB Project	Title Compression Short Side Plate L-Q1 OSE CEB Press 6 (a-z Build 1.0)			Identification number OSEP6-P6-12	Sheet 22/94
				Rev A Date of issue 2026-10-04	

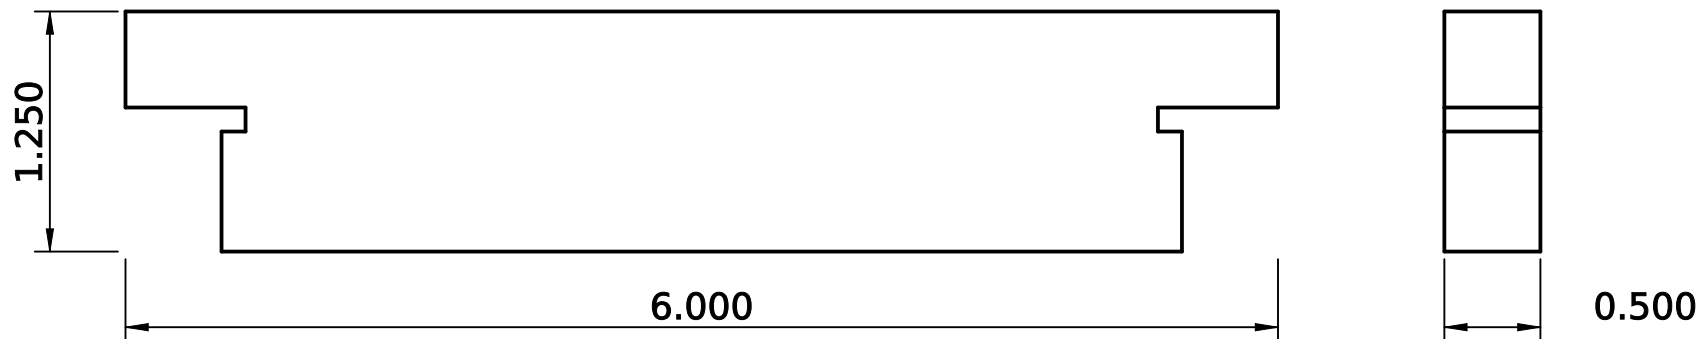

NOTES:

1. ALL DIMENSIONS IN INCHES. TOLERANCE $\pm 1/32$ UNLESS NOTED.
2. BREAK SHARP EDGES, REMOVE BURRS.
3. MATERIAL PER TITLE BLOCK. FILLET WELDS $1/4$ UNLESS NOTED.
4. OSE 01-271-00-0, IN FRAME CHANNEL ASSEMBLY. USED IN: MAIN FRAME 6.
5. DXF LIBRARY L-F13: 6 X 1-1/4 X 1/2 - MATCHES THE MODEL.
6. GEOMETRY FROM OSE FULL_ASSEMBLY.STP (CEB PRESS 6); TITLE BLOCKS OF OSE'S 2D SET SAY 'CEB PRESS 5'.

Material 1/2" plate, 1-1/4 x 6		Qty 6	Scale 1:1	Units inch	Projection 	
Created by J. Clements III		Approved by -		Document type Detail drawing	Status Draft	
Legal owner J. Clements III CEB Project	Title Frame Channel Plate L-F13 OSE CEB Press 6 (a-z Build 1.0)			Identification number OSEP6-P6-13		Sheet 23/94
				Rev A	Date of issue 2026-10-04	


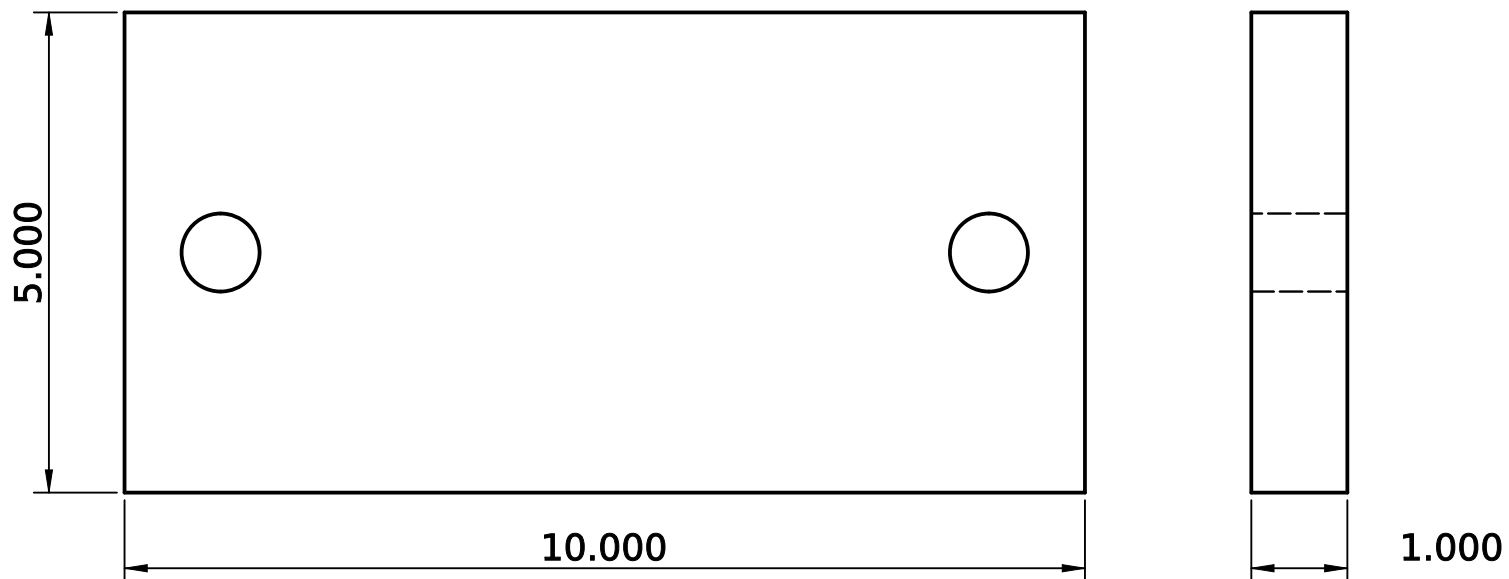


NOTES:

1. ALL DIMENSIONS IN INCHES. TOLERANCE $\pm 1/32$ UNLESS NOTED.
2. BREAK SHARP EDGES, REMOVE BURRS.
3. MATERIAL PER TITLE BLOCK. FILLET WELDS $1/4$ UNLESS NOTED.
4. OSE 01-035-00-0 / WELDMENT 001-0035, IN CYLINDER FOOT. USED IN: PRESS CYLINDER AND FOOT 1.
5. GEOMETRY FROM OSE FULL_ASSEMBLY.STP (CEB PRESS 6); TITLE BLOCKS OF OSE'S 2D SET SAY 'CEB PRESS 5'.

Material FLAT BAR, FB1X4		Qty 1	Scale 1:2	Units inch	Projection 
Created by J. Clements III		Approved by -		Document type Detail drawing	Status Draft
Legal owner J. Clements III CEB Project	Title Main Cylinder - Lower Press Foot OSE CEB Press 6 (a-z Build 1.0)			Identification number OSEP6-P6-14	Sheet 24/94
				Rev A	

1.000

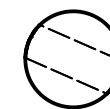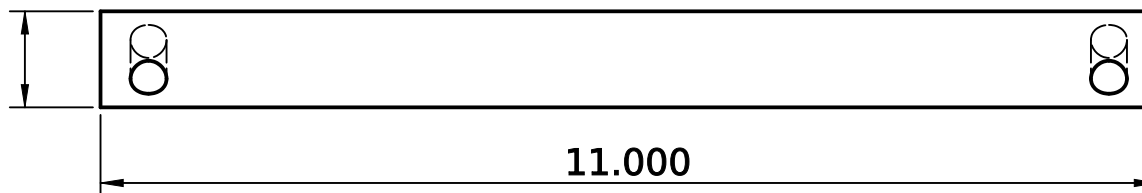


1.000



NOTES:

1. ALL DIMENSIONS IN INCHES. TOLERANCE $\pm 1/32$ UNLESS NOTED.
2. BREAK SHARP EDGES, REMOVE BURRS.
3. MATERIAL PER TITLE BLOCK. FILLET WELDS $1/4$ UNLESS NOTED.
4. OSE 01-103-00-0, IN MAIN FRAME ASSEMBLY. USED IN: PRESS CYLINDER AND FOOT
- 1.
5. GEOMETRY FROM OSE FULL_ASSEMBLY.STP (CEB PRESS 6); TITLE BLOCKS OF OSE'S 2D SET SAY 'CEB PRESS 5'.


Material 1-1/2 ROUND BAR X 11		Qty 1	Scale 1:2	Units inch	Projection 	
Created by J. Clements III		Approved by -		Document type Detail drawing	Status Draft	
Legal owner J. Clements III CEB Project	Title Main Frame - Cylinder Pin OSE CEB Press 6 (a-z Build 1.0)			Identification number OSEP6-P6-15		Sheet 25/94
				Rev A	Date of issue 2026-10-04	

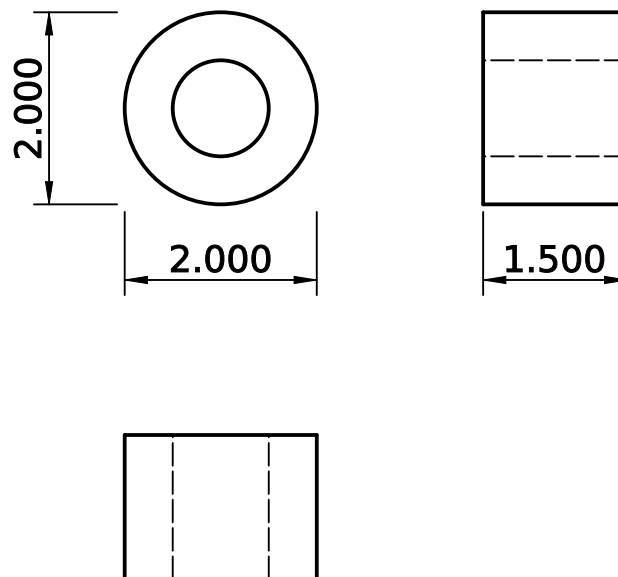

NOTES:

1. ALL DIMENSIONS IN INCHES. TOLERANCE $\pm 1/32$ UNLESS NOTED.
2. BREAK SHARP EDGES, REMOVE BURRS.
3. MATERIAL PER TITLE BLOCK. FILLET WELDS $1/4$ UNLESS NOTED.
4. OSE 01-109-00-0 / WELDMENT 001-0109, IN MAIN FRAME ASSEMBLY. USED IN: PRESS CYLINDER AND FOOT 2.
5. GEOMETRY FROM OSE FULL_ASSEMBLY.STP (CEB PRESS 6); TITLE BLOCKS OF OSE'S 2D SET SAY 'CEB PRESS 5'.


Material TUBE, DOM 2" OD X 1.5" ID	Qty 2	Scale 1:2	Units inch	Projection 
Created by J. Clements III	Approved by -	Document type Detail drawing	Status Draft	
Legal owner J. Clements III CEB Project	Title Main Frame - Horizontal Members, Cylinder OSE CEB Press 6 (a-z Build 1.0)	Identification number OSEP6-P6-16 Rev A	Date of issue 2026-10-04	Sheet 26/94

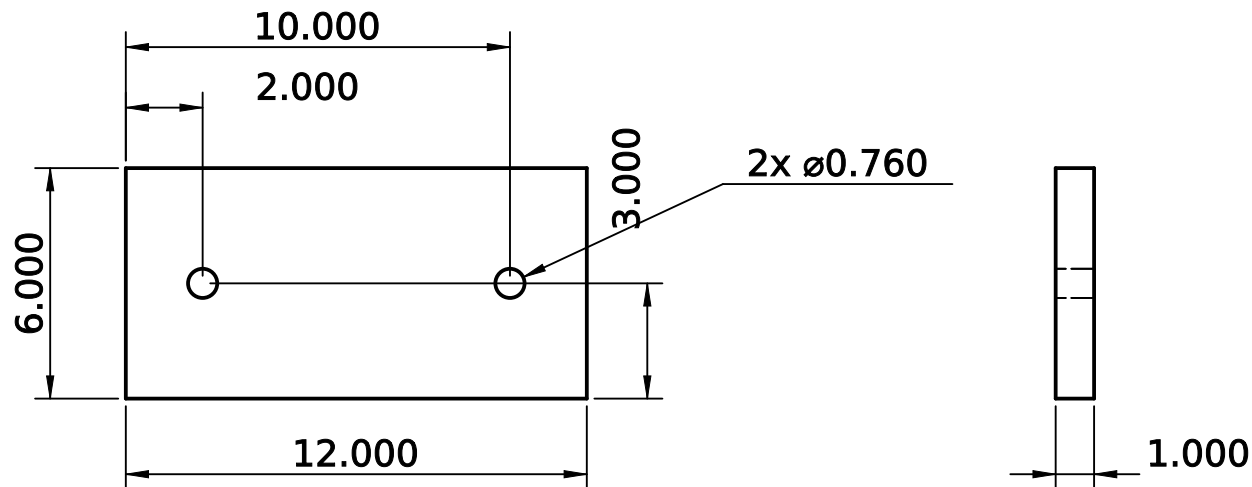

NOTES:

1. ALL DIMENSIONS IN INCHES. TOLERANCE $\pm 1/32$ UNLESS NOTED.
2. BREAK SHARP EDGES, REMOVE BURRS.
3. MATERIAL PER TITLE BLOCK. FILLET WELDS 1/4 UNLESS NOTED.
4. OSE 01-162-00-0, IN PRESS FOOT ASSEMBLY. USED IN: PRESS CYLINDER AND FOOT
- 1.
5. GEOMETRY FROM OSE FULL_ASSEMBLY.STP (CEB PRESS 6); TITLE BLOCKS OF OSE'S 2D SET SAY 'CEB PRESS 5'.


Material 1 X 6 X 12 PLATE		Qty 1	Scale 1:5	Units inch	Projection 	
Created by J. Clements III		Approved by -		Document type Detail drawing	Status Draft	
Legal owner J. Clements III CEB Project		Title Upper Press Foot (AR300) OSE CEB Press 6 (a-z Build 1.0)			Identification number OSEP6-P6-17	Sheet 27/94
			Rev A	Date of issue 2026-10-04		

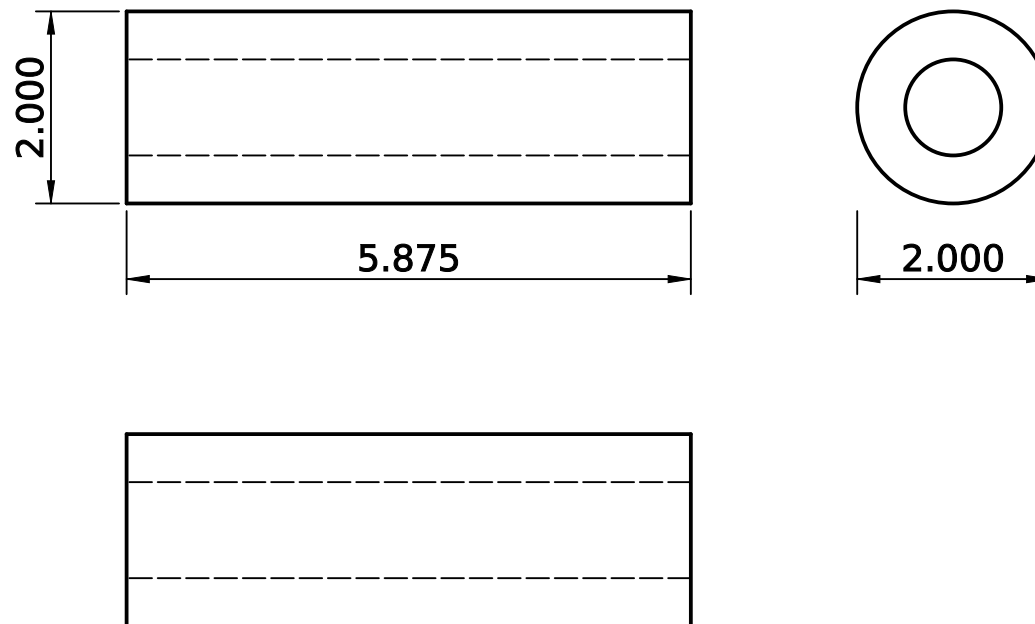

NOTES:

1. ALL DIMENSIONS IN INCHES. TOLERANCE $\pm 1/32$ UNLESS NOTED.
2. BREAK SHARP EDGES, REMOVE BURRS.
3. MATERIAL PER TITLE BLOCK. FILLET WELDS $1/4$ UNLESS NOTED.
4. OSE 01-189-00-0, IN PMC-21012. USED IN: PRESS CYLINDER AND FOOT 1.
5. GEOMETRY FROM OSE FULL_ASSEMBLY.STP (CEB PRESS 6); TITLE BLOCKS OF OSE'S 2D SET SAY 'CEB PRESS 5'.


Material 1/4 X 2-1/2 ROUND TUBE X 5-7/8		Qty 1	Scale 1:2	Units inch	Projection 	
Created by J. Clements III		Approved by -		Document type Detail drawing	Status Draft	
Legal owner J. Clements III CEB Project	Title 1/4 X 2-1/2 Round Tube X 5-7/8 OSE CEB Press 6 (a-z Build 1.0)			Identification number OSEP6-P6-18		Sheet 28/94
				Rev A	Date of issue 2026-10-04	

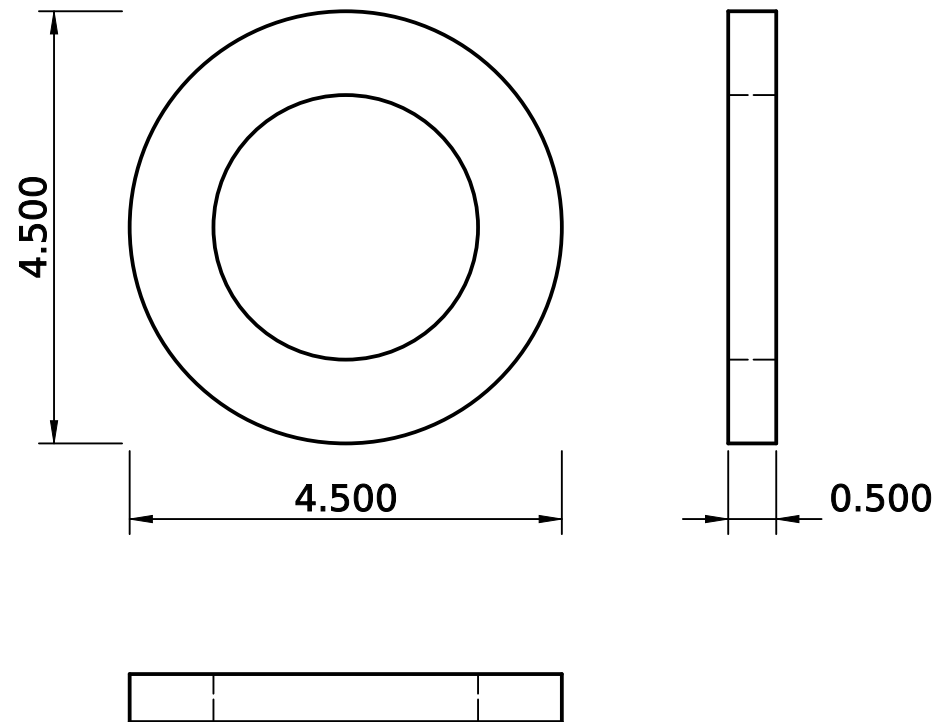

NOTES:

1. ALL DIMENSIONS IN INCHES. TOLERANCE $\pm 1/32$ UNLESS NOTED.
2. BREAK SHARP EDGES, REMOVE BURRS.
3. MATERIAL PER TITLE BLOCK. FILLET WELDS $1/4$ UNLESS NOTED.
4. OSE 01-281-00-0, IN CYLINDER FOOT. USED IN: PRESS CYLINDER AND FOOT 1.
5. DXF LIBRARY L-O11: 4-1/2 X 4-1/2 X 1/2 - MATCHES THE MODEL.
6. GEOMETRY FROM OSE FULL_ASSEMBLY.STP (CEB PRESS 6); TITLE BLOCKS OF OSE'S 2D SET SAY 'CEB PRESS 5'.


Material 4-1/2 x 4-1/2 x 1/2 (see model)		Qty 1	Scale 1:2	Units inch	Projection 
Created by J. Clements III		Approved by -	Document type Detail drawing		Status Draft
Legal owner J. Clements III CEB Project		Title Cylinder Foot Plate L-O11 OSE CEB Press 6 (a-z Build 1.0)		Identification number OSEP6-P6-19	Sheet 29/94
				Rev A Date of issue 2026-10-04	

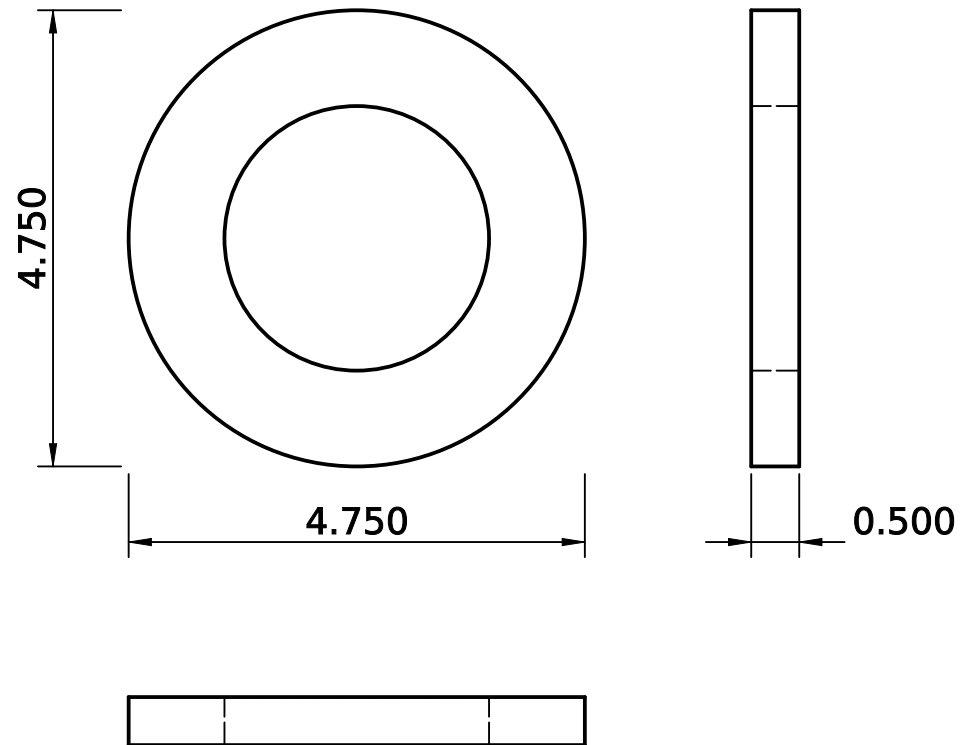

NOTES:

1. ALL DIMENSIONS IN INCHES. TOLERANCE $\pm 1/32$ UNLESS NOTED.
2. BREAK SHARP EDGES, REMOVE BURRS.
3. MATERIAL PER TITLE BLOCK. FILLET WELDS $1/4$ UNLESS NOTED.
4. OSE 01-282-00-0, IN CYLINDER FOOT. USED IN: PRESS CYLINDER AND FOOT 1.
5. DXF LIBRARY L-O12: 4-3/4 X 4-3/4 X 1/2 - MATCHES THE MODEL.
6. GEOMETRY FROM OSE FULL_ASSEMBLY.STP (CEB PRESS 6); TITLE BLOCKS OF OSE'S 2D SET SAY 'CEB PRESS 5'.

Material 4-3/4 x 4-3/4 x 1/2 (see model)		Qty 1	Scale 1:2	Units inch	Projection 
Created by J. Clements III		Approved by -	Document type Detail drawing		Status Draft
Legal owner J. Clements III CEB Project		Title Cylinder Foot Plate L-O12 OSE CEB Press 6 (a-z Build 1.0)		Identification number OSEP6-P6-20	Sheet 30/94
				Rev A Date of issue 2026-10-04	

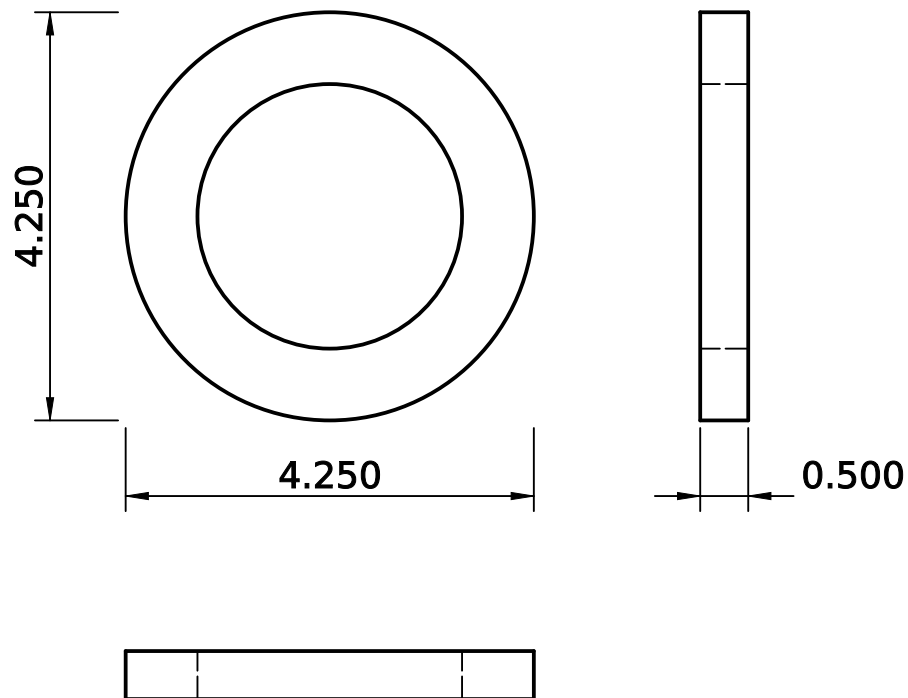


NOTES:

1. ALL DIMENSIONS IN INCHES. TOLERANCE $\pm 1/32$ UNLESS NOTED.
2. BREAK SHARP EDGES, REMOVE BURRS.
3. MATERIAL PER TITLE BLOCK. FILLET WELDS $1/4$ UNLESS NOTED.
4. OSE 01-283-00-0, IN CYLINDER FOOT. USED IN: PRESS CYLINDER AND FOOT 1.
5. DXF LIBRARY L-O13: 4-1/4 X 4-1/4 X 1/2 - MATCHES THE MODEL.
6. GEOMETRY FROM OSE FULL_ASSEMBLY.STP (CEB PRESS 6); TITLE BLOCKS OF OSE'S 2D SET SAY 'CEB PRESS 5'.

Material 4-1/4 x 4-1/4 x 1/2 (see model)		Qty 1	Scale 1:2	Units inch	Projection 	
Created by J. Clements III		Approved by -	Document type Detail drawing		Status Draft	
Legal owner J. Clements III CEB Project	Title Cylinder Foot Plate L-O13 OSE CEB Press 6 (a-z Build 1.0)			Identification number OSEP6-P6-21		Sheet 31/94
				Rev A	Date of issue 2026-10-04	

4.000

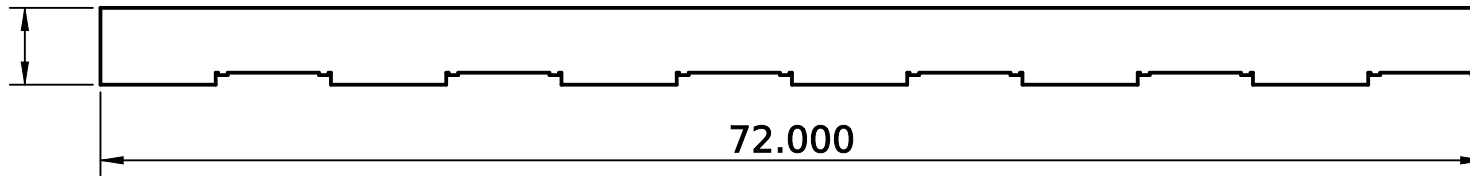

72.000



0.500

NOTES:

1. ALL DIMENSIONS IN INCHES. TOLERANCE $\pm 1/32$ UNLESS NOTED.
2. BREAK SHARP EDGES, REMOVE BURRS.
3. MATERIAL PER TITLE BLOCK. FILLET WELDS $1/4$ UNLESS NOTED.
4. OSE 01-004-00-0 / WELDMENT 001-0004, IN REAR SECONDARY ARM ASSEMBLY, REAR SECONDARY ARM ASSEMBLY. USED IN: ARMS 2.
5. DXF LIBRARY L-A3: 72 X 4 X $1/2$ - MATCHES THE MODEL.
6. OSE 2015 WELDMENT REDRAW MAKES IT FROM ANGLE, STEEL, L6X4X $1/2$ INSTEAD.
7. GEOMETRY FROM OSE FULL_ASSEMBLY.STP (CEB PRESS 6); TITLE BLOCKS OF OSE'S 2D SET SAY 'CEB PRESS 5'.

Material 1/2" plate, 4 x 72		Qty 2	Scale 1:10	Units inch	Projection 	
Created by J. Clements III		Approved by -		Document type Detail drawing	Status Draft	
Legal owner J. Clements III CEB Project	Title Secondary Arm L-A3 OSE CEB Press 6 (a-z Build 1.0)			Identification number OSEP6-P6-22		Sheet 32/94
				Rev A	Date of issue 2026-10-04	


5.966

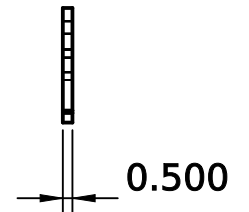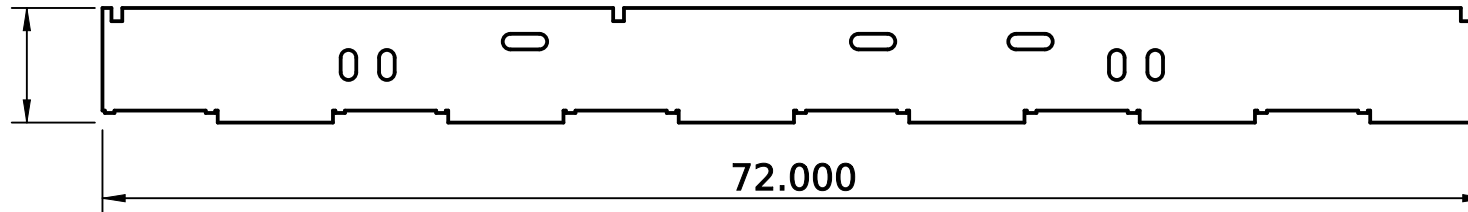

NOTES:

1. ALL DIMENSIONS IN INCHES. TOLERANCE $\pm 1/32$ UNLESS NOTED.
2. BREAK SHARP EDGES, REMOVE BURRS.
3. MATERIAL PER TITLE BLOCK. FILLET WELDS $1/4$ UNLESS NOTED.
4. OSE 01-009-00-1 / WELDMENT 001-0009, IN PRIMARY ARM LEFT HAND ASSEMBLY, PRIMARY ARM RIGHT HAND ASSEMBLY. USED IN: ARMS 2.
5. DXF LIBRARY L-A2: 72 X 5.966 X $1/2$ - MATCHES THE MODEL.
6. OSE 2015 WELDMENT REDRAW MAKES IT FROM ANGLE, STEEL, L6X4X $1/2$ INSTEAD.
7. GEOMETRY FROM OSE FULL_ASSEMBLY.STP (CEB PRESS 6); TITLE BLOCKS OF OSE'S 2D SET SAY 'CEB PRESS 5'.


Material 1/2" plate, 5.966 x 72		Qty 2	Scale 1:10	Units inch	Projection 	
Created by J. Clements III		Approved by -		Document type Detail drawing	Status Draft	
Legal owner J. Clements III CEB Project	Title Primary Arm L-A2 OSE CEB Press 6 (a-z Build 1.0)			Identification number OSEP6-P6-23		Sheet 33/94
				Rev A	Date of issue 2026-10-04	

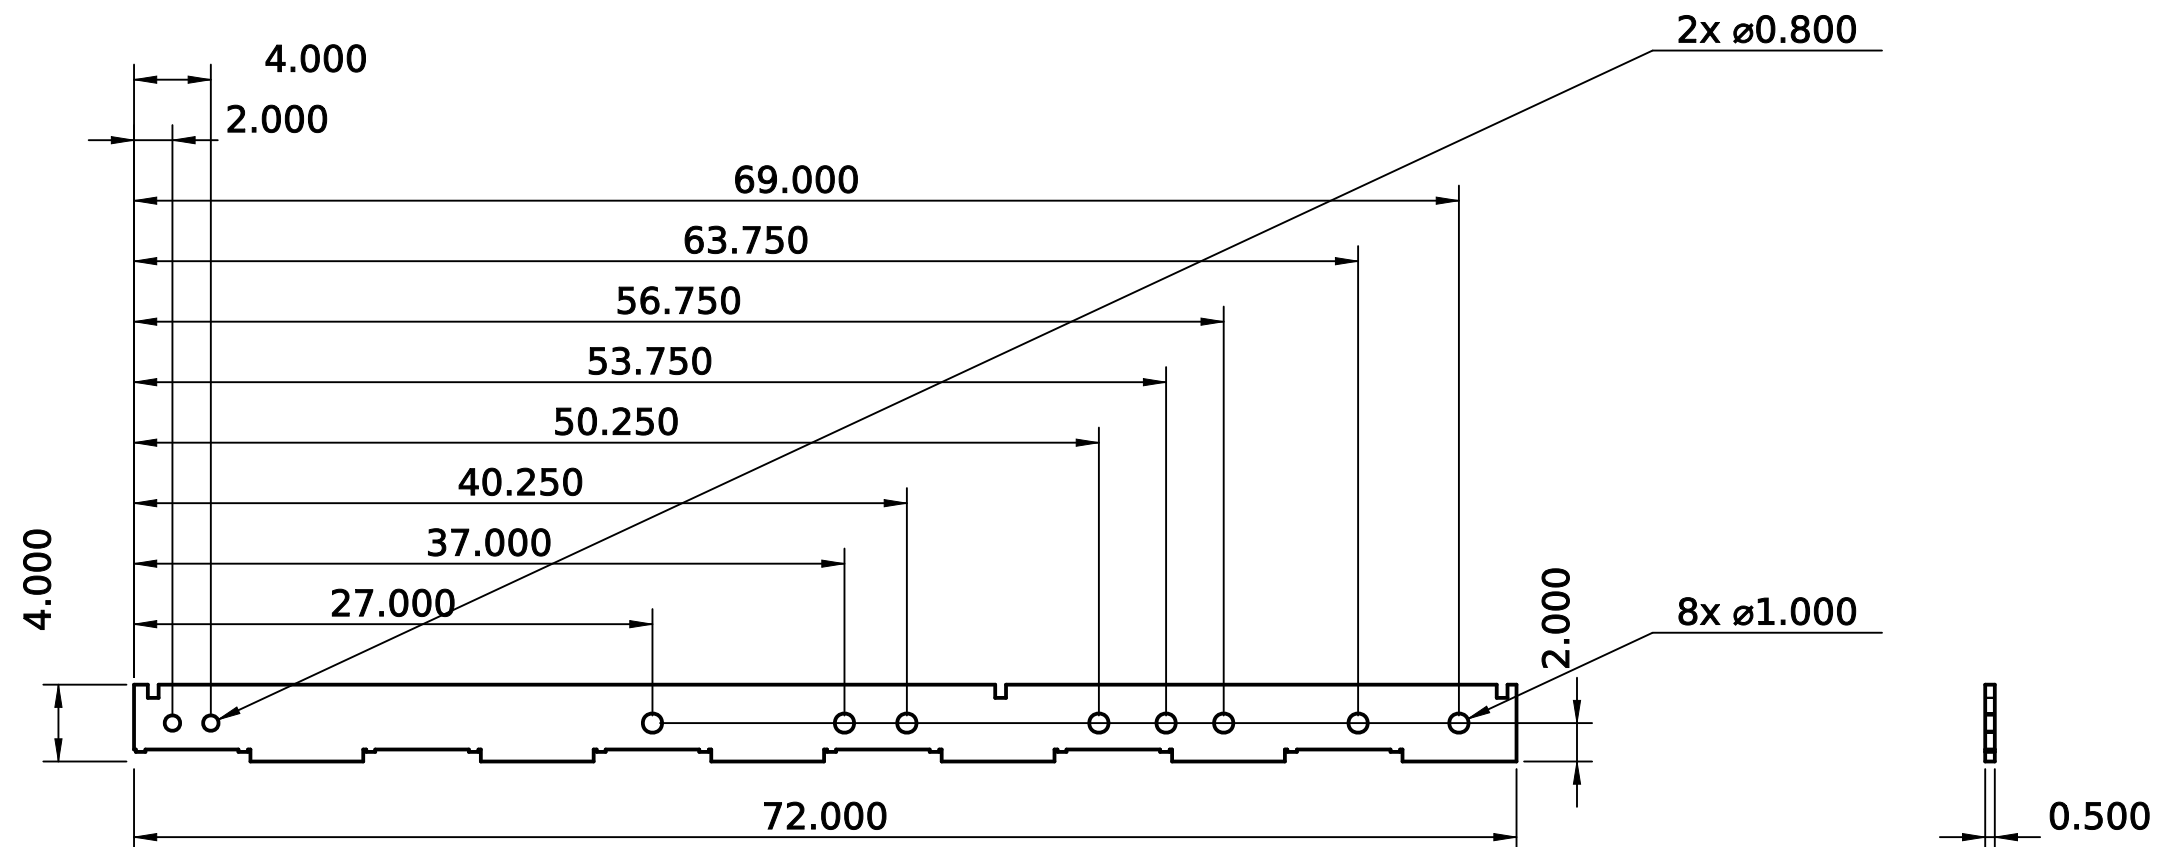

NOTES:

1. ALL DIMENSIONS IN INCHES. TOLERANCE $\pm 1/32$ UNLESS NOTED.
2. BREAK SHARP EDGES, REMOVE BURRS.
3. MATERIAL PER TITLE BLOCK. FILLET WELDS $1/4$ UNLESS NOTED.
4. OSE 01-010-00-0 / WELDMENT 001-0010, IN PRIMARY ARM LEFT HAND ASSEMBLY, PRIMARY ARM RIGHT HAND ASSEMBLY. USED IN: ARMS 2.
5. DXF LIBRARY L-A1: 72 X 4 X $1/2$ - MATCHES THE MODEL.
6. OSE 2015 WELDMENT REDRAW MAKES IT FROM ANGLE, STEEL, L6X4X $1/2$ INSTEAD.
7. GEOMETRY FROM OSE FULL_ASSEMBLY.STP (CEB PRESS 6); TITLE BLOCKS OF OSE'S 2D SET SAY 'CEB PRESS 5'.

Material 1/2" plate, 4 x 72		Qty 2	Scale 1:10	Units inch	Projection 
Created by J. Clements III		Approved by -		Document type Detail drawing	
Legal owner J. Clements III CEB Project		Title Primary Arm L-A1 OSE CEB Press 6 (a-z Build 1.0)			Identification number OSEP6-P6-24
					Rev A
					Date of issue 2026-10-04
					Sheet 34/94

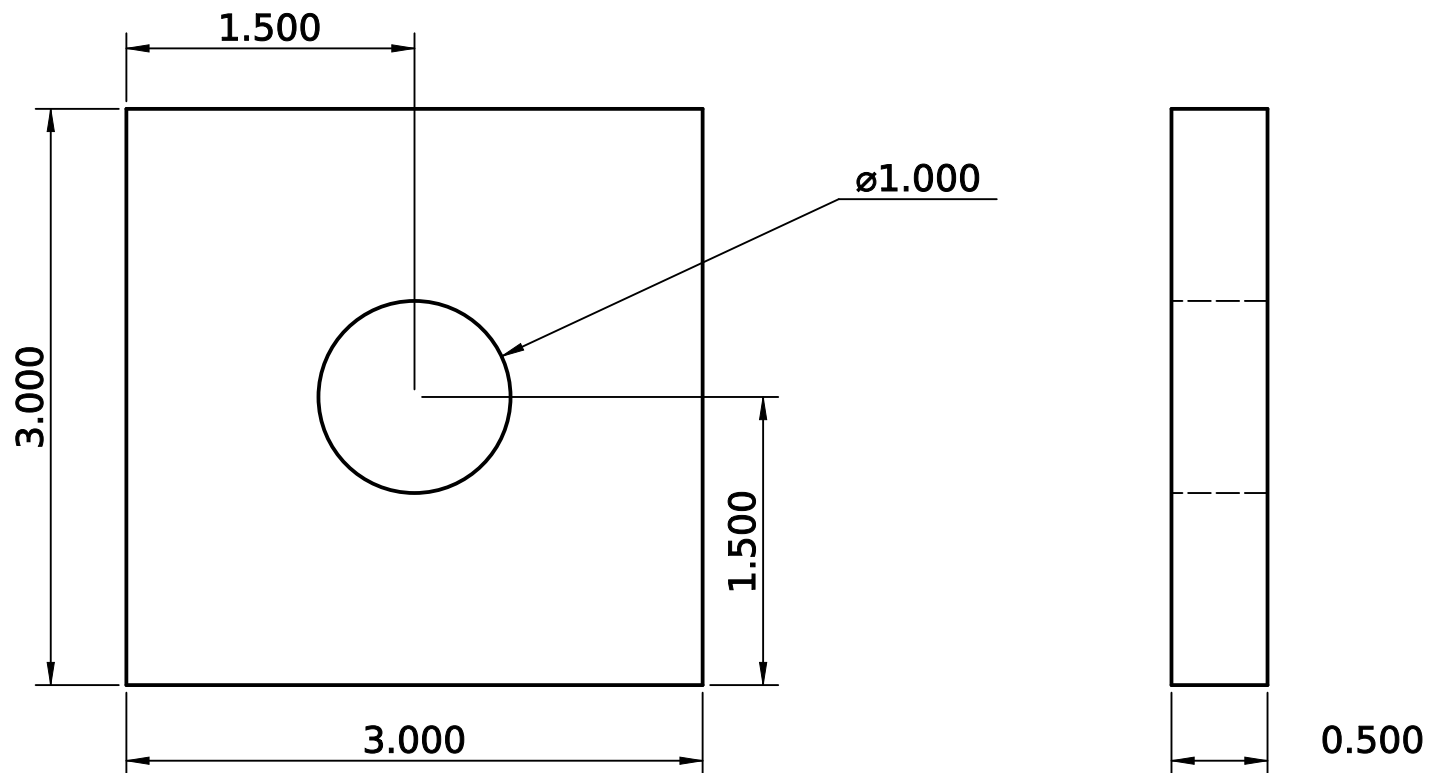


NOTES:

1. ALL DIMENSIONS IN INCHES. TOLERANCE $\pm 1/32$ UNLESS NOTED.
2. BREAK SHARP EDGES, REMOVE BURRS.
3. MATERIAL PER TITLE BLOCK. FILLET WELDS $1/4$ UNLESS NOTED.
4. OSE 01-028-00-0 / WELDMENT 001-0028, IN REAR SECONDARY ARM ASSEMBLY. USED IN: ARMS 2.
5. DXF LIBRARY L-D7: 3 X 3 X $1/2$ - MATCHES THE MODEL.
6. GEOMETRY FROM OSE FULL_ASSEMBLY.STP (CEB PRESS 6); TITLE BLOCKS OF OSE'S 2D SET SAY 'CEB PRESS 5'.

Material 1/2" plate, 3 x 3		Qty 2	Scale 1:1	Units inch	Projection 	
Created by J. Clements III		Approved by -	Document type Detail drawing		Status Draft	
Legal owner J. Clements III CEB Project	Title Secondary Arms - Eye for 2nd Cylinder OSE CEB Press 6 (a-z Build 1.0)			Identification number OSEP6-P6-25		Sheet 35/94
				Rev A	Date of issue 2026-10-04	

6.000

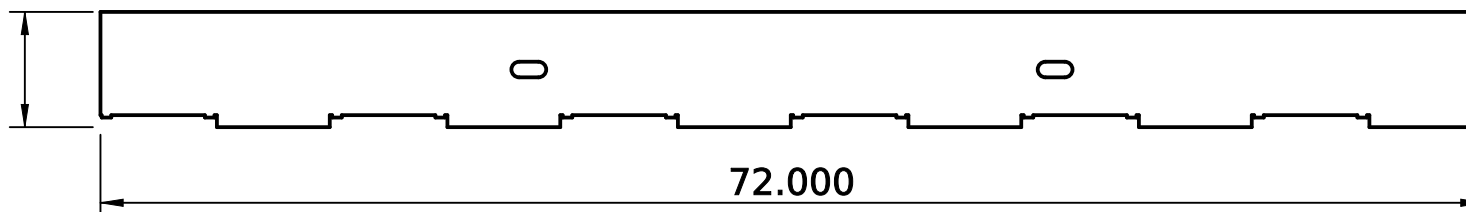


0.500

NOTES:

1. ALL DIMENSIONS IN INCHES. TOLERANCE $\pm 1/32$ UNLESS NOTED.
2. BREAK SHARP EDGES, REMOVE BURRS.
3. MATERIAL PER TITLE BLOCK. FILLET WELDS $1/4$ UNLESS NOTED.
4. OSE 01-138-00-0, IN REAR SECONDARY ARM ASSEMBLY. USED IN: ARMS 1.
5. DXF LIBRARY L-A5: 72 X 6 X $1/2$ - MATCHES THE MODEL.
6. GEOMETRY FROM OSE FULL_ASSEMBLY.STP (CEB PRESS 6); TITLE BLOCKS OF OSE'S 2D SET SAY 'CEB PRESS 5'.

Material 1/2" plate, 6 x 72		Qty 1	Scale 1:10	Units inch	Projection 	
Created by J. Clements III		Approved by -		Document type Detail drawing	Status Draft	
Legal owner J. Clements III CEB Project	Title Rear Secondary Arm Plate L-A5 OSE CEB Press 6 (a-z Build 1.0)			Identification number OSEP6-P6-26		Sheet 36/94
				Rev A	Date of issue 2026-10-04	


6.125

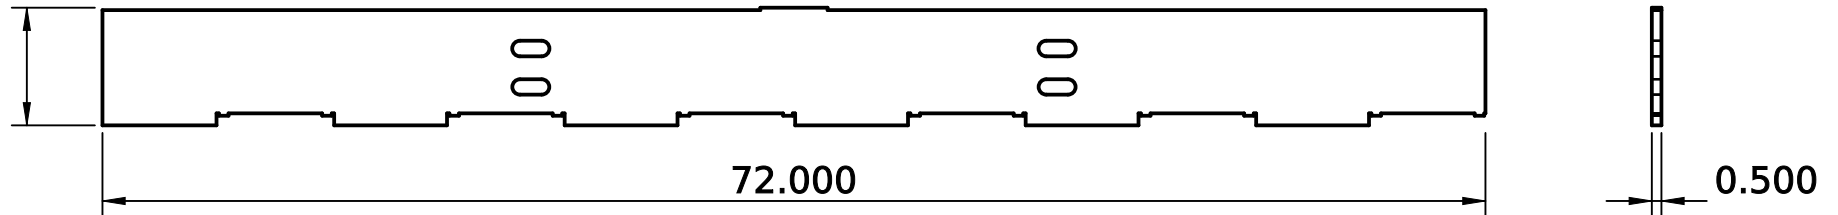

NOTES:

1. ALL DIMENSIONS IN INCHES. TOLERANCE $\pm 1/32$ UNLESS NOTED.
2. BREAK SHARP EDGES, REMOVE BURRS.
3. MATERIAL PER TITLE BLOCK. FILLET WELDS $1/4$ UNLESS NOTED.
4. OSE 01-139-00-0, IN REAR SECONDARY ARM ASSEMBLY. USED IN: ARMS 1.
5. DXF LIBRARY L-A4: 72 X 6-1/8 X 1/2 - MATCHES THE MODEL.
6. GEOMETRY FROM OSE FULL_ASSEMBLY.STP (CEB PRESS 6); TITLE BLOCKS OF OSE'S 2D SET SAY 'CEB PRESS 5'.


Material 1/2" plate, 6-1/8 x 72		Qty 1	Scale 1:10	Units inch	Projection 	
Created by J. Clements III		Approved by -		Document type Detail drawing	Status Draft	
Legal owner J. Clements III CEB Project	Title Rear Secondary Arm Plate L-A4 OSE CEB Press 6 (a-z Build 1.0)			Identification number OSEP6-P6-27		Sheet 37/94
				Rev A	Date of issue 2026-10-04	

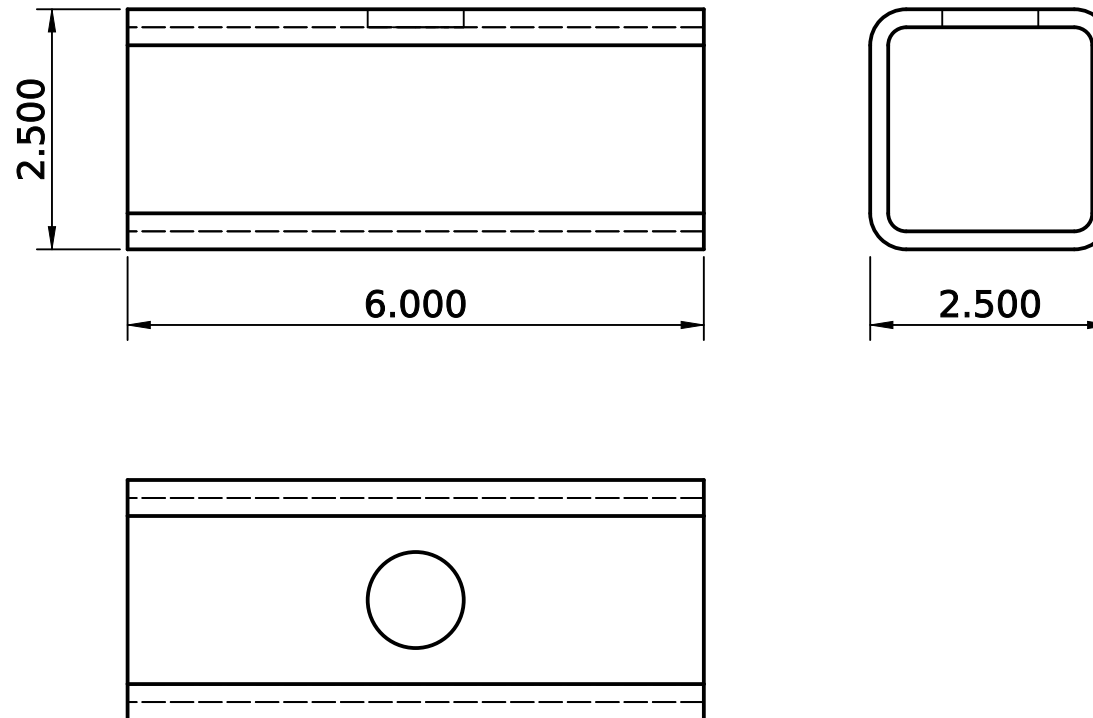

NOTES:

1. ALL DIMENSIONS IN INCHES. TOLERANCE $\pm 1/32$ UNLESS NOTED.
2. BREAK SHARP EDGES, REMOVE BURRS.
3. MATERIAL PER TITLE BLOCK. FILLET WELDS $1/4$ UNLESS NOTED.
4. OSE 01-182-00-0, IN CLAMP TUBE ASSEMBLY. USED IN: FEET AND LEGS 8, ARMS 8, GRATE 4.
5. GEOMETRY FROM OSE FULL_ASSEMBLY.STP (CEB PRESS 6); TITLE BLOCKS OF OSE'S 2D SET SAY 'CEB PRESS 5'.


Material 3/16 X 2-1/2 SQUARE TUBE X 6		Qty 20	Scale 1:2	Units inch	Projection 
Created by J. Clements III		Approved by -	Document type Detail drawing		Status Draft
Legal owner J. Clements III CEB Project		Title Leg Holder Tube OSE CEB Press 6 (a-z Build 1.0)		Identification number OSEP6-P6-28	Sheet 38/94
				Rev A Date of issue 2026-10-04	

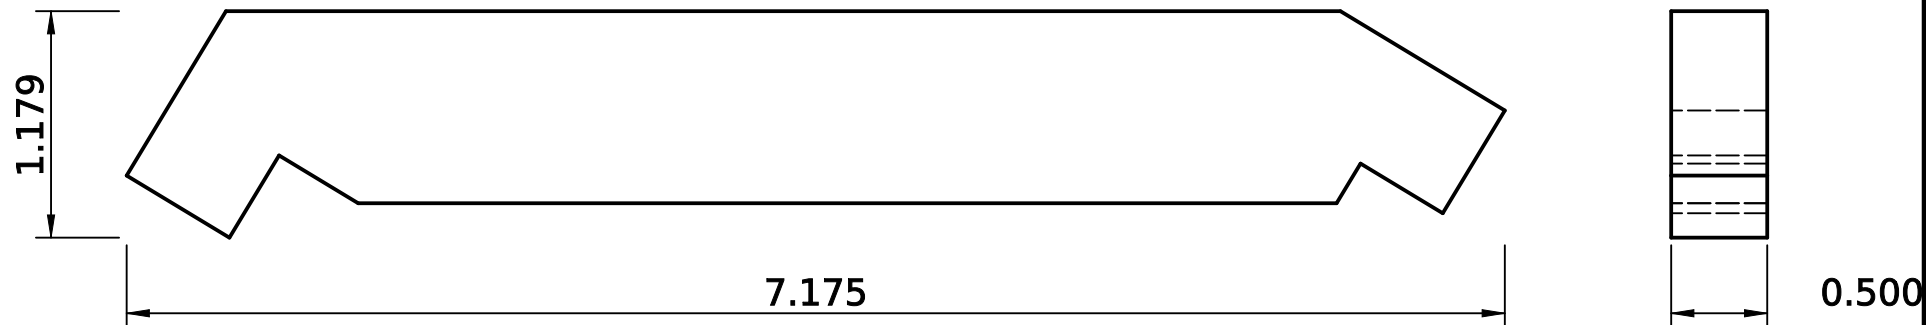

NOTES:

1. ALL DIMENSIONS IN INCHES. TOLERANCE $\pm 1/32$ UNLESS NOTED.
2. BREAK SHARP EDGES, REMOVE BURRS.
3. MATERIAL PER TITLE BLOCK. FILLET WELDS $1/4$ UNLESS NOTED.
4. OSE 01-272-00-0, IN PRIMARY ARM LEFT HAND ASSEMBLY, PRIMARY ARM RIGHT HAND ASSEMBLY. USED IN: ARMS 6.
5. DXF LIBRARY L-A6: 20.946 X 7.454 X $1/2$ - MODEL 7.175 X 1.179 X $1/2$; CHECK.
6. GEOMETRY FROM OSE FULL_ASSEMBLY.STP (CEB PRESS 6); TITLE BLOCKS OF OSE'S 2D SET SAY 'CEB PRESS 5'.

Material 1/2" plate, 1.179 x 7.175		Qty 6	Scale 1:1	Units inch	Projection 
Created by J. Clements III		Approved by -		Document type Detail drawing	Status Draft
Legal owner J. Clements III CEB Project	Title Primary Arm Plate L-A6 OSE CEB Press 6 (a-z Build 1.0)	Identification number OSEP6-P6-29		Sheet 39/94	
		Rev A	Date of issue 2026-10-04		

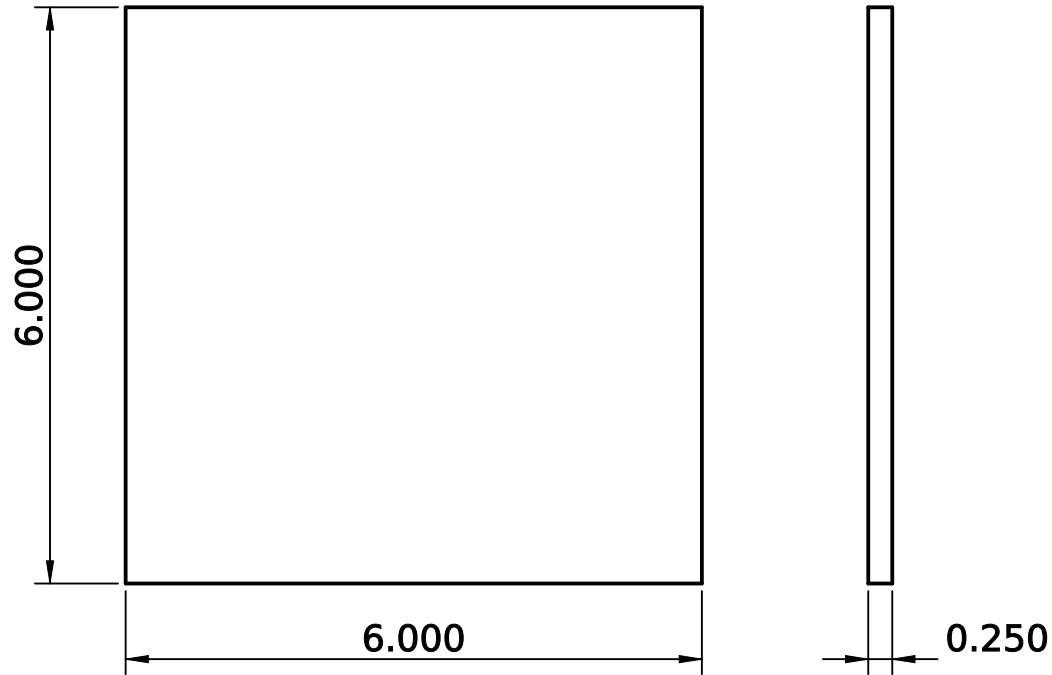


NOTES:

1. ALL DIMENSIONS IN INCHES. TOLERANCE $\pm 1/32$ UNLESS NOTED.
2. BREAK SHARP EDGES, REMOVE BURRS.
3. MATERIAL PER TITLE BLOCK. FILLET WELDS $1/4$ UNLESS NOTED.
4. OSE 01-006-00-0 / WELDMENT 001-0006, IN FOOT ASSEMBLY. USED IN: FEET AND LEGS 4.
5. DXF LIBRARY L-Q17: 6 X 6 X $1/4$ - MATCHES THE MODEL.
6. GEOMETRY FROM OSE FULL_ASSEMBLY.STP (CEB PRESS 6); TITLE BLOCKS OF OSE'S 2D SET SAY 'CEB PRESS 5'.

Material 1/4" plate, 6 x 6		Qty 4	Scale 1:2	Units inch	Projection 	
Created by J. Clements III		Approved by -		Document type Detail drawing	Status Draft	
Legal owner J. Clements III CEB Project	Title Foot Plate L-Q17 OSE CEB Press 6 (a-z Build 1.0)			Identification number OSEP6-P6-30		Sheet 40/94
				Rev A	Date of issue 2026-10-04	

2.000

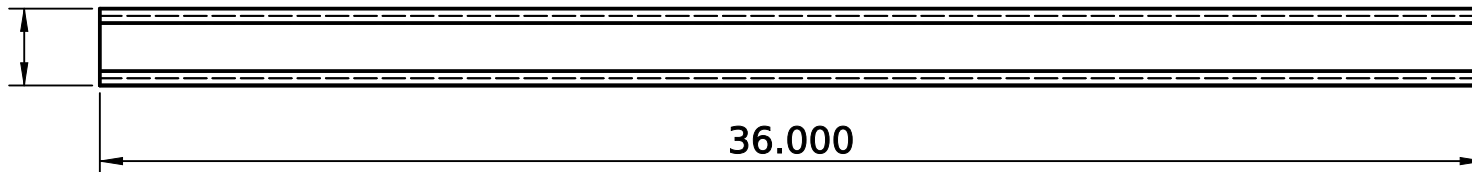


2.000



NOTES:

1. ALL DIMENSIONS IN INCHES. TOLERANCE $\pm 1/32$ UNLESS NOTED.
2. BREAK SHARP EDGES, REMOVE BURRS.
3. MATERIAL PER TITLE BLOCK. FILLET WELDS $1/4$ UNLESS NOTED.
4. OSE 01-155-00-0. USED IN: FEET AND LEGS 4.
5. GEOMETRY FROM OSE FULL_ASSEMBLY.STP (CEB PRESS 6); TITLE BLOCKS OF OSE'S 2D SET SAY 'CEB PRESS 5'.


Material 3/16 X 2 SQUARE TUBE X 36		Qty 4	Scale 1:5	Units inch	Projection 	
Created by J. Clements III		Approved by -		Document type Detail drawing	Status Draft	
Legal owner J. Clements III CEB Project	Title Leg OSE CEB Press 6 (a-z Build 1.0)			Identification number OSEP6-P6-31		Sheet 41/94
				Rev A	Date of issue 2026-10-04	

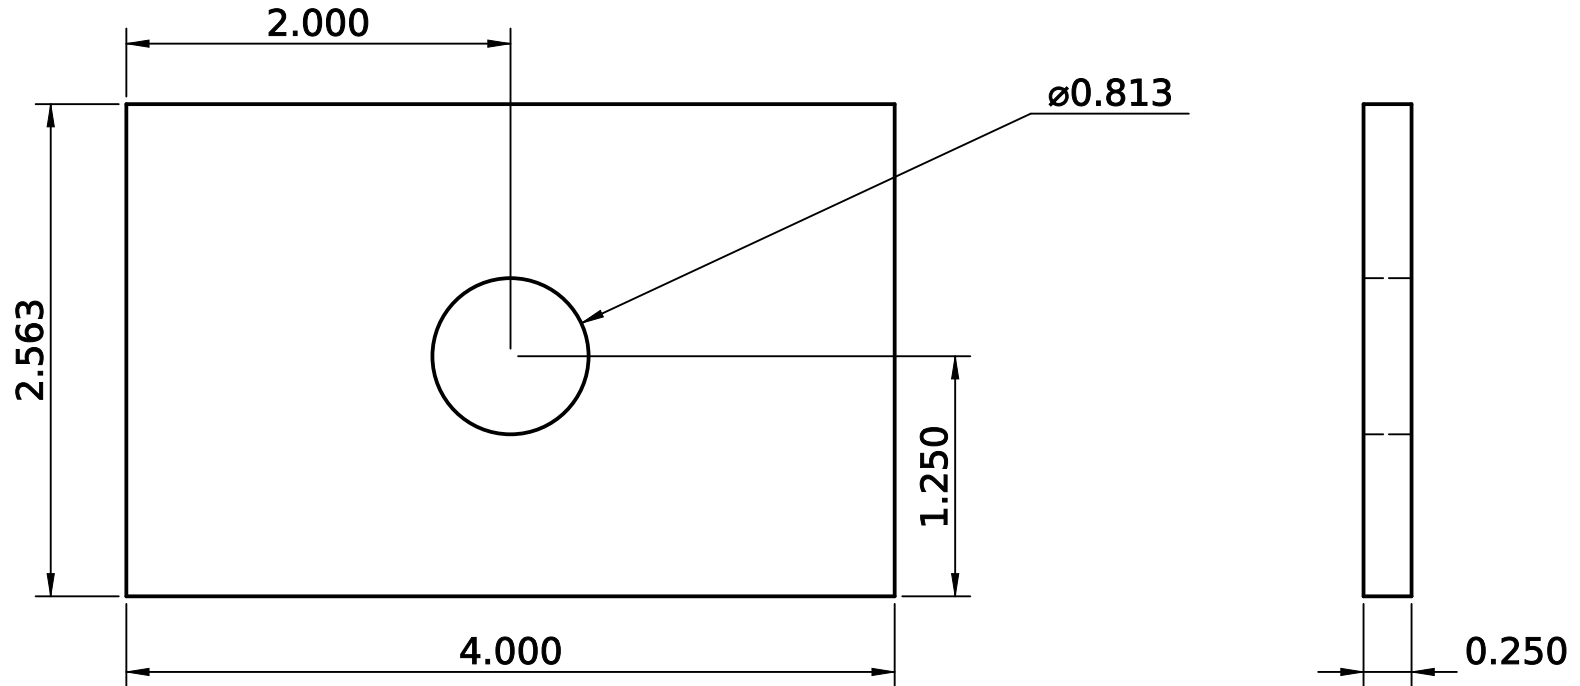

NOTES:

1. ALL DIMENSIONS IN INCHES. TOLERANCE $\pm 1/32$ UNLESS NOTED.
2. BREAK SHARP EDGES, REMOVE BURRS.
3. MATERIAL PER TITLE BLOCK. FILLET WELDS 1/4 UNLESS NOTED.
4. OSE 01-247-00-0, IN SUPPORT HOLDER WELDMENT. USED IN: FEET AND LEGS 8.
5. GEOMETRY FROM OSE FULL_ASSEMBLY.STP (CEB PRESS 6); TITLE BLOCKS OF OSE'S 2D SET SAY 'CEB PRESS 5'.


Material 1/4" plate, 2-9/16 x 4		Qty 8	Scale 1:1	Units inch	Projection 
Created by J. Clements III		Approved by -		Document type Detail drawing	Status Draft
Legal owner J. Clements III CEB Project	Title Support Holder Part 01-247 OSE CEB Press 6 (a-z Build 1.0)	Identification number OSEP6-P6-32		Sheet 42/94	
		Rev A	Date of issue 2026-10-04		

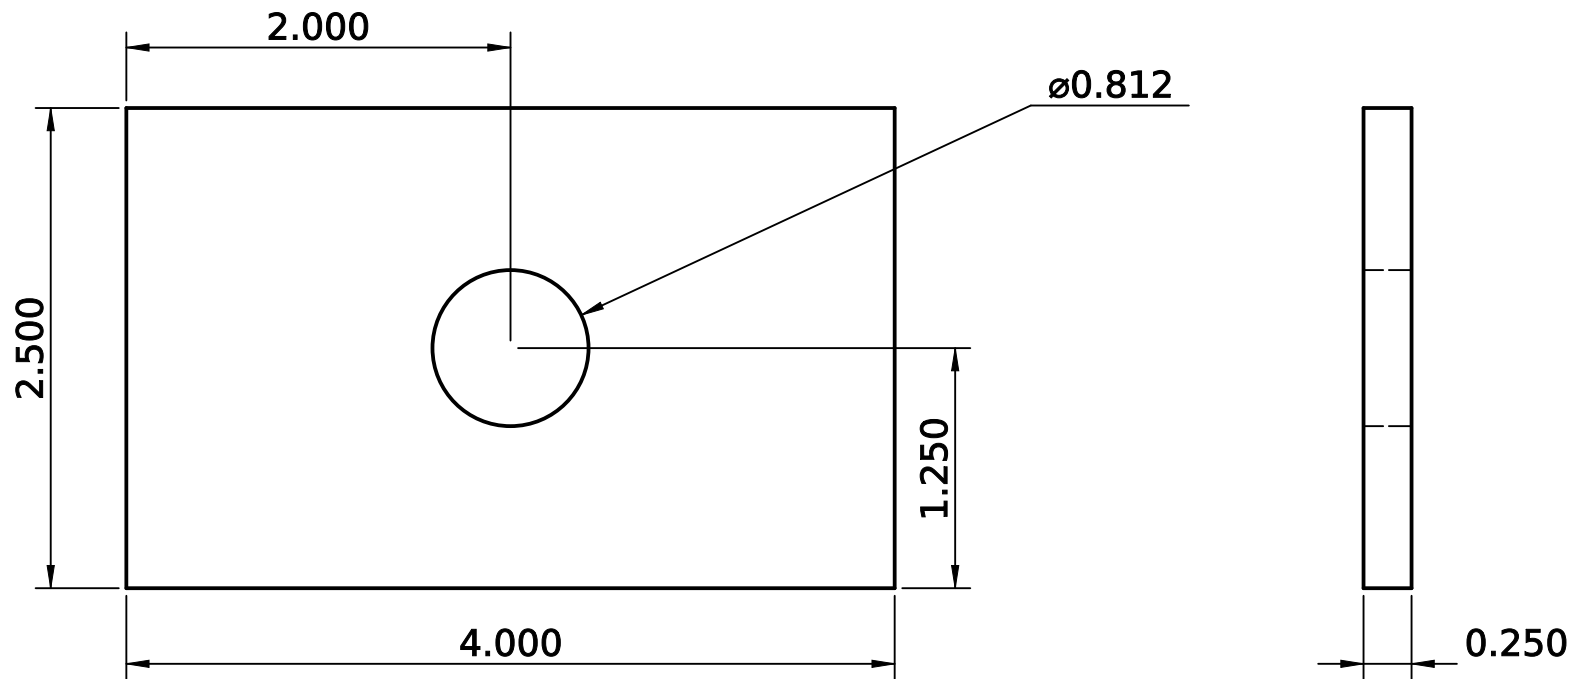

NOTES:

1. ALL DIMENSIONS IN INCHES. TOLERANCE $\pm 1/32$ UNLESS NOTED.
2. BREAK SHARP EDGES, REMOVE BURRS.
3. MATERIAL PER TITLE BLOCK. FILLET WELDS 1/4 UNLESS NOTED.
4. OSE 01-268-00-0, IN SUPPORT HOLDER WELDMENT. USED IN: FEET AND LEGS 8.
5. DXF LIBRARY L-Q9: 4 X 2-1/2 X 1/4 - MATCHES THE MODEL.
6. GEOMETRY FROM OSE FULL_ASSEMBLY.STP (CEB PRESS 6); TITLE BLOCKS OF OSE'S 2D SET SAY 'CEB PRESS 5'.


Material 1/4" plate, 2-1/2 x 4		Qty 8	Scale 1:1	Units inch	Projection 	
Created by J. Clements III		Approved by -	Document type Detail drawing		Status Draft	
Legal owner J. Clements III CEB Project	Title Support Holder Plate L-Q9 OSE CEB Press 6 (a-z Build 1.0)			Identification number OSEP6-P6-33		Sheet 43/94
				Rev A	Date of issue 2026-10-04	

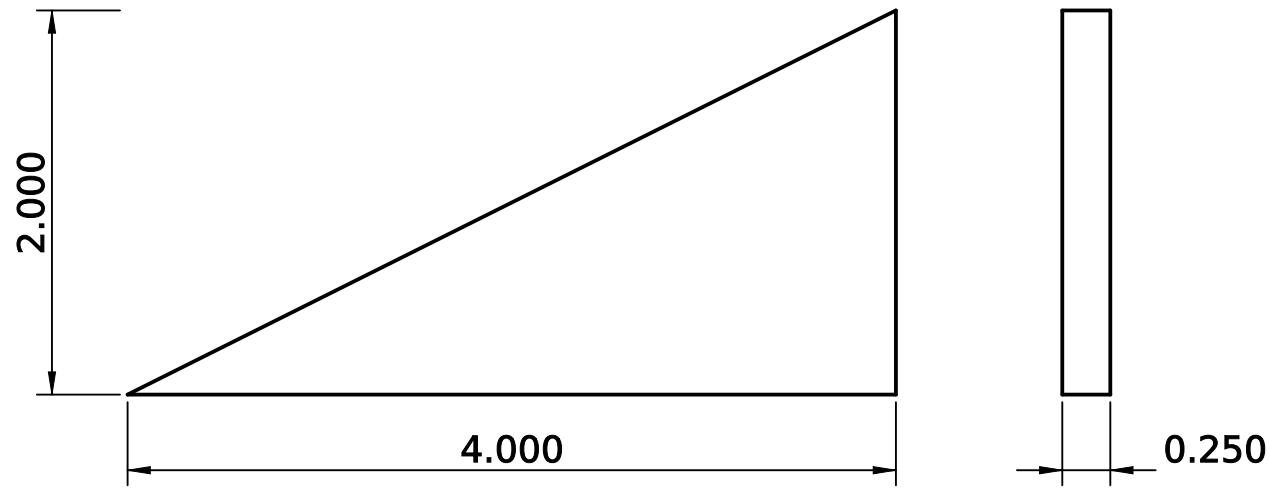

NOTES:

1. ALL DIMENSIONS IN INCHES. TOLERANCE $\pm 1/32$ UNLESS NOTED.
2. BREAK SHARP EDGES, REMOVE BURRS.
3. MATERIAL PER TITLE BLOCK. FILLET WELDS $1/4$ UNLESS NOTED.
4. OSE 01-269-00-0, IN SUPPORT HOLDER WELDMENT. USED IN: FEET AND LEGS 8.
5. DXF LIBRARY L-Q15: 4 X 2 X $1/4$ - MATCHES THE MODEL.
6. GEOMETRY FROM OSE FULL_ASSEMBLY.STP (CEB PRESS 6); TITLE BLOCKS OF OSE'S 2D SET SAY 'CEB PRESS 5'.


Material 1/4" plate, 2 x 4		Qty 8	Scale 1:1	Units inch	Projection 	
Created by J. Clements III		Approved by -		Document type Detail drawing	Status Draft	
Legal owner J. Clements III CEB Project	Title Support Holder Plate L-Q15 OSE CEB Press 6 (a-z Build 1.0)			Identification number OSEP6-P6-34		Sheet 44/94
				Rev A	Date of issue 2026-10-04	

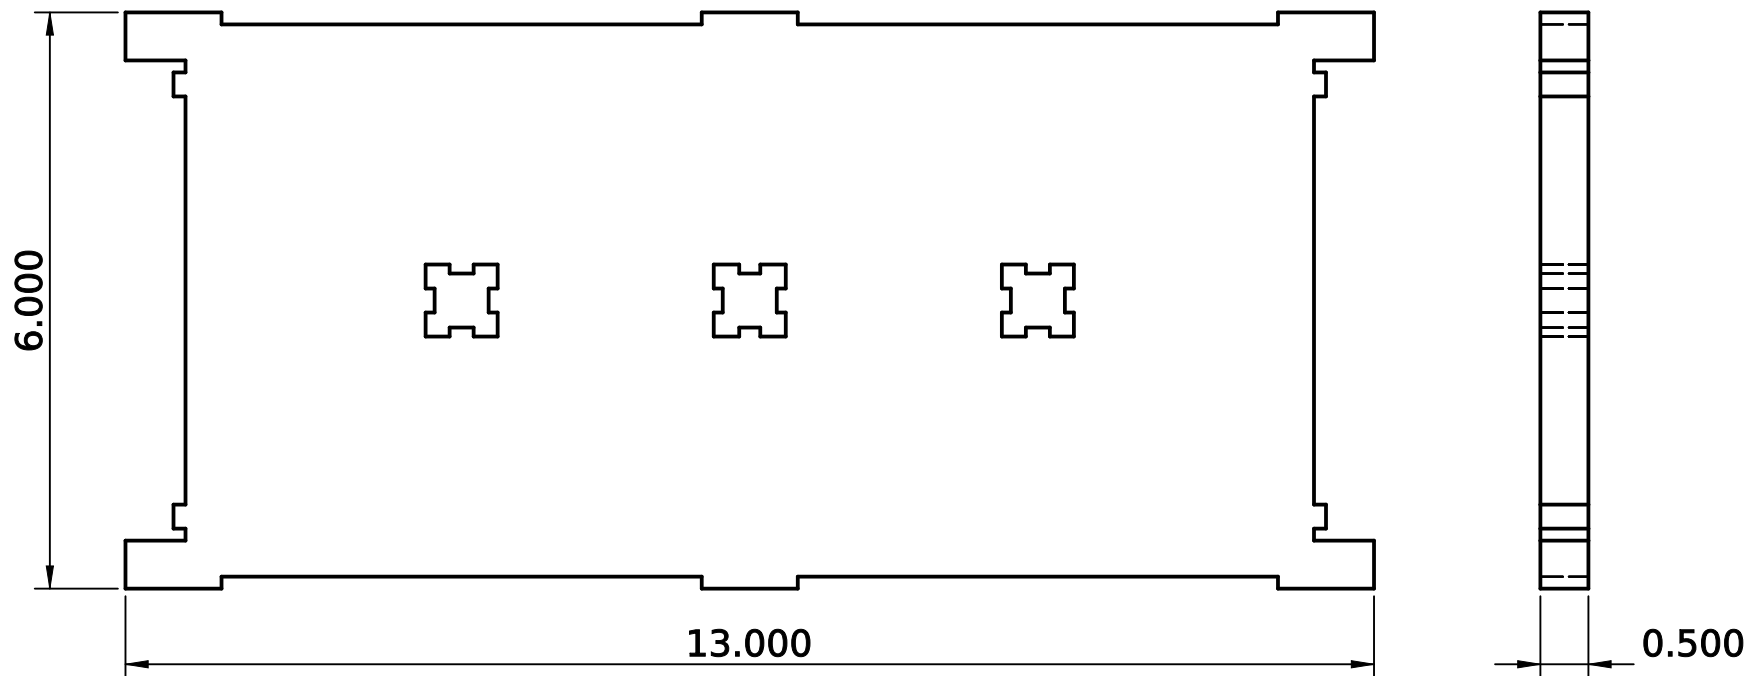

NOTES:

1. ALL DIMENSIONS IN INCHES. TOLERANCE $\pm 1/32$ UNLESS NOTED.
2. BREAK SHARP EDGES, REMOVE BURRS.
3. MATERIAL PER TITLE BLOCK. FILLET WELDS $1/4$ UNLESS NOTED.
4. OSE 01-025-00-2 / WELDMENT 001-0025, IN DRAWER ASSEMBLY. USED IN: DRAWER 1.
5. DXF LIBRARY L-D5: 13 X 6 X $1/2$ - MATCHES THE MODEL.
6. GEOMETRY FROM OSE FULL_ASSEMBLY.STP (CEB PRESS 6); TITLE BLOCKS OF OSE'S 2D SET SAY 'CEB PRESS 5'.


Material 1/2" plate, 6 x 13		Qty 1	Scale 1:2	Units inch	Projection 	
Created by J. Clements III		Approved by -		Document type Detail drawing	Status Draft	
Legal owner J. Clements III CEB Project	Title Soil Loading Drawer - Press Plate - D5 OSE CEB Press 6 (a-z Build 1.0)			Identification number OSEP6-P6-35		Sheet 45/94
				Rev A	Date of issue 2026-10-04	

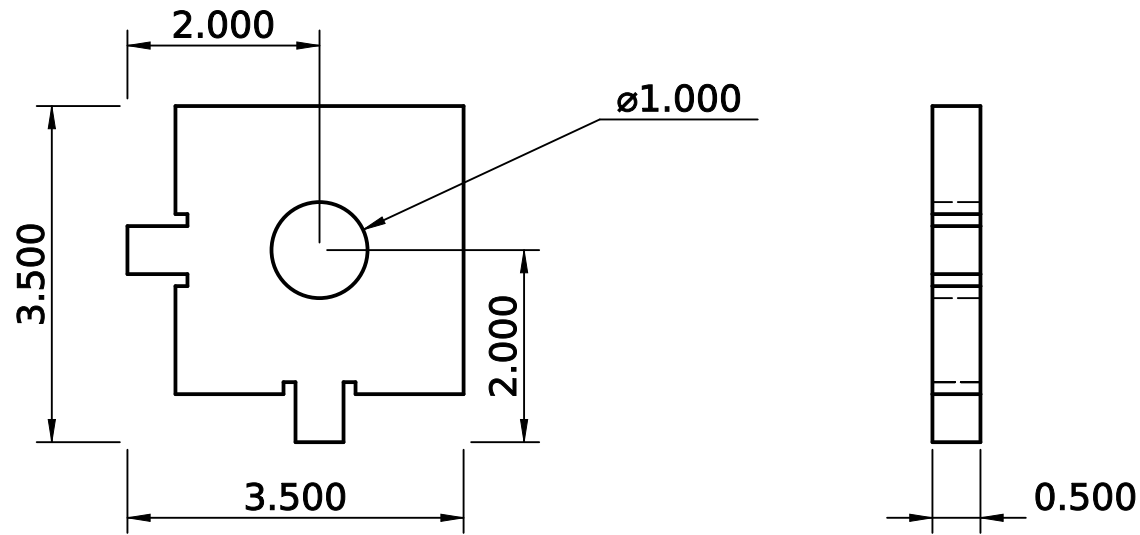

NOTES:

1. ALL DIMENSIONS IN INCHES. TOLERANCE $\pm 1/32$ UNLESS NOTED.
2. BREAK SHARP EDGES, REMOVE BURRS.
3. MATERIAL PER TITLE BLOCK. FILLET WELDS $1/4$ UNLESS NOTED.
4. OSE 01-028-00-2 / WELDMENT 001-0028, IN DRAWER ASSEMBLY. USED IN: DRAWER 2.
5. DXF LIBRARY L-D9: 3-1/2 X 3-1/2 X 1/2 - MATCHES THE MODEL.
6. GEOMETRY FROM OSE FULL_ASSEMBLY.STP (CEB PRESS 6); TITLE BLOCKS OF OSE'S 2D SET SAY 'CEB PRESS 5'.


Material 1/2" plate, 3-1/2 x 3-1/2		Qty 2	Scale 1:2	Units inch	Projection 
Created by J. Clements III		Approved by -		Document type Detail drawing	Status Draft
Legal owner J. Clements III CEB Project	Title Soil Loading Drawer - Tongue LBS OSE CEB Press 6 (a-z Build 1.0)			Identification number OSEP6-P6-36	Sheet 46/94
				Rev A	

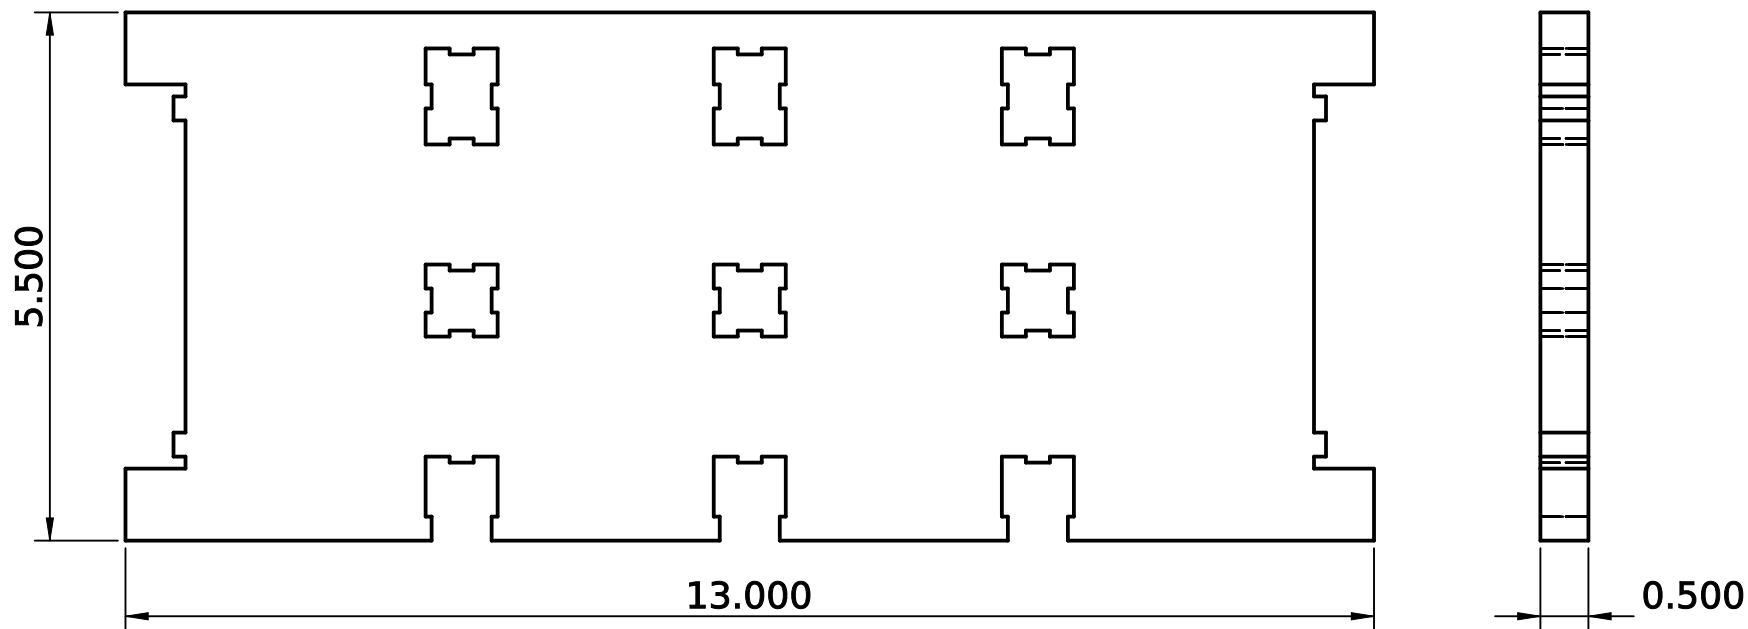

NOTES:

1. ALL DIMENSIONS IN INCHES. TOLERANCE $\pm 1/32$ UNLESS NOTED.
2. BREAK SHARP EDGES, REMOVE BURRS.
3. MATERIAL PER TITLE BLOCK. FILLET WELDS $1/4$ UNLESS NOTED.
4. OSE 01-029-00-2 / WELDMENT 001-0029, IN DRAWER ASSEMBLY. USED IN: DRAWER 2.
5. DXF LIBRARY L-D3: 13 X 5-1/2 X 1/2 - MATCHES THE MODEL.
6. GEOMETRY FROM OSE FULL_ASSEMBLY.STP (CEB PRESS 6); TITLE BLOCKS OF OSE'S 2D SET SAY 'CEB PRESS 5'.


Material 1/2" plate, 5-1/2 x 13		Qty 2	Scale 1:2	Units inch	Projection 
Created by J. Clements III		Approved by -		Document type Detail drawing	Status Draft
Legal owner J. Clements III CEB Project	Title Soil Loading Drawer - Vertical Supports OSE CEB Press 6 (a-z Build 1.0)			Identification number OSEP6-R6-37 Rev A Date of issue 2026-10-04	Sheet 47/94

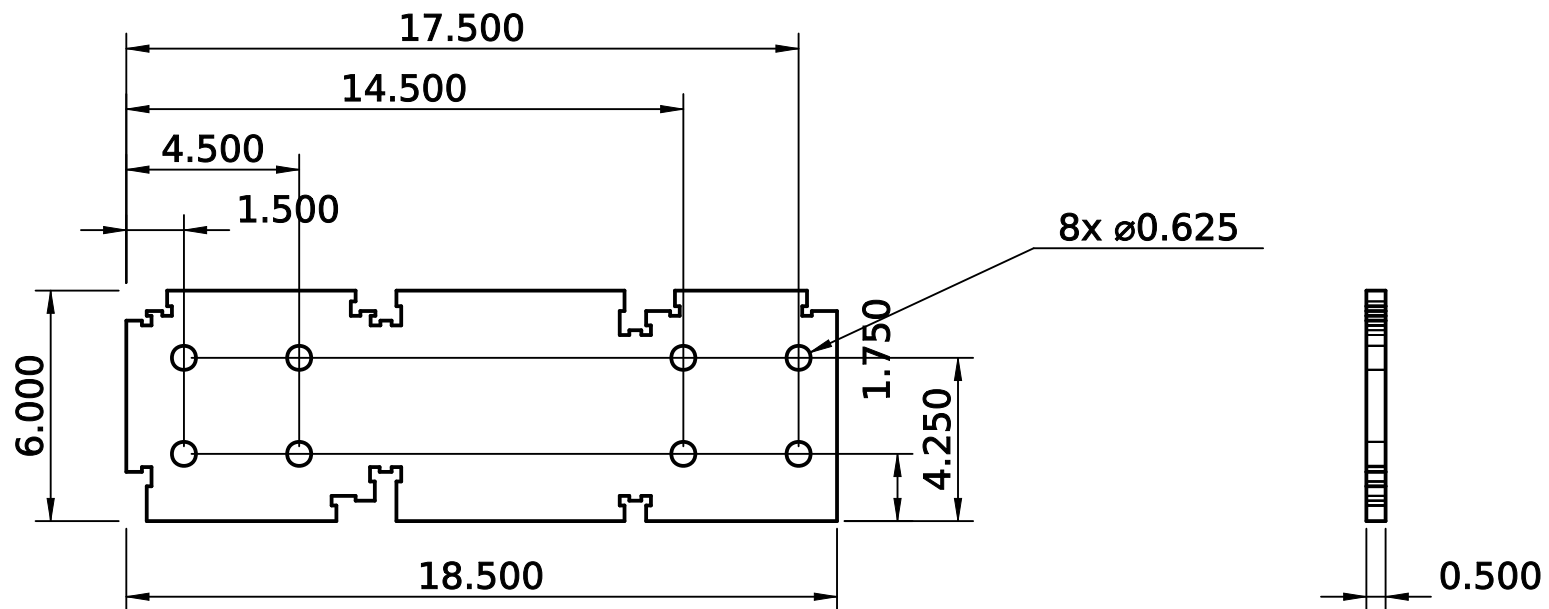

NOTES:

1. ALL DIMENSIONS IN INCHES. TOLERANCE $\pm 1/32$ UNLESS NOTED.
2. BREAK SHARP EDGES, REMOVE BURRS.
3. MATERIAL PER TITLE BLOCK. FILLET WELDS $1/4$ UNLESS NOTED.
4. OSE 01-030-00-2 / WELDMENT 001-0030, IN DRAWER ASSEMBLY. USED IN: DRAWER 2.
5. DXF LIBRARY L-D2: 18-1/2 X 6 X 1/2 - MATCHES THE MODEL.
6. GEOMETRY FROM OSE FULL_ASSEMBLY.STP (CEB PRESS 6); TITLE BLOCKS OF OSE'S 2D SET SAY 'CEB PRESS 5'.


Material 1/2" plate, 6 x 18-1/2		Qty 2	Scale 1:5	Units inch	Projection 
Created by J. Clements III		Approved by -		Document type Detail drawing	Status Draft
Legal owner J. Clements III CEB Project	Title Drawer Side L-D2 OSE CEB Press 6 (a-z Build 1.0)			Identification number OSEP6-P6-38	Sheet 48/94
				Rev A	

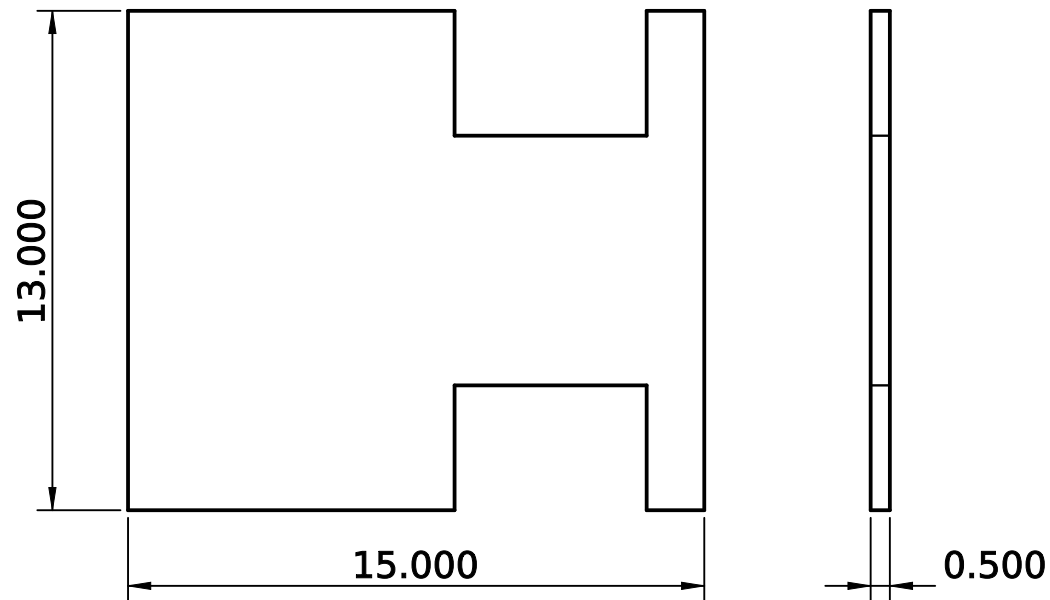

NOTES:

1. ALL DIMENSIONS IN INCHES. TOLERANCE $\pm 1/32$ UNLESS NOTED.
2. BREAK SHARP EDGES, REMOVE BURRS.
3. MATERIAL PER TITLE BLOCK. FILLET WELDS $1/4$ UNLESS NOTED.
4. OSE 01-032-00-2 / WELDMENT 001-0032, IN DRAWER ASSEMBLY. USED IN: DRAWER 1.
5. DXF LIBRARY L-D1: 15 X 13 X $1/2$ - MATCHES THE MODEL.
6. GEOMETRY FROM OSE FULL_ASSEMBLY.STP (CEB PRESS 6); TITLE BLOCKS OF OSE'S 2D SET SAY 'CEB PRESS 5'.


Material 1/2" plate, 13 x 15		Qty 1	Scale 1:5	Units inch	Projection 	
Created by J. Clements III		Approved by -	Document type Detail drawing		Status Draft	
Legal owner J. Clements III CEB Project	Title Soil Loading Drawer - Roof L-D1 OSE CEB Press 6 (a-z Build 1.0)			Identification number OSEP6-P6-39		Sheet 49/94
				Rev A	Date of issue 2026-10-04	

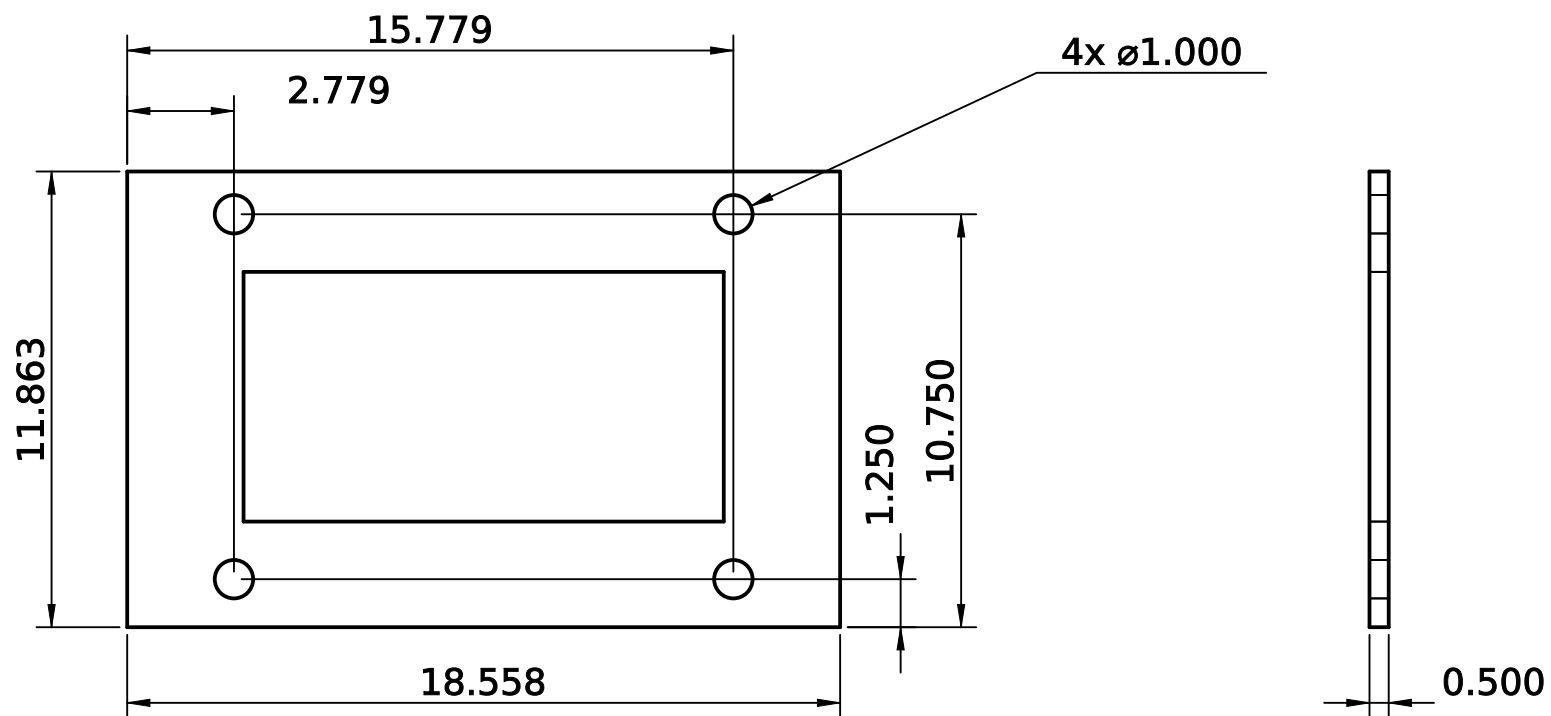

NOTES:

1. ALL DIMENSIONS IN INCHES. TOLERANCE $\pm 1/32$ UNLESS NOTED.
2. BREAK SHARP EDGES, REMOVE BURRS.
3. MATERIAL PER TITLE BLOCK. FILLET WELDS $1/4$ UNLESS NOTED.
4. OSE 01-126-00-0, IN SADDLE WELDMENT. USED IN: DRAWER 1.
5. DXF LIBRARY L-F8: 18.558 X 11.863 X $1/2$ - MATCHES THE MODEL.
6. GEOMETRY FROM OSE FULL_ASSEMBLY.STP (CEB PRESS 6); TITLE BLOCKS OF OSE'S 2D SET SAY 'CEB PRESS 5'.


Material 1/2" plate, 11.863 x 18.558		Qty 1	Scale 1:5	Units inch	Projection 	
Created by J. Clements III		Approved by -	Document type Detail drawing		Status Draft	
Legal owner J. Clements III CEB Project	Title Saddle Plate L-F8 OSE CEB Press 6 (a-z Build 1.0)			Identification number OSEP6-P6-40		Sheet 50/94
				Rev A	Date of issue 2026-10-04	

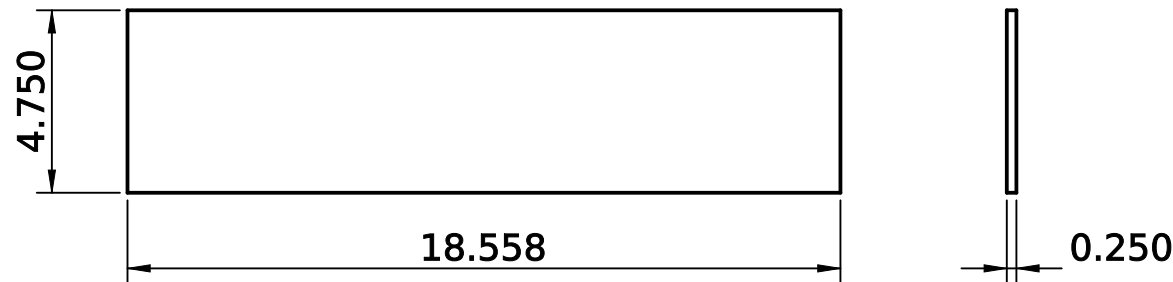

NOTES:

1. ALL DIMENSIONS IN INCHES. TOLERANCE $\pm 1/32$ UNLESS NOTED.
2. BREAK SHARP EDGES, REMOVE BURRS.
3. MATERIAL PER TITLE BLOCK. FILLET WELDS $1/4$ UNLESS NOTED.
4. OSE 01-128-00-0, IN SADDLE WELDMENT. USED IN: DRAWER 1.
5. DXF LIBRARY L-Q5: 18.558 X 4-3/4 X 1/4 - MATCHES THE MODEL.
6. GEOMETRY FROM OSE FULL_ASSEMBLY.STP (CEB PRESS 6); TITLE BLOCKS OF OSE'S 2D SET SAY 'CEB PRESS 5'.


Material 1/4" plate, 4-3/4 x 18.558		Qty 1	Scale 1:5	Units inch	Projection 	
Created by J. Clements III		Approved by -		Document type Detail drawing	Status Draft	
Legal owner J. Clements III CEB Project	Title Saddle Plate L-Q5 OSE CEB Press 6 (a-z Build 1.0)			Identification number OSEP6-P6-41		Sheet 51/94
				Rev A	Date of issue 2026-10-04	

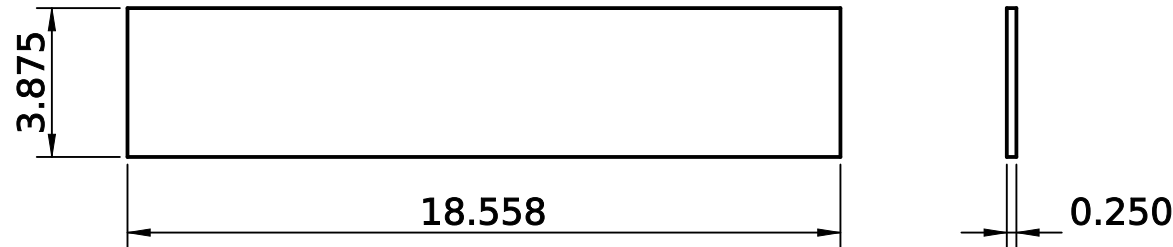

NOTES:

1. ALL DIMENSIONS IN INCHES. TOLERANCE $\pm 1/32$ UNLESS NOTED.
2. BREAK SHARP EDGES, REMOVE BURRS.
3. MATERIAL PER TITLE BLOCK. FILLET WELDS $1/4$ UNLESS NOTED.
4. OSE 01-129-00-0, IN SADDLE WELDMENT. USED IN: DRAWER 1.
5. DXF LIBRARY L-Q3: 18.558 X $3-7/8$ X $1/4$ - MATCHES THE MODEL.
6. GEOMETRY FROM OSE FULL_ASSEMBLY.STP (CEB PRESS 6); TITLE BLOCKS OF OSE'S 2D SET SAY 'CEB PRESS 5'.


Material 1/4" plate, 3-7/8 x 18.558		Qty 1	Scale 1:5	Units inch	Projection 	
Created by J. Clements III		Approved by -		Document type Detail drawing	Status Draft	
Legal owner J. Clements III CEB Project	Title Saddle Plate L-Q3 OSE CEB Press 6 (a-z Build 1.0)			Identification number OSEP6-P6-42		Sheet 52/94
				Rev A	Date of issue 2026-10-04	

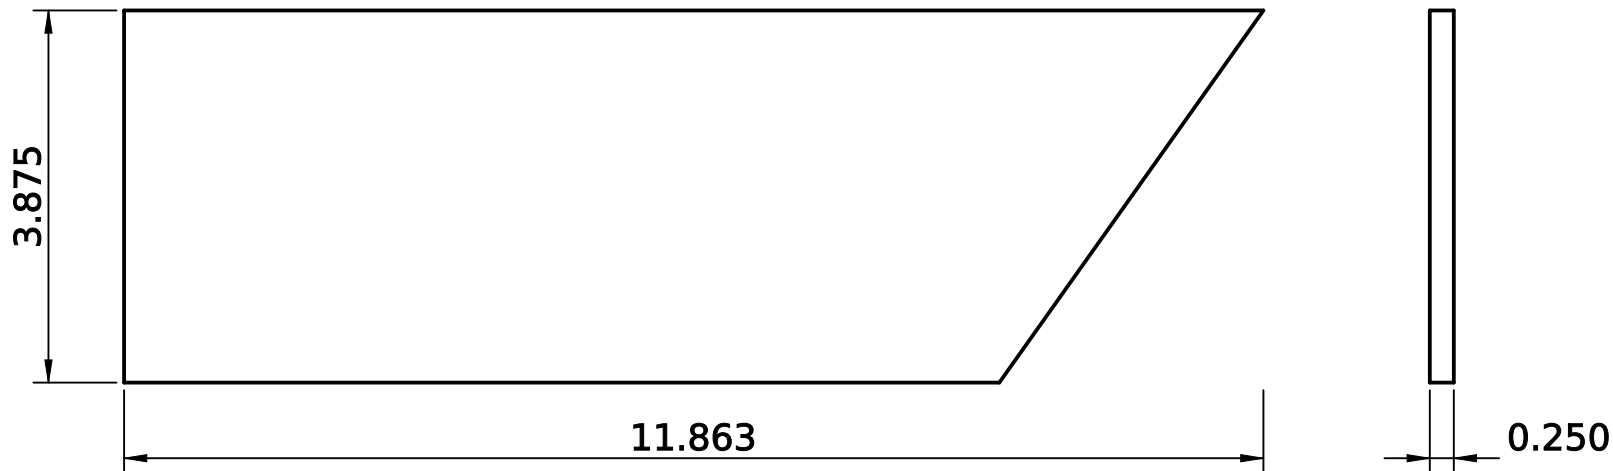

NOTES:

1. ALL DIMENSIONS IN INCHES. TOLERANCE $\pm 1/32$ UNLESS NOTED.
2. BREAK SHARP EDGES, REMOVE BURRS.
3. MATERIAL PER TITLE BLOCK. FILLET WELDS $1/4$ UNLESS NOTED.
4. OSE 01-130-00-0, IN SADDLE WELDMENT. USED IN: DRAWER 2.
5. DXF LIBRARY L-Q4: 11.863 X $3-7/8$ X $1/4$ - MATCHES THE MODEL.
6. GEOMETRY FROM OSE FULL_ASSEMBLY.STP (CEB PRESS 6); TITLE BLOCKS OF OSE'S 2D SET SAY 'CEB PRESS 5'.


Material 1/4" plate, 3-7/8 x 11.863		Qty 2	Scale 1:2	Units inch	Projection 	
Created by J. Clements III		Approved by -		Document type Detail drawing	Status Draft	
Legal owner J. Clements III CEB Project	Title Saddle Plate L-Q4 OSE CEB Press 6 (a-z Build 1.0)			Identification number OSEP6-P6-43		Sheet 53/94
				Rev A	Date of issue 2026-10-04	

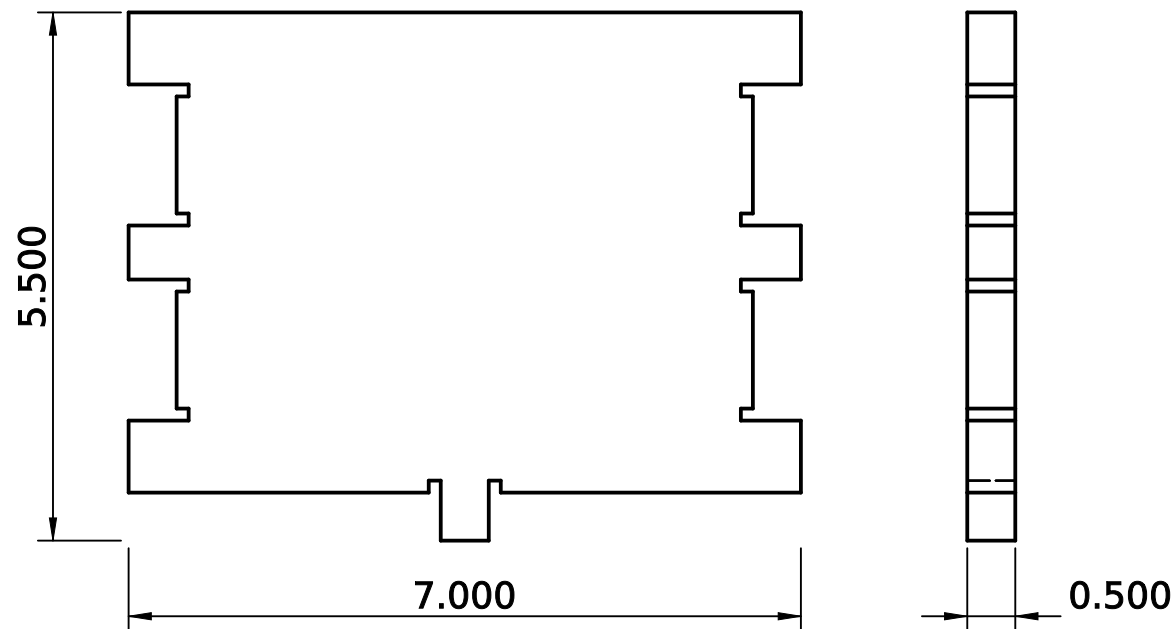

NOTES:

1. ALL DIMENSIONS IN INCHES. TOLERANCE $\pm 1/32$ UNLESS NOTED.
2. BREAK SHARP EDGES, REMOVE BURRS.
3. MATERIAL PER TITLE BLOCK. FILLET WELDS $1/4$ UNLESS NOTED.
4. OSE 01-132-00-2, IN DRAWER ASSEMBLY. USED IN: DRAWER 3.
5. DXF LIBRARY L-D4: 7 X 5-1/2 X 1/2 - MATCHES THE MODEL.
6. GEOMETRY FROM OSE FULL_ASSEMBLY.STP (CEB PRESS 6); TITLE BLOCKS OF OSE'S 2D SET SAY 'CEB PRESS 5'.


Material 1/2" plate, 5-1/2 x 7		Qty 3	Scale 1:2	Units inch	Projection 	
Created by J. Clements III		Approved by -		Document type Detail drawing	Status Draft	
Legal owner J. Clements III CEB Project	Title Drawer Plate L-D4 OSE CEB Press 6 (a-z Build 1.0)			Identification number OSEP6-P6-44		Sheet 54/94
				Rev A	Date of issue 2026-10-04	

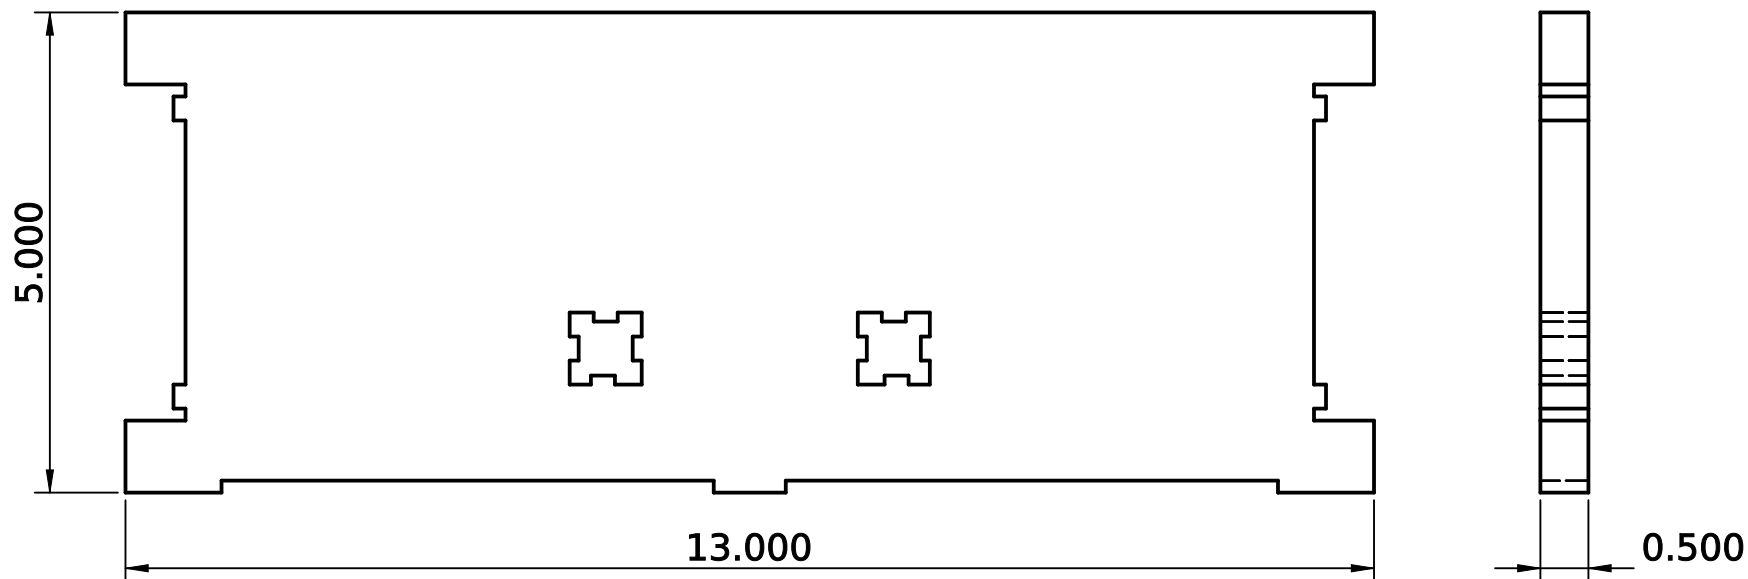

NOTES:

1. ALL DIMENSIONS IN INCHES. TOLERANCE $\pm 1/32$ UNLESS NOTED.
2. BREAK SHARP EDGES, REMOVE BURRS.
3. MATERIAL PER TITLE BLOCK. FILLET WELDS $1/4$ UNLESS NOTED.
4. OSE 01-133-00-2, IN DRAWER ASSEMBLY. USED IN: DRAWER 1.
5. DXF LIBRARY L-D8: 13 X 5 X $1/2$ - MATCHES THE MODEL.
6. GEOMETRY FROM OSE FULL_ASSEMBLY.STP (CEB PRESS 6); TITLE BLOCKS OF OSE'S 2D SET SAY 'CEB PRESS 5'.


Material 1/2" plate, 5 x 13		Qty 1	Scale 1:2	Units inch	Projection 
Created by J. Clements III		Approved by -		Document type Detail drawing	Status Draft
Legal owner J. Clements III CEB Project	Title Drawer Plate L-D8 OSE CEB Press 6 (a-z Build 1.0)			Identification number OSEP6-P6-45	Sheet 55/94
				Rev A	

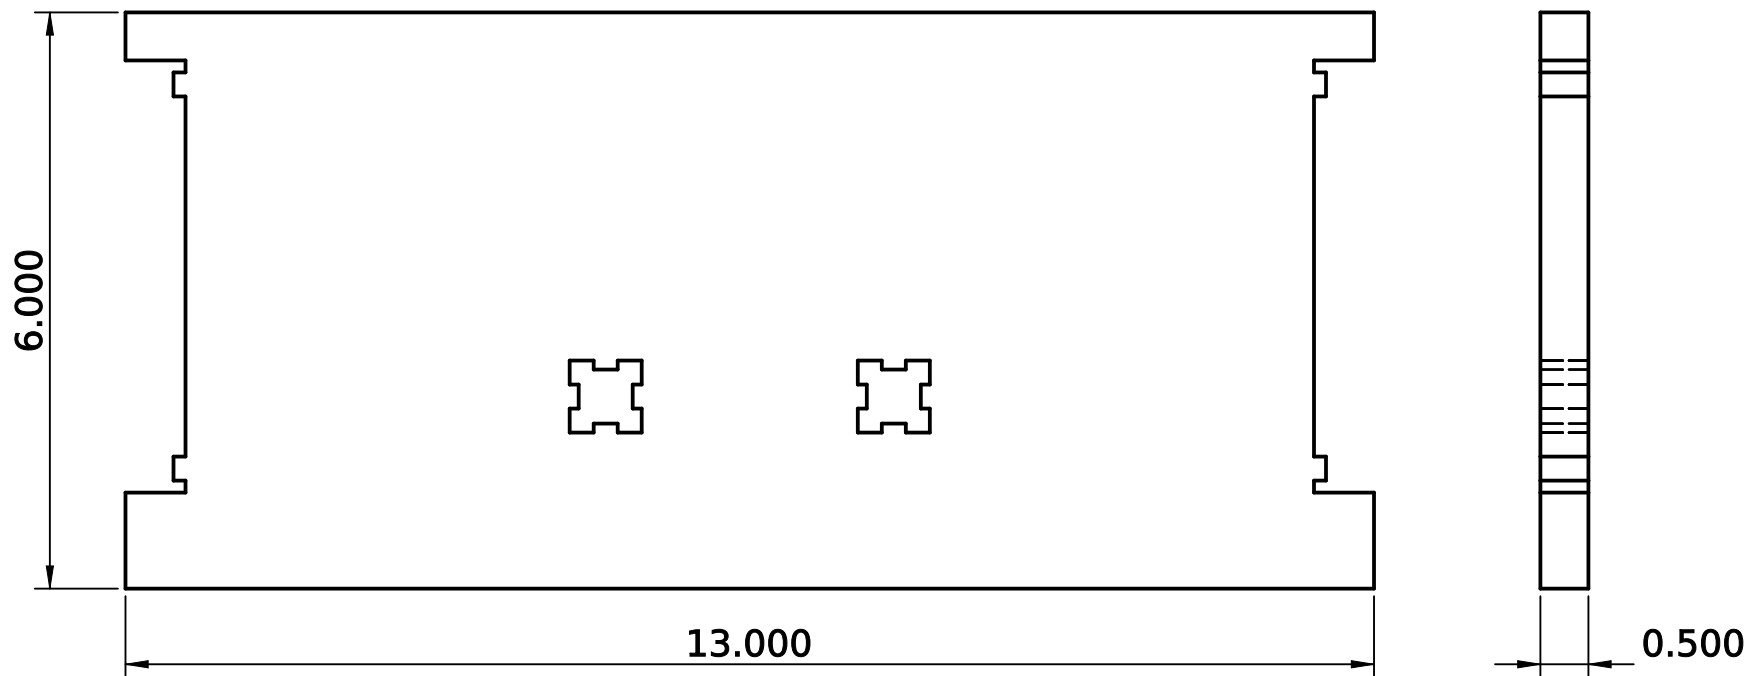

NOTES:


1. ALL DIMENSIONS IN INCHES. TOLERANCE $\pm 1/32$ UNLESS NOTED.
2. BREAK SHARP EDGES, REMOVE BURRS.
3. MATERIAL PER TITLE BLOCK. FILLET WELDS $1/4$ UNLESS NOTED.
4. OSE 01-134-00-2, IN DRAWER ASSEMBLY. USED IN: DRAWER 1.
5. DXF LIBRARY L-D6: 13 X 6 X $1/2$ - MATCHES THE MODEL.
6. GEOMETRY FROM OSE FULL_ASSEMBLY.STP (CEB PRESS 6); TITLE BLOCKS OF OSE'S 2D SET SAY 'CEB PRESS 5'.

Material 1/2" plate, 6 x 13		Qty 1	Scale 1:2	Units inch	Projection 	
Created by J. Clements III		Approved by -		Document type Detail drawing	Status Draft	
Legal owner J. Clements III CEB Project	Title Drawer Plate L-D6 OSE CEB Press 6 (a-z Build 1.0)			Identification number OSEP6-P6-46		Sheet 56/94
				Rev A	Date of issue 2026-10-04	

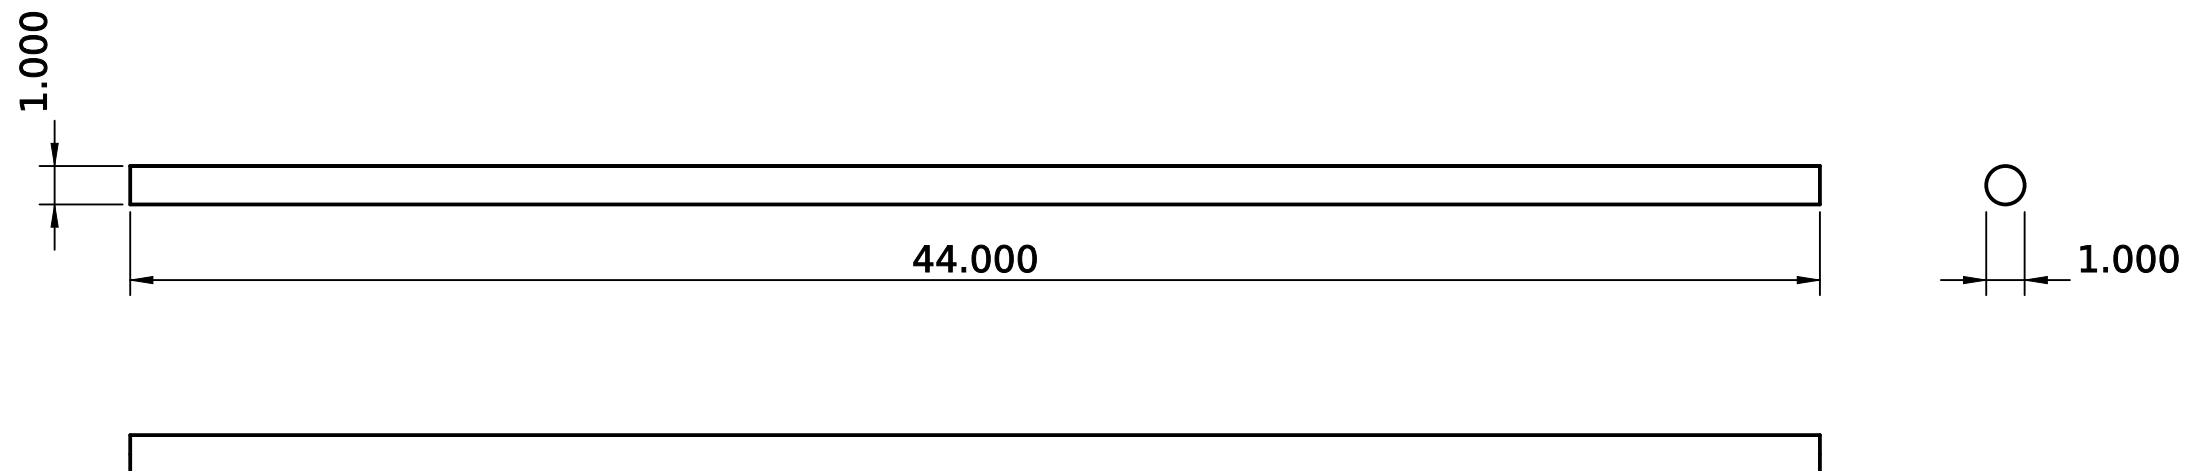

NOTES:
1. ALL DIMENSIONS IN INCHES. TOLERANCE $\pm 1/32$ UNLESS NOTED.
2. BREAK SHARP EDGES, REMOVE BURRS.
3. MATERIAL PER TITLE BLOCK. FILLET WELDS $1/4$ UNLESS NOTED.
4. OSE 01-221-00-0, IN GUIDE ROD ASSEMBLY. USED IN: DRAWER 2.
5. GEOMETRY FROM OSE FULL_ASSEMBLY.STP (CEB PRESS 6); TITLE BLOCKS OF OSE'S 2D SET SAY 'CEB PRESS 5'.


Material 1IN ROUND BAR X 48IN		Qty 2	Scale 1:5	Units inch	Projection 
Created by J. Clements III		Approved by -		Document type Detail drawing	Status Draft
Legal owner J. Clements III CEB Project		Title Drawer Guide Rod OSE CEB Press 6 (a-z Build 1.0)		Identification number OSEP6-P6-47	Sheet 57/94
				Rev A	Date of issue 2026-10-04

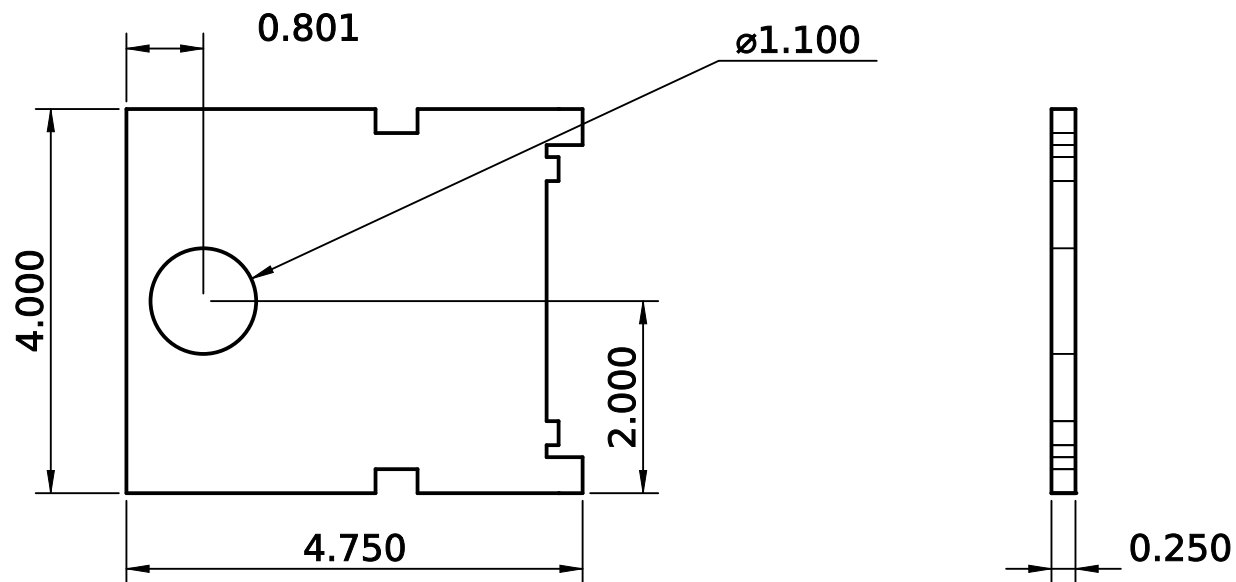

NOTES:

1. ALL DIMENSIONS IN INCHES. TOLERANCE $\pm 1/32$ UNLESS NOTED.
2. BREAK SHARP EDGES, REMOVE BURRS.
3. MATERIAL PER TITLE BLOCK. FILLET WELDS $1/4$ UNLESS NOTED.
4. OSE 01-239-00-0, IN SHAFT SUPPORT ASSEMBLY. USED IN: DRAWER 4.
5. DXF LIBRARY L-Q11: 4-3/4 X 4 X 1/4 - MATCHES THE MODEL.
6. GEOMETRY FROM OSE FULL_ASSEMBLY.STP (CEB PRESS 6); TITLE BLOCKS OF OSE'S 2D SET SAY 'CEB PRESS 5'.


Material 1/4" plate, 4 x 4-3/4		Qty 4	Scale 1:2	Units inch	Projection 	
Created by J. Clements III		Approved by -	Document type Detail drawing		Status Draft	
Legal owner J. Clements III CEB Project	Title Shaft Support Plate L-Q11 OSE CEB Press 6 (a-z Build 1.0)			Identification number OSEP6-P6-48		Sheet 58/94
				Rev A	Date of issue 2026-10-04	

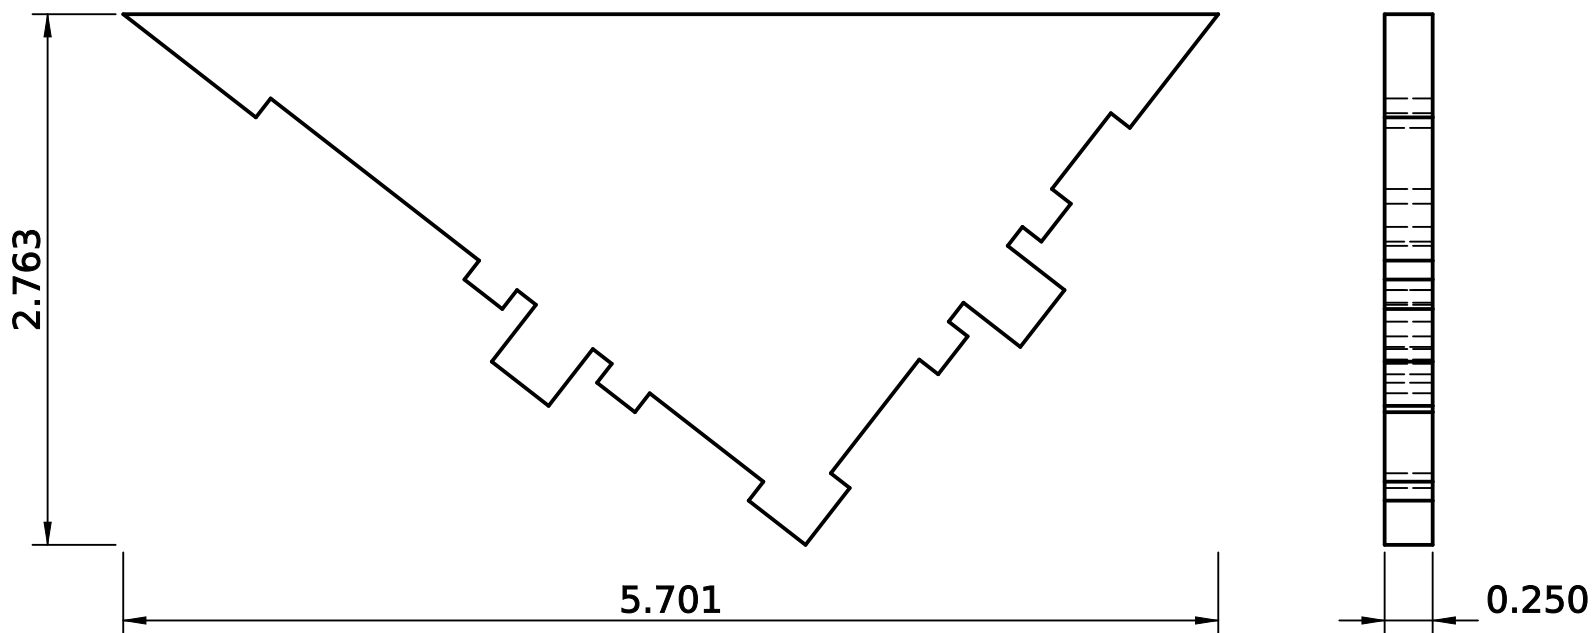

NOTES:

1. ALL DIMENSIONS IN INCHES. TOLERANCE $\pm 1/32$ UNLESS NOTED.
2. BREAK SHARP EDGES, REMOVE BURRS.
3. MATERIAL PER TITLE BLOCK. FILLET WELDS $1/4$ UNLESS NOTED.
4. OSE 01-241-00-0, IN SHAFT SUPPORT ASSEMBLY. USED IN: DRAWER 8.
5. DXF LIBRARY L-Q12: 4-3/4 X 3-3/4 X 1/4 - MODEL 5.701 X 2.763 X 1/4; CHECK.
6. GEOMETRY FROM OSE FULL_ASSEMBLY.STP (CEB PRESS 6); TITLE BLOCKS OF OSE'S 2D SET SAY 'CEB PRESS 5'.


Material 1/4" plate, 2.763 x 5.701		Qty 8	Scale 1:1	Units inch	Projection 	
Created by J. Clements III		Approved by -		Document type Detail drawing	Status Draft	
Legal owner J. Clements III CEB Project	Title Shaft Support Plate L-Q12 OSE CEB Press 6 (a-z Build 1.0)			Identification number OSEP6-P6-49		Sheet 59/94
				Rev A	Date of issue 2026-10-04	

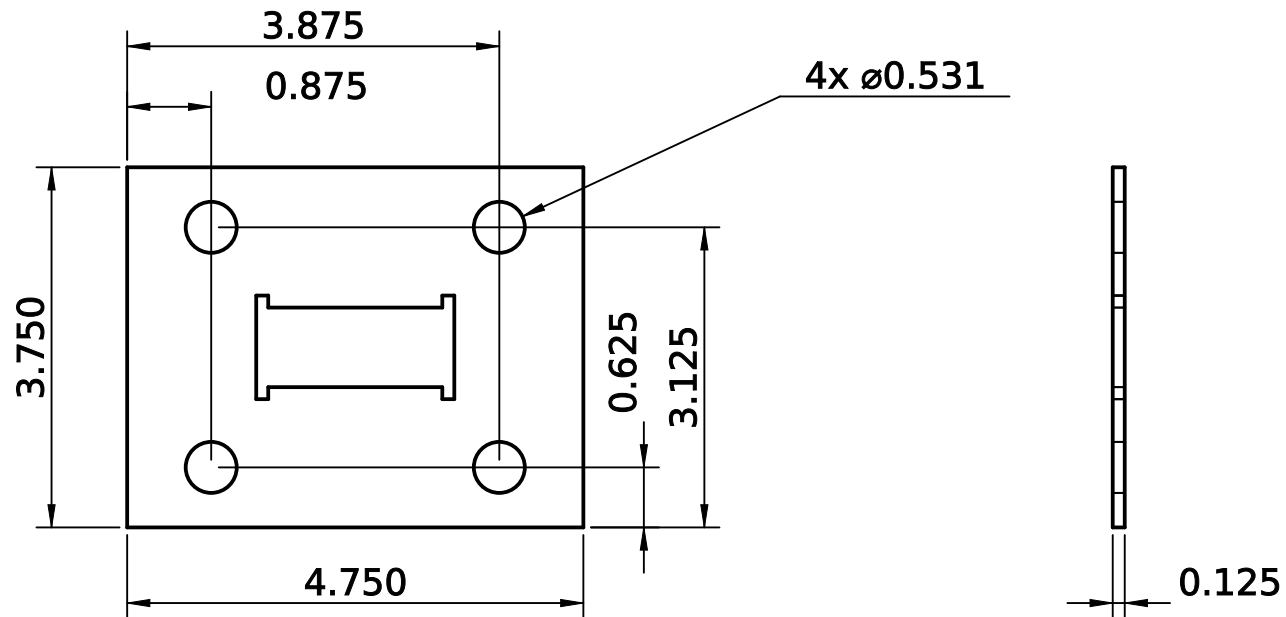

NOTES:

1. ALL DIMENSIONS IN INCHES. TOLERANCE $\pm 1/32$ UNLESS NOTED.
2. BREAK SHARP EDGES, REMOVE BURRS.
3. MATERIAL PER TITLE BLOCK. FILLET WELDS 1/4 UNLESS NOTED.
4. OSE 01-277-01-0, IN 01-236-01-0. USED IN: DRAWER 4.
5. L-H19 NOT FOUND IN THE ORIGINAL DXF LIBRARIES.
6. GEOMETRY FROM OSE FULL_ASSEMBLY.STP (CEB PRESS 6); TITLE BLOCKS OF OSE'S 2D SET SAY 'CEB PRESS 5'.

Material 1/8" plate, 3-3/4 x 4-3/4		Qty 4	Scale 1:2	Units inch	Projection 
Created by J. Clements III		Approved by -		Document type Detail drawing	Status Draft
Legal owner J. Clements III CEB Project	Title Plate L-H19 OSE CEB Press 6 (a-z Build 1.0)			Identification number OSEP6-P6-50	Sheet 60/94
				Rev A	


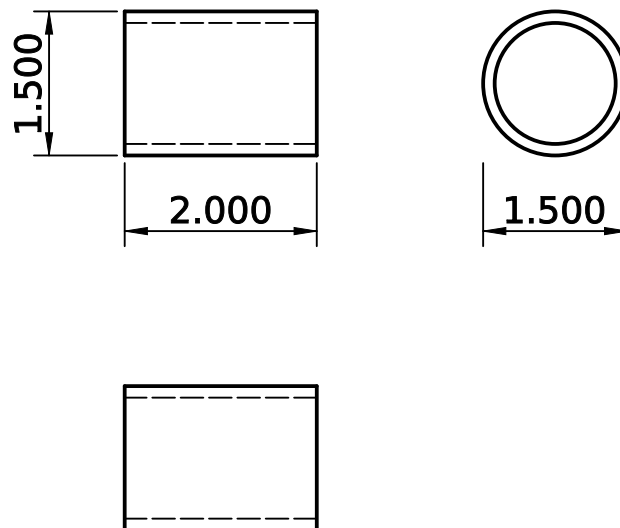


NOTES:

1. ALL DIMENSIONS IN INCHES. TOLERANCE $\pm 1/32$ UNLESS NOTED.
2. BREAK SHARP EDGES, REMOVE BURRS.
3. MATERIAL PER TITLE BLOCK. FILLET WELDS $1/4$ UNLESS NOTED.
4. OSE 01-286-00-0, IN 01-236-01-0. USED IN: DRAWER 4.
5. GEOMETRY FROM OSE FULL_ASSEMBLY.STP (CEB PRESS 6); TITLE BLOCKS OF OSE'S 2D SET SAY 'CEB PRESS 5'.

Material round / tube, 1-1/2 dia x 2		Qty 4	Scale 1:2	Units inch	Projection 	
Created by J. Clements III		Approved by -		Document type Detail drawing	Status Draft	
Legal owner J. Clements III CEB Project	Title Part 01-286 OSE CEB Press 6 (a-z Build 1.0)			Identification number OSEP6-P6-51		Sheet 61/94
				Rev A	Date of issue 2026-10-04	

2.000

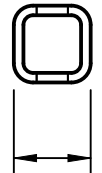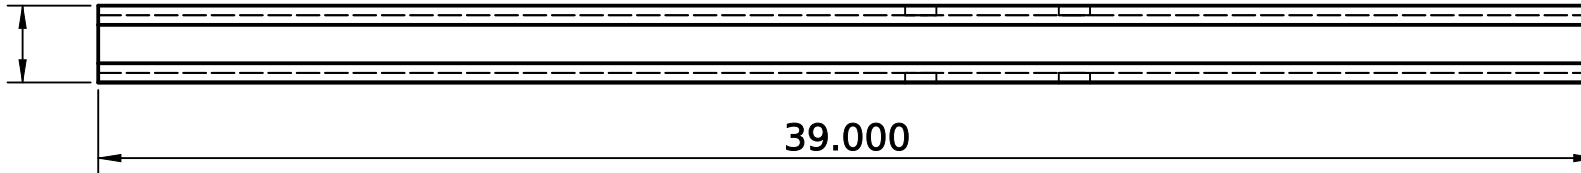


2.000



NOTES:

1. ALL DIMENSIONS IN INCHES. TOLERANCE $\pm 1/32$ UNLESS NOTED.
2. BREAK SHARP EDGES, REMOVE BURRS.
3. MATERIAL PER TITLE BLOCK. FILLET WELDS $1/4$ UNLESS NOTED.
4. OSE 01-049-00-0 / WELDMENT 001-0049. USED IN: HOPPER 2.
5. GEOMETRY FROM OSE FULL_ASSEMBLY.STP (CEB PRESS 6); TITLE BLOCKS OF OSE'S 2D SET SAY 'CEB PRESS 5'.


Material SQUARE TUBE, HSS2X2X1/4.		Qty 2	Scale 1:5	Units inch	Projection 	
Created by J. Clements III		Approved by -		Document type Detail drawing	Status Draft	
Legal owner J. Clements III CEB Project	Title Hopper Support OSE CEB Press 6 (a-z Build 1.0)			Identification number OSEP6-P6-52		Sheet 62/94
				Rev A	Date of issue 2026-10-04	

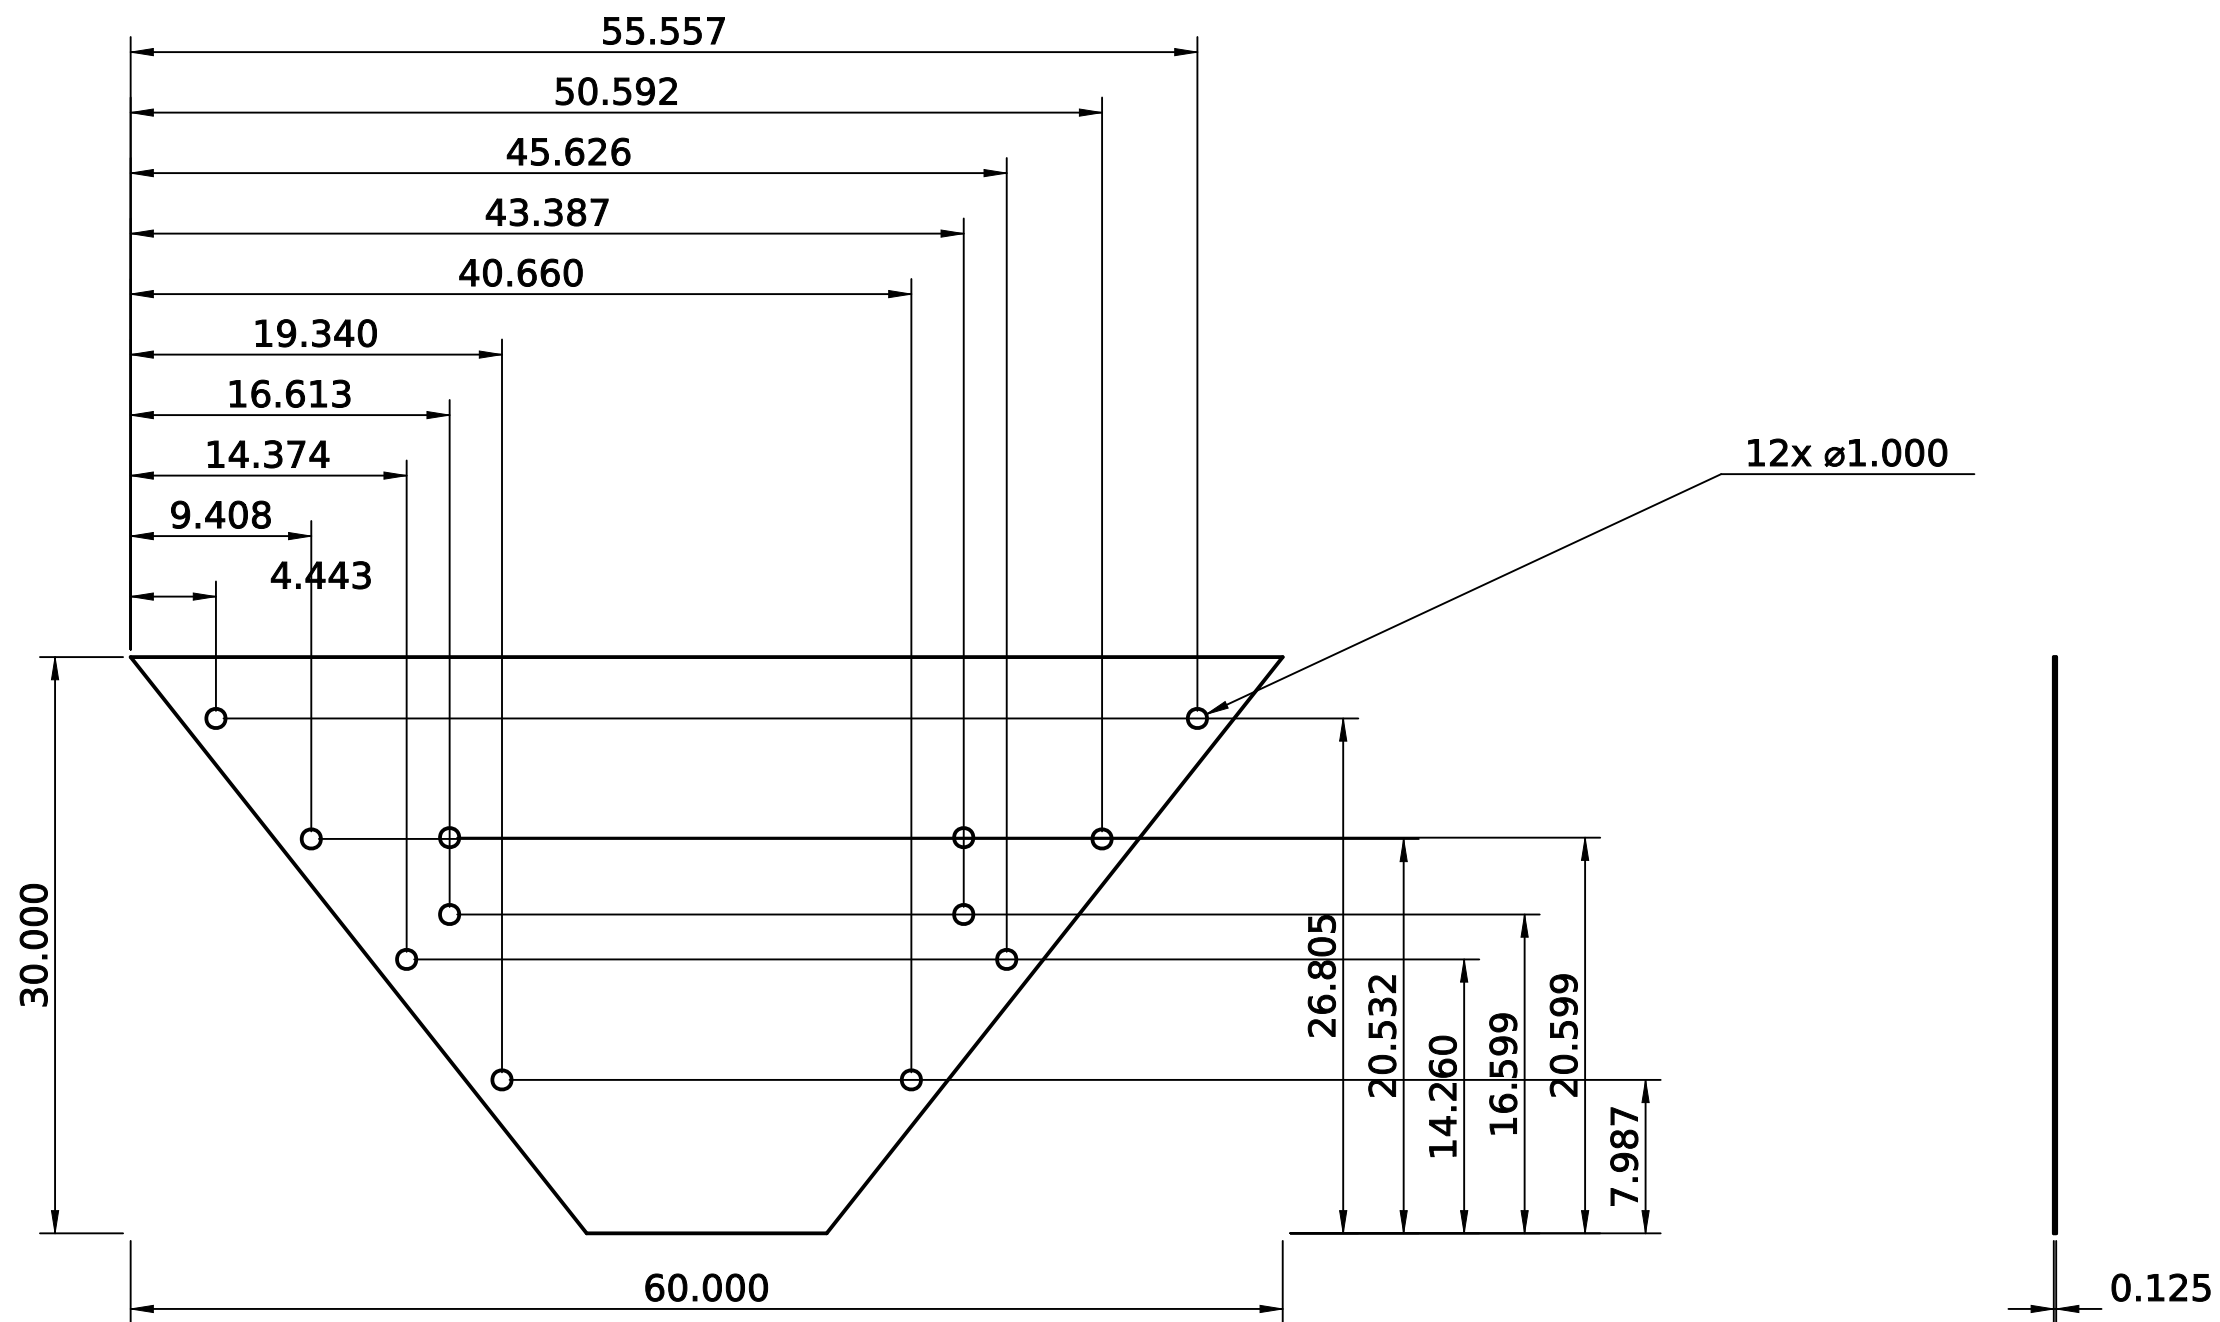

NOTES:

1. ALL DIMENSIONS IN INCHES. TOLERANCE $\pm 1/32$ UNLESS NOTED.
2. BREAK SHARP EDGES, REMOVE BURRS.
3. MATERIAL PER TITLE BLOCK. FILLET WELDS $1/4$ UNLESS NOTED.
4. OSE 01-060-00-0 / WELDMENT 001-0060, IN HOPPER ASSEMBLY. USED IN: HOPPER 1.
5. DXF LIBRARY L-H2: 60 X 30 X $1/8$ - MATCHES THE MODEL.
6. OSE 2015 WELDMENT REDRAW MAKES IT FROM 11 GAUGE STEEL SHEET INSTEAD.
7. GEOMETRY FROM OSE FULL_ASSEMBLY.STP (CEB PRESS 6); TITLE BLOCKS OF OSE'S 2D SET SAY 'CEB PRESS 5'.


Material 1/8" plate, 30 x 60		Qty 1	Scale 1:10	Units inch	Projection 
Created by J. Clements III		Approved by -		Document type Detail drawing	
Legal owner J. Clements III CEB Project		Title Hopper Sheet L-H2 OSE CEB Press 6 (a-z Build 1.0)			Identification number OSEP6-P6-53
					Rev A
					Date of issue 2026-10-04
					Sheet 63/94

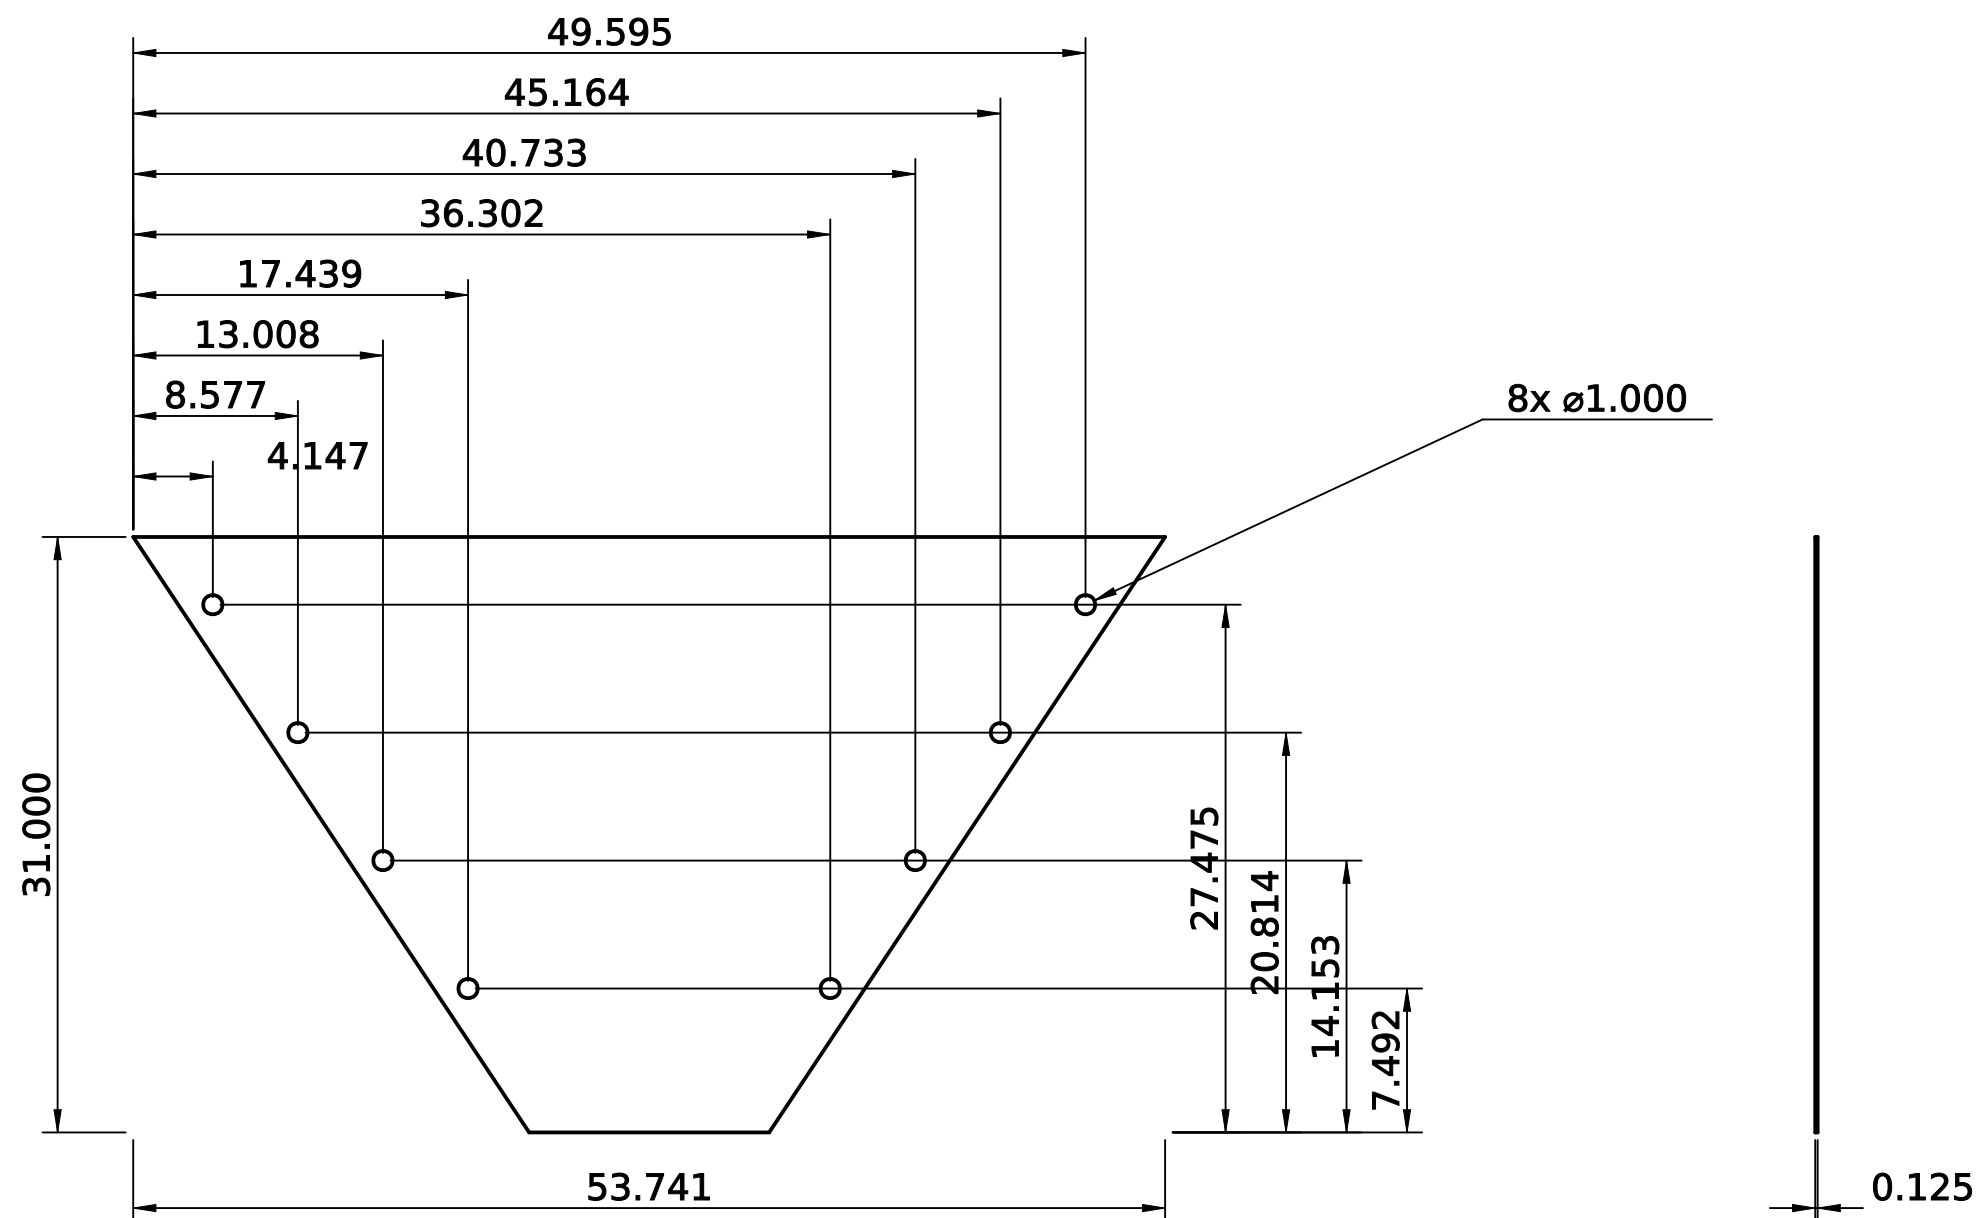

NOTES:

1. ALL DIMENSIONS IN INCHES. TOLERANCE $\pm 1/32$ UNLESS NOTED.
2. BREAK SHARP EDGES, REMOVE BURRS.
3. MATERIAL PER TITLE BLOCK. FILLET WELDS $1/4$ UNLESS NOTED.
4. OSE 01-061-00-0 / WELDMENT 001-0061, IN HOPPER ASSEMBLY. USED IN: HOPPER 1.
5. DXF LIBRARY L-H3: 53.741 X 31 X $1/8$ - MATCHES THE MODEL.
6. OSE 2015 WELDMENT REDRAW MAKES IT FROM 11 GAUGE STEEL SHEET INSTEAD.
7. GEOMETRY FROM OSE FULL_ASSEMBLY.STP (CEB PRESS 6); TITLE BLOCKS OF OSE'S 2D SET SAY 'CEB PRESS 5'.


Material 1/8" plate, 31 x 53.741		Qty 1	Scale 1:10	Units inch	Projection 
Created by J. Clements III		Approved by -		Document type Detail drawing	Status Draft
Legal owner J. Clements III CEB Project		Title Hopper Sheet L-H3 OSE CEB Press 6 (a-z Build 1.0)			Identification number OSEP6-P6-54
					Rev A
					Date of issue 2026-10-04
					Sheet 64/94

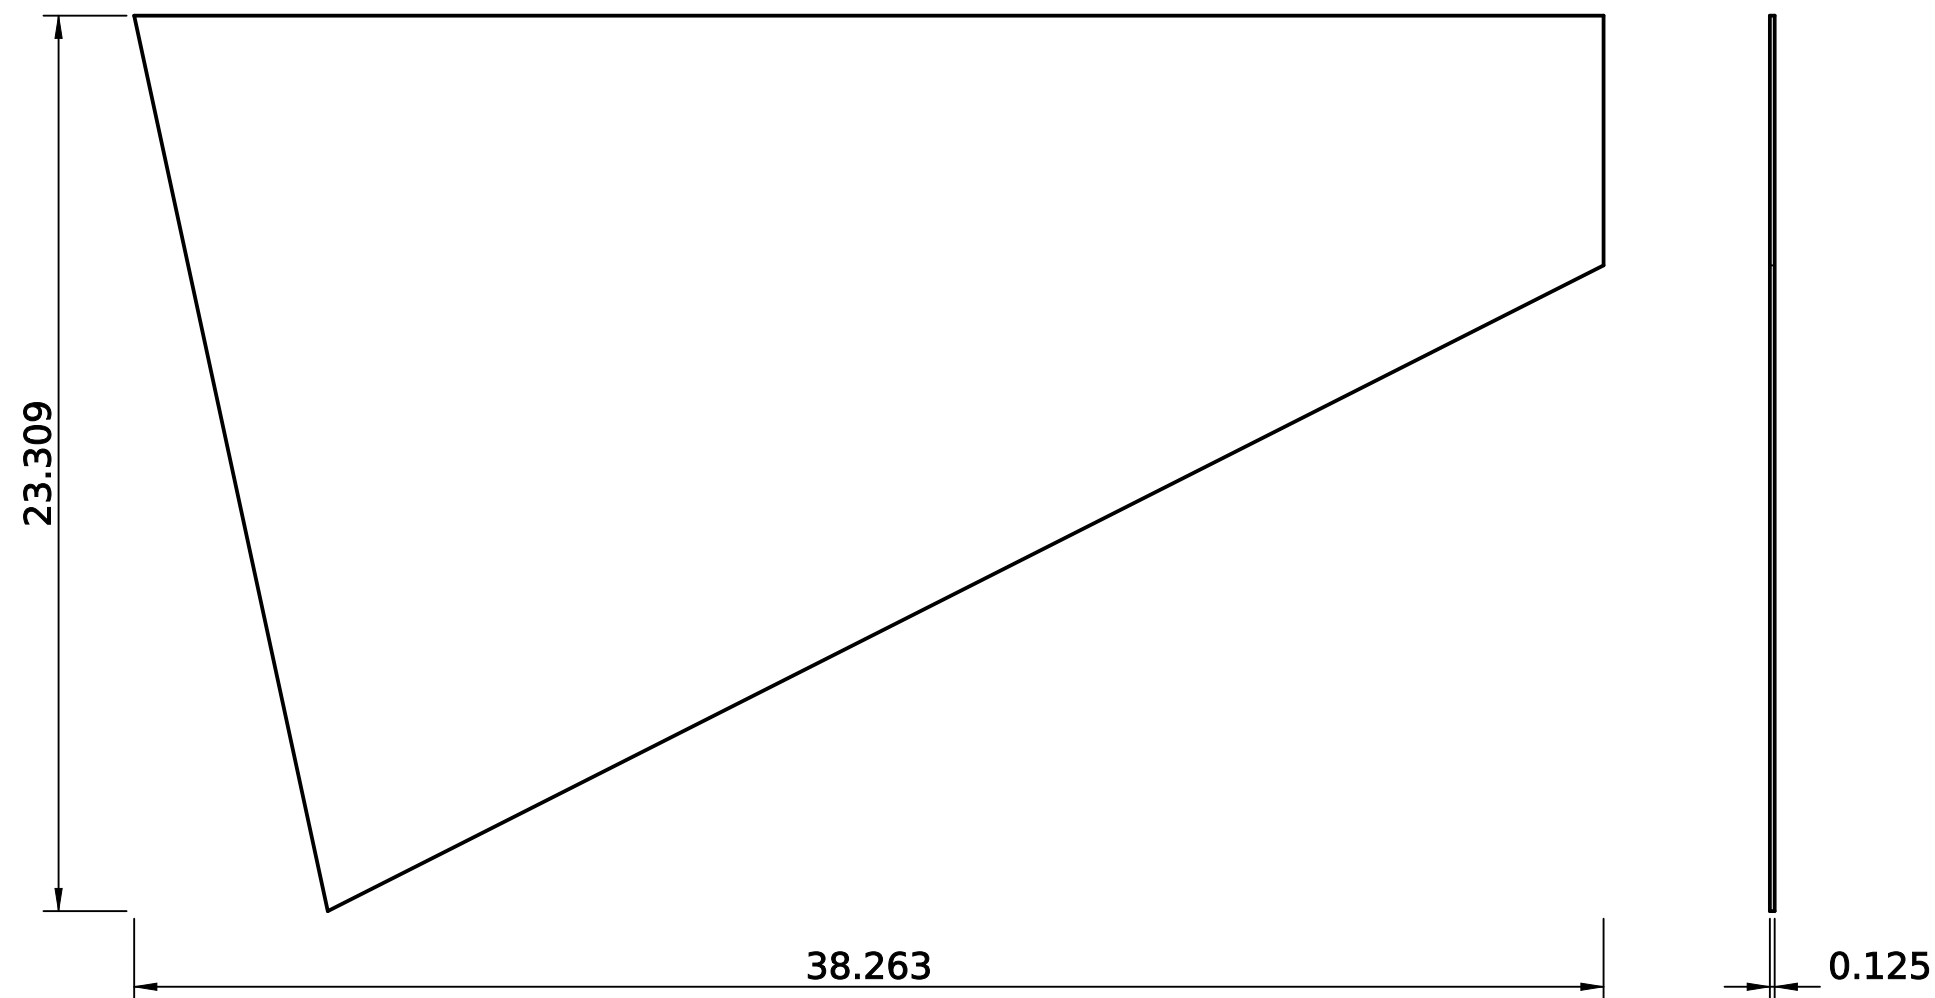

NOTES:

1. ALL DIMENSIONS IN INCHES. TOLERANCE $\pm 1/32$ UNLESS NOTED.
2. BREAK SHARP EDGES, REMOVE BURRS.
3. MATERIAL PER TITLE BLOCK. FILLET WELDS $1/4$ UNLESS NOTED.
4. OSE 01-062-00-0 / WELDMENT 001-0062, IN HOPPER ASSEMBLY. USED IN: HOPPER 2.
5. DXF LIBRARY L-H1: 38.263 X 23-5/16 X $1/8$ - MATCHES THE MODEL.
6. OSE 2015 WELDMENT REDRAW MAKES IT FROM 11 GAUGE STEEL INSTEAD.
7. GEOMETRY FROM OSE FULL_ASSEMBLY.STP (CEB PRESS 6); TITLE BLOCKS OF OSE'S 2D SET SAY 'CEB PRESS 5'.

Material 1/8" plate, 23-5/16 x 38.263		Qty 2	Scale 1:5	Units inch	Projection 	
Created by J. Clements III		Approved by -		Document type Detail drawing	Status Draft	
Legal owner J. Clements III CEB Project	Title Hopper Side Sheet L-H1 OSE CEB Press 6 (a-z Build 1.0)			Identification number OSEP6-P6-55		Sheet 65/94
				Rev A	Date of issue 2026-10-04	

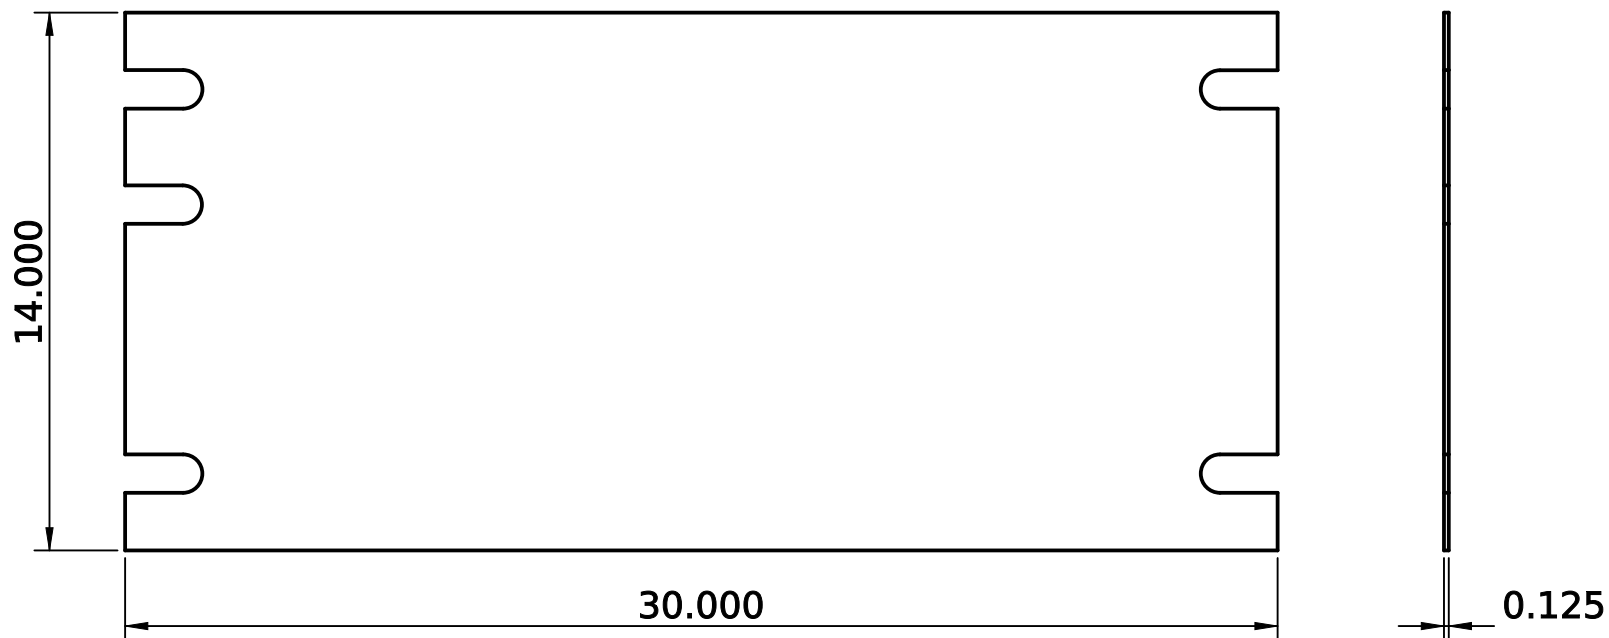

NOTES:

1. ALL DIMENSIONS IN INCHES. TOLERANCE $\pm 1/32$ UNLESS NOTED.
2. BREAK SHARP EDGES, REMOVE BURRS.
3. MATERIAL PER TITLE BLOCK. FILLET WELDS $1/4$ UNLESS NOTED.
4. OSE 01-079-00-0. USED IN: HOPPER 1.
5. DXF LIBRARY L-H9: 30 X 14 X $1/8$ - MATCHES THE MODEL.
6. GEOMETRY FROM OSE FULL_ASSEMBLY.STP (CEB PRESS 6); TITLE BLOCKS OF OSE'S 2D SET SAY 'CEB PRESS 5'.


Material 1/8" plate, 14 x 30		Qty 1	Scale 1:5	Units inch	Projection 
Created by J. Clements III		Approved by -		Document type Detail drawing	Status Draft
Legal owner J. Clements III CEB Project	Title Brick Holder Plate L-H9 OSE CEB Press 6 (a-z Build 1.0)			Identification number OSEP6-P6-56	Sheet 66/94
				Rev A	



NOTES:

1. ALL DIMENSIONS IN INCHES. TOLERANCE $\pm 1/32$ UNLESS NOTED.
2. BREAK SHARP EDGES, REMOVE BURRS.
3. MATERIAL PER TITLE BLOCK. FILLET WELDS $1/4$ UNLESS NOTED.
4. OSE 01-080-00-0. USED IN: HOPPER 1.
5. DXF LIBRARY L-H8: 30 X 13-1/2 X 1/8 - MATCHES THE MODEL.
6. GEOMETRY FROM OSE FULL_ASSEMBLY.STP (CEB PRESS 6); TITLE BLOCKS OF OSE'S 2D SET SAY 'CEB PRESS 5'.


Material 1/8" plate, 13-1/2 x 30		Qty 1	Scale 1:5	Units inch	Projection 
Created by J. Clements III		Approved by -		Document type Detail drawing	Status Draft
Legal owner J. Clements III CEB Project	Title Dirt Keeper Plate L-H8 OSE CEB Press 6 (a-z Build 1.0)			Identification number OSEP6-P6-57	Sheet 67/94
				Rev A	

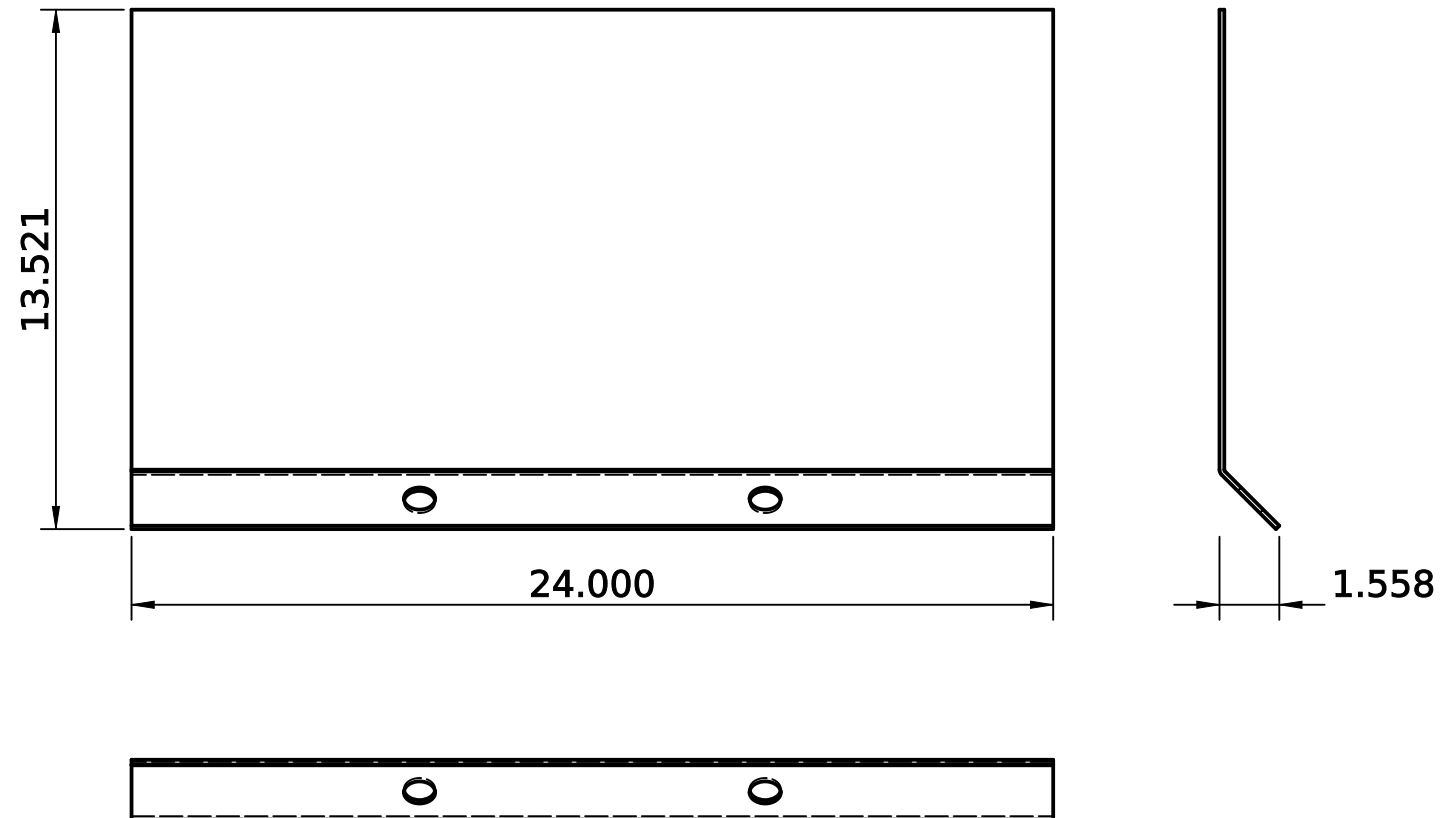

- NOTES:
1. ALL DIMENSIONS IN INCHES. TOLERANCE $\pm 1/32$ UNLESS NOTED.
 2. BREAK SHARP EDGES, REMOVE BURRS.
 3. MATERIAL PER TITLE BLOCK. FILLET WELDS $1/4$ UNLESS NOTED.
 4. OSE 01-152-00-0, IN SIDE SOIL DEFLECTOR ASSEMBLY. USED IN: HOPPER 2.
 5. BENT FROM $1/8$ " SHEET: FLAT BLANK 23×14.056 PER OSE DXF L-H5.
 6. GEOMETRY FROM OSE FULL_ASSEMBLY.STP (CEB PRESS 6); TITLE BLOCKS OF OSE'S 2D SET SAY 'CEB PRESS 5'.

Material 1/8" sheet, bent, 23.0 x 14.1		Qty 2	Scale 1:5	Units inch	Projection 	
Created by J. Clements III		Approved by -	Document type Detail drawing		Status Draft	
Legal owner J. Clements III CEB Project	Title Side Soil Deflector L-H5 OSE CEB Press 6 (a-z Build 1.0)			Identification number OSEP6-P6-58		Sheet 68/94
				Rev A	Date of issue 2026-10-04	

2.000

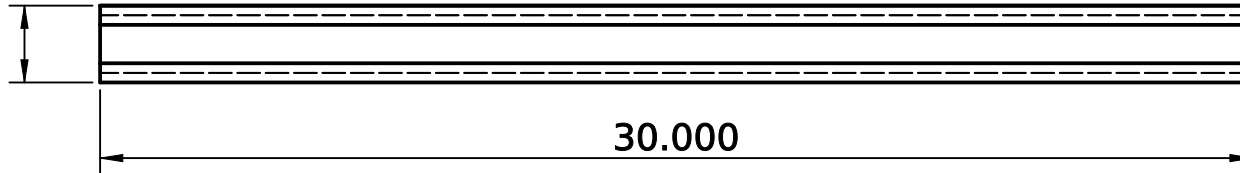


2.000



NOTES:

1. ALL DIMENSIONS IN INCHES. TOLERANCE $\pm 1/32$ UNLESS NOTED.
2. BREAK SHARP EDGES, REMOVE BURRS.
3. MATERIAL PER TITLE BLOCK. FILLET WELDS $1/4$ UNLESS NOTED.
4. OSE 01-186-00-0. USED IN: HOPPER 2.
5. GEOMETRY FROM OSE FULL_ASSEMBLY.STP (CEB PRESS 6); TITLE BLOCKS OF OSE'S 2D SET SAY 'CEB PRESS 5'.


Material 3/16 X 2 SQUARE TUBE X 38		Qty 2	Scale 1:5	Units inch	Projection 	
Created by J. Clements III		Approved by -		Document type Detail drawing	Status Draft	
Legal owner J. Clements III CEB Project	Title Grate Support Tube OSE CEB Press 6 (a-z Build 1.0)			Identification number OSEP6-P6-59		Sheet 69/94
				Rev A	Date of issue 2026-10-04	

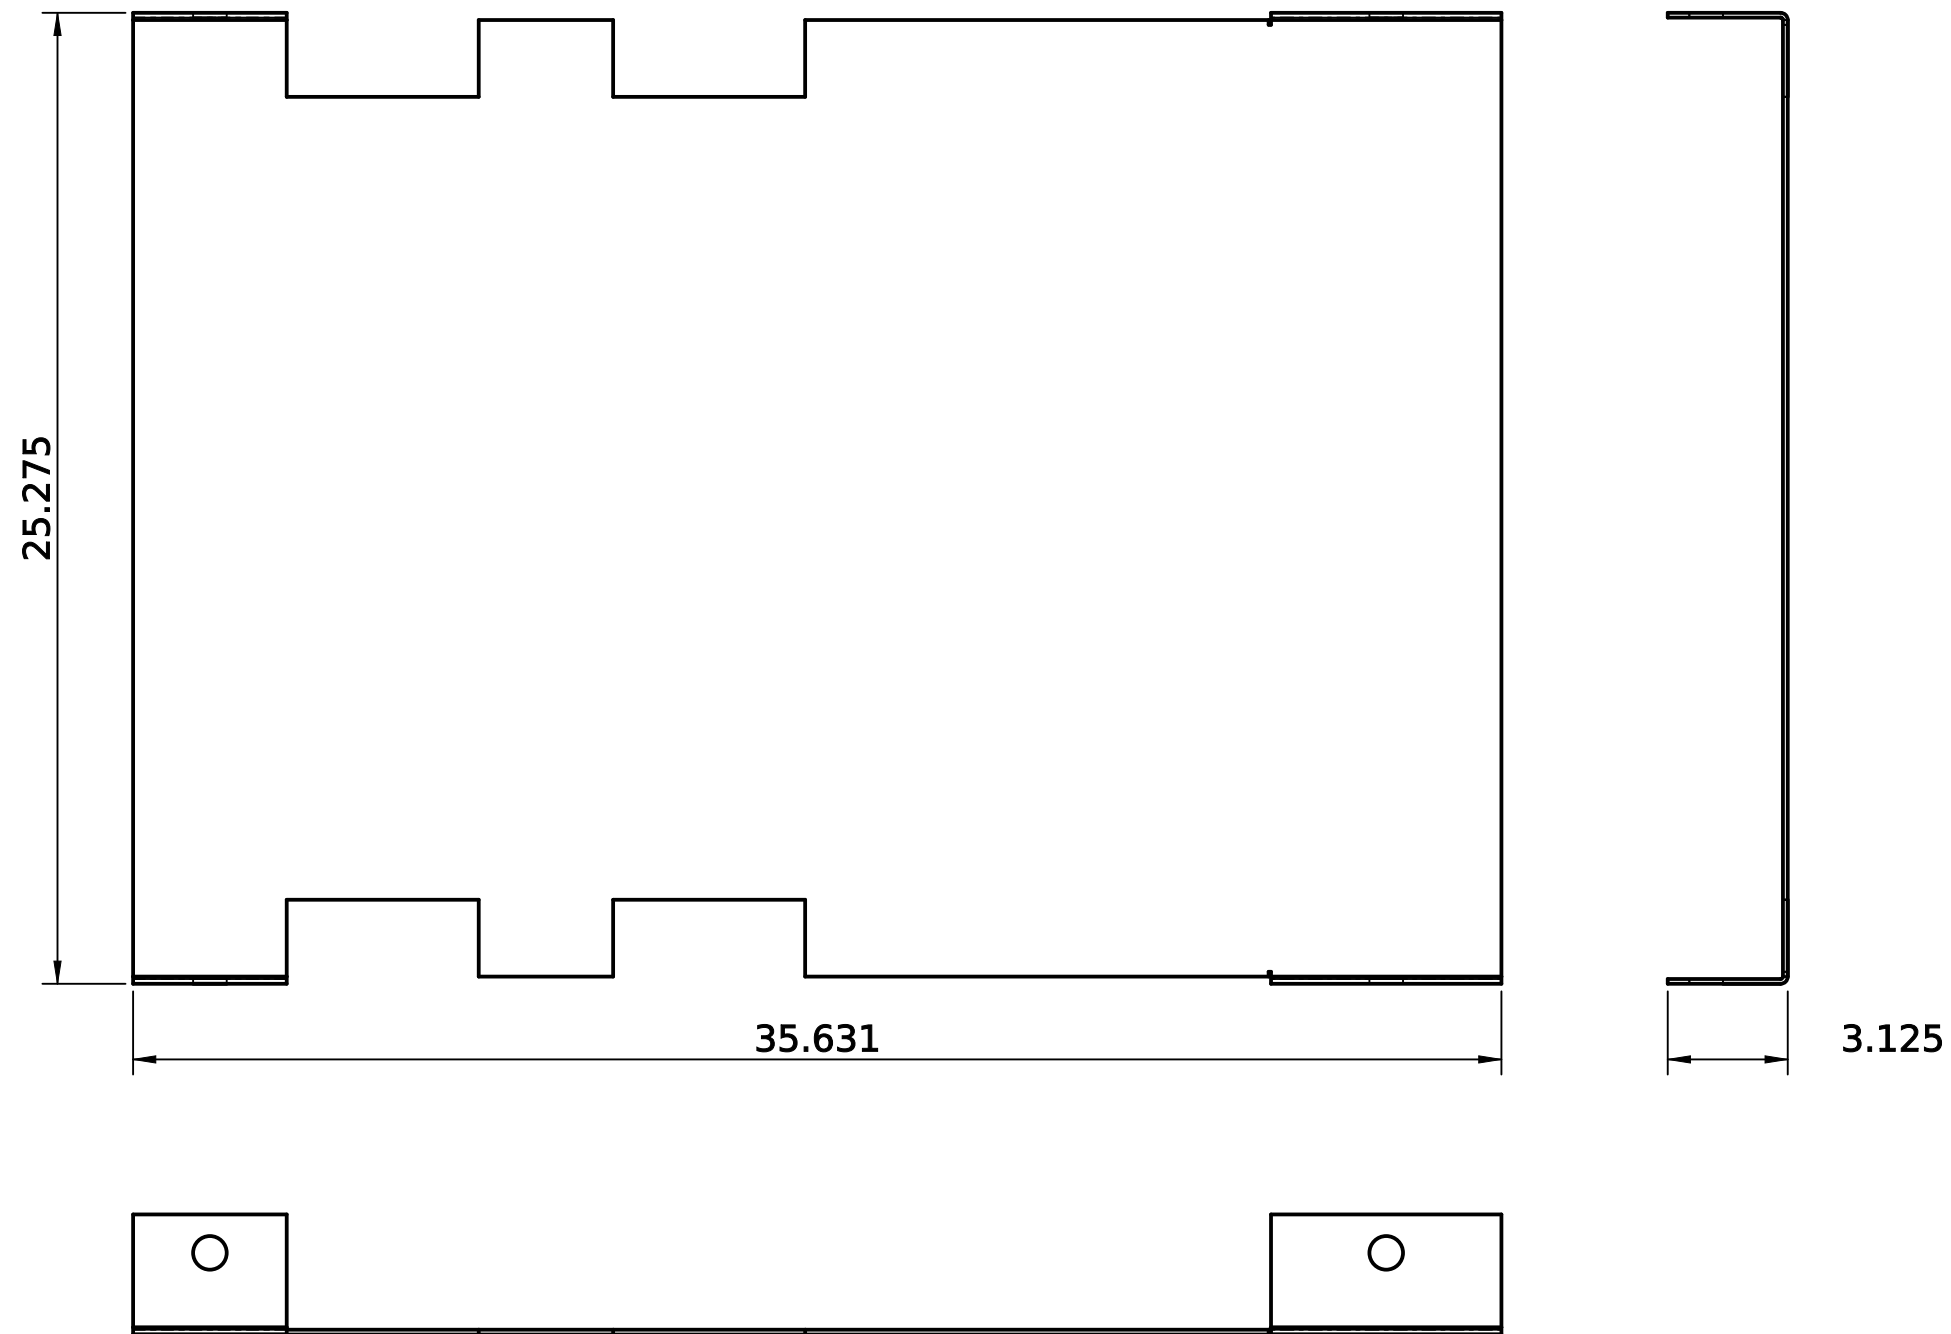

NOTES:

1. ALL DIMENSIONS IN INCHES. TOLERANCE $\pm 1/32$ UNLESS NOTED.
2. BREAK SHARP EDGES, REMOVE BURRS.
3. MATERIAL PER TITLE BLOCK. FILLET WELDS $1/4$ UNLESS NOTED.
4. OSE 01-244-00-1, IN GUARD ASSEMBLY. USED IN: HOPPER 1.
5. BENT FROM $1/8$ " SHEET: FLAT BLANK 35.631 X 31.101 PER OSE DXF L-H12.
6. GEOMETRY FROM OSE FULL_ASSEMBLY.STP (CEB PRESS 6); TITLE BLOCKS OF OSE'S 2D SET SAY 'CEB PRESS 5'.

Material 1/8" sheet, bent, 35.6 x 31.1		Qty 1	Scale 1:5	Units inch	Projection 
Created by J. Clements III		Approved by -		Document type Detail drawing	Status Draft
Legal owner J. Clements III CEB Project		Title Guard L-H12 OSE CEB Press 6 (a-z Build 1.0)			Identification number OSEP6-P6-60
					Rev A
					Date of issue 2026-10-04
					Sheet 70/94

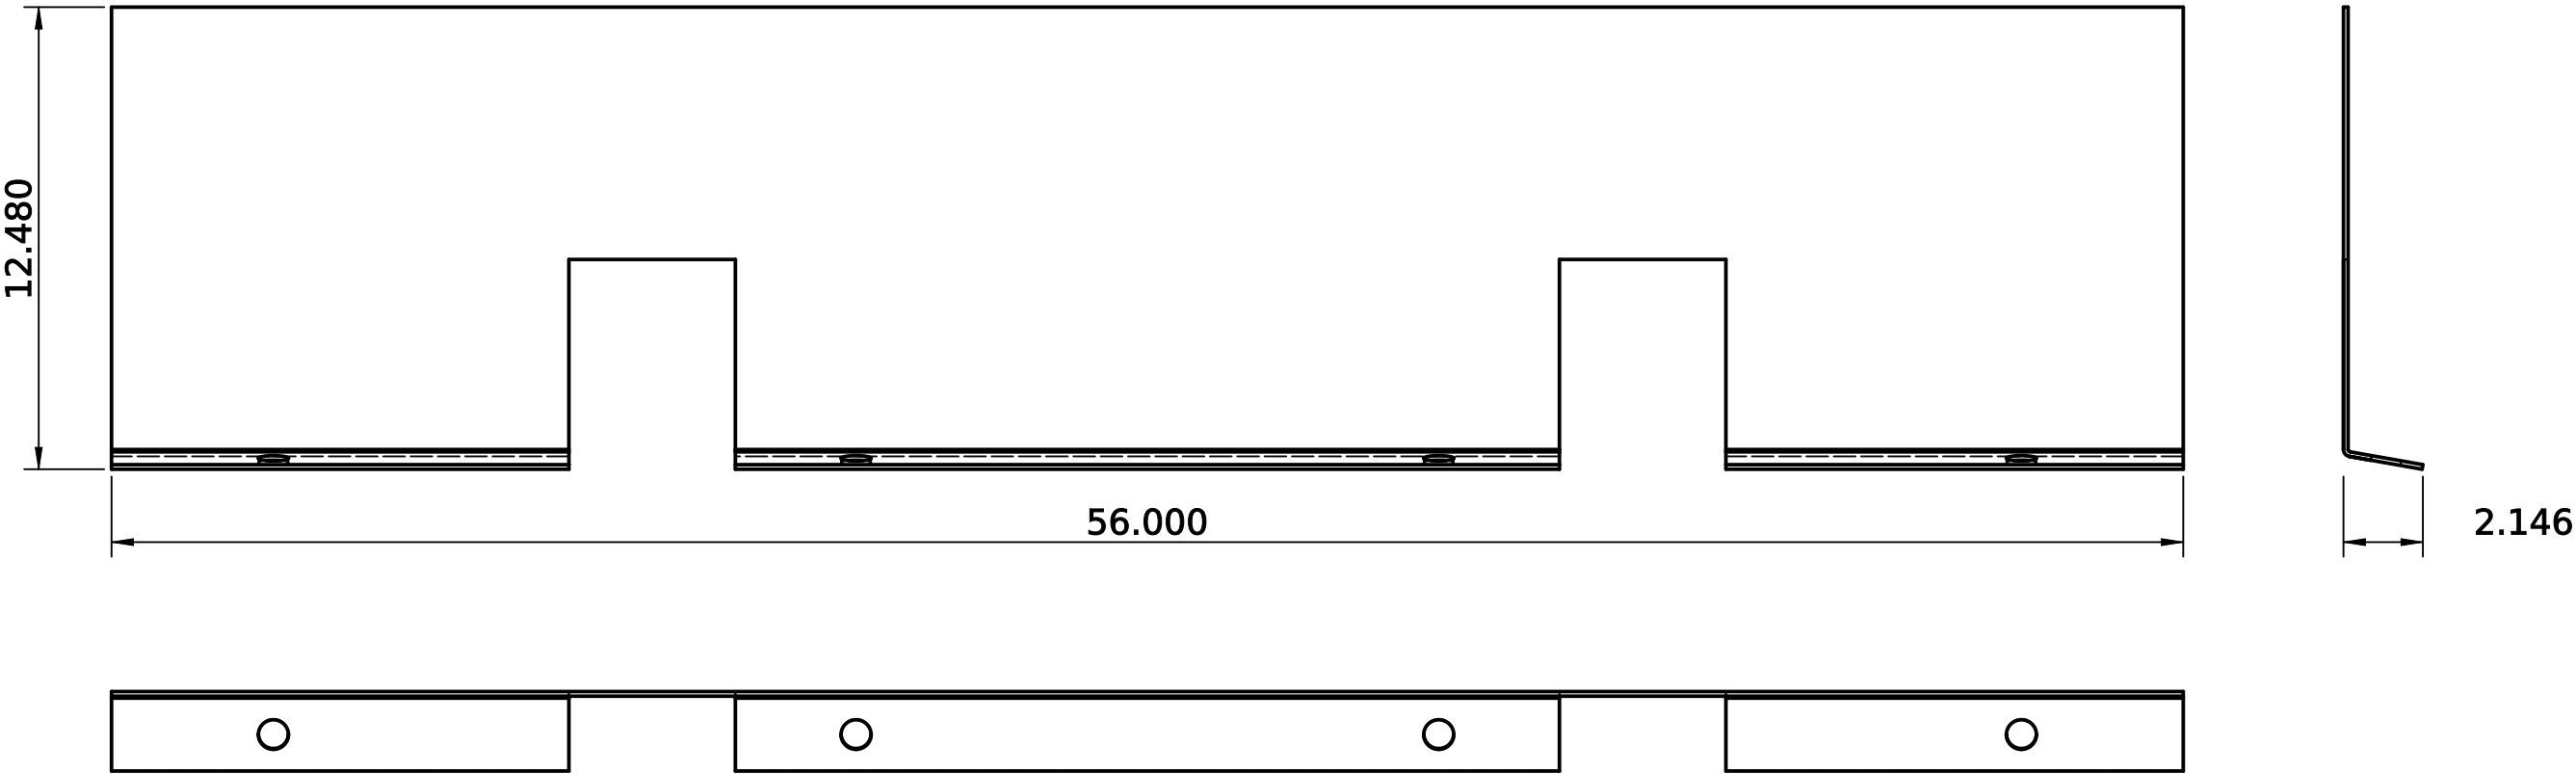

NOTES:

1. ALL DIMENSIONS IN INCHES. TOLERANCE ±1/32 UNLESS NOTED.

2. BREAK SHARP EDGES, REMOVE BURRS.


3. MATERIAL PER TITLE BLOCK. FILLET WELDS 1/4 UNLESS NOTED.

4. OSE 01-257-00-0, IN FRONT SOIL DEFLECTOR ASSEMBLY. USED IN: HOPPER 1.

5. BENT FROM 1/8" SHEET: FLAT BLANK 56 X 14.092 PER OSE DXF L-H4.

6. GEOMETRY FROM OSE FULL_ASSEMBLY.STP (CEB PRESS 6); TITLE BLOCKS OF OSE'S 2D SET SAY 'CEB PRESS 5'.


Material 1/8" sheet, bent, 56.0 x 14.1		Qty 1	Scale 1:5	Units inch	Projection 	
Created by J. Clements III		Approved by -		Document type Detail drawing	Status Draft	
Legal owner J. Clements III CEB Project	Title Front Soil Deflector L-H4 OSE CEB Press 6 (a-z Build 1.0)			Identification number OSEP6-P6-61		Sheet 71/94
				Rev A	Date of issue 2026-10-04	

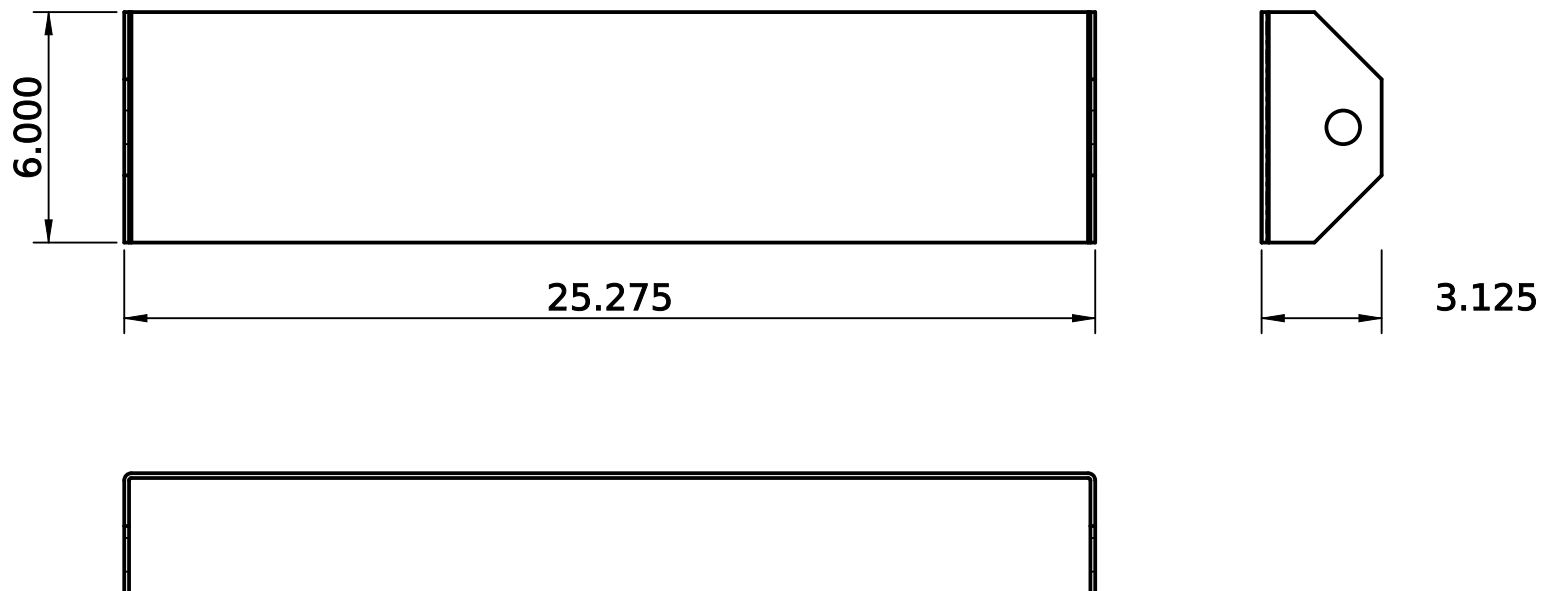

NOTES:

1. ALL DIMENSIONS IN INCHES. TOLERANCE $\pm 1/32$ UNLESS NOTED.
2. BREAK SHARP EDGES, REMOVE BURRS.
3. MATERIAL PER TITLE BLOCK. FILLET WELDS $1/4$ UNLESS NOTED.
4. OSE 01-275-00-0, IN GUARD ASSEMBLY. USED IN: HOPPER 1.
5. BENT FROM $1/8$ " SHEET: FLAT BLANK 31.101 X 6 PER OSE DXF L-H10.
6. GEOMETRY FROM OSE FULL_ASSEMBLY.STP (CEB PRESS 6); TITLE BLOCKS OF OSE'S 2D SET SAY 'CEB PRESS 5'.


Material 1/8" sheet, bent, 31.1 x 6.0		Qty 1	Scale 1:5	Units inch	Projection 	
Created by J. Clements III		Approved by -		Document type Detail drawing	Status Draft	
Legal owner J. Clements III CEB Project	Title Guard L-H10 OSE CEB Press 6 (a-z Build 1.0)			Identification number OSEP6-P6-62		Sheet 72/94
				Rev A	Date of issue 2026-10-04	

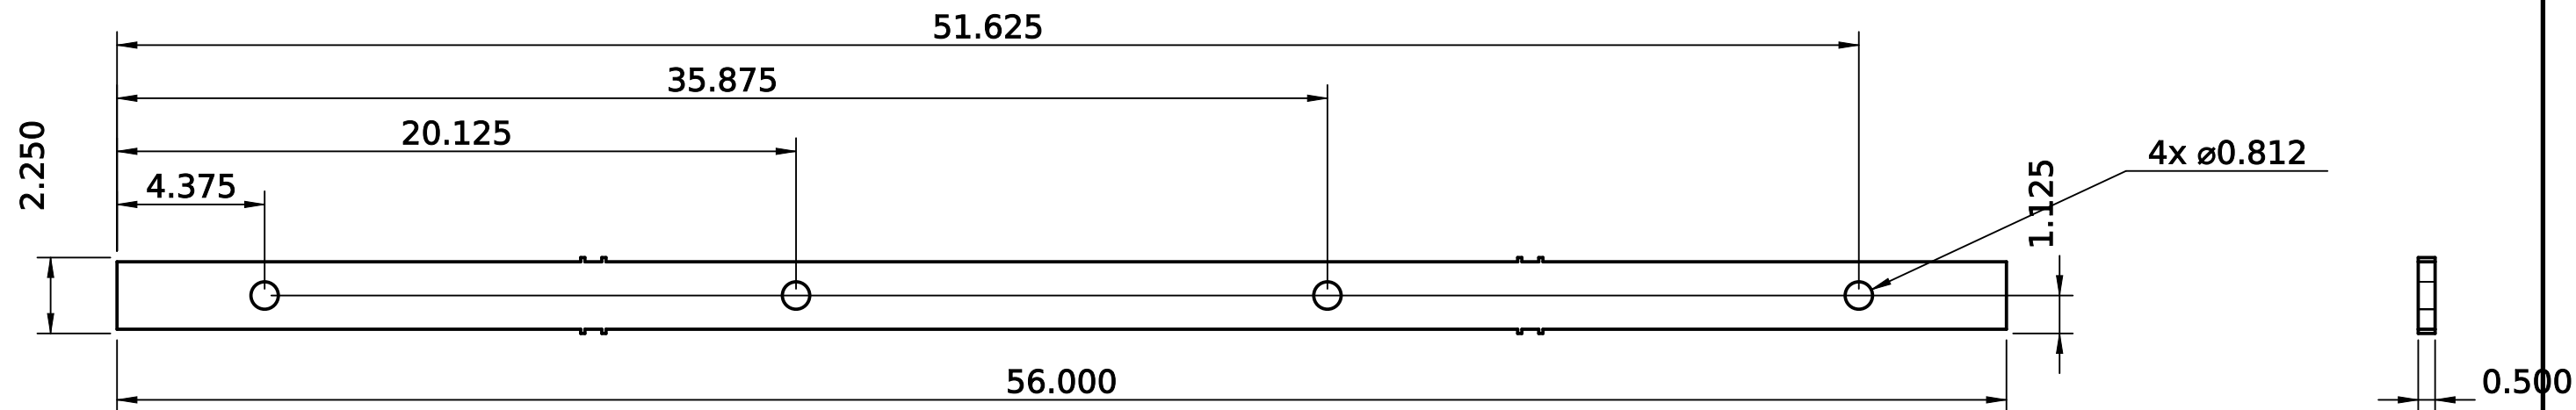

NOTES:

1. ALL DIMENSIONS IN INCHES. TOLERANCE $\pm 1/32$ UNLESS NOTED.
2. BREAK SHARP EDGES, REMOVE BURRS.
3. MATERIAL PER TITLE BLOCK. FILLET WELDS $1/4$ UNLESS NOTED.
4. OSE 01-068-00-0, IN GRATE ASSEMBLY. USED IN: GRATE 2.
5. DXF LIBRARY L-G2: 56 X 2-5/16 X $1/2$ - MODEL 56 X 2-1/4 X $1/2$; CHECK.
6. OSE 2015 WELDMENT REDRAW MAKES IT FROM $1/4$ X 2 X 2 HR FLAT X 72 PER DETAIL INSTEAD.
7. GEOMETRY FROM OSE FULL_ASSEMBLY.STP (CEB PRESS 6); TITLE BLOCKS OF OSE'S 2D SET SAY 'CEB PRESS 5'.

Material 1/2" plate, 2-1/4 x 56		Qty 2	Scale 1:5	Units inch	Projection 	
Created by J. Clements III		Approved by -		Document type Detail drawing	Status Draft	
Legal owner J. Clements III CEB Project	Title Grate Side L-G2 OSE CEB Press 6 (a-z Build 1.0)			Identification number OSEP6-P6-63		Sheet 73/94
				Rev A	Date of issue 2026-10-04	

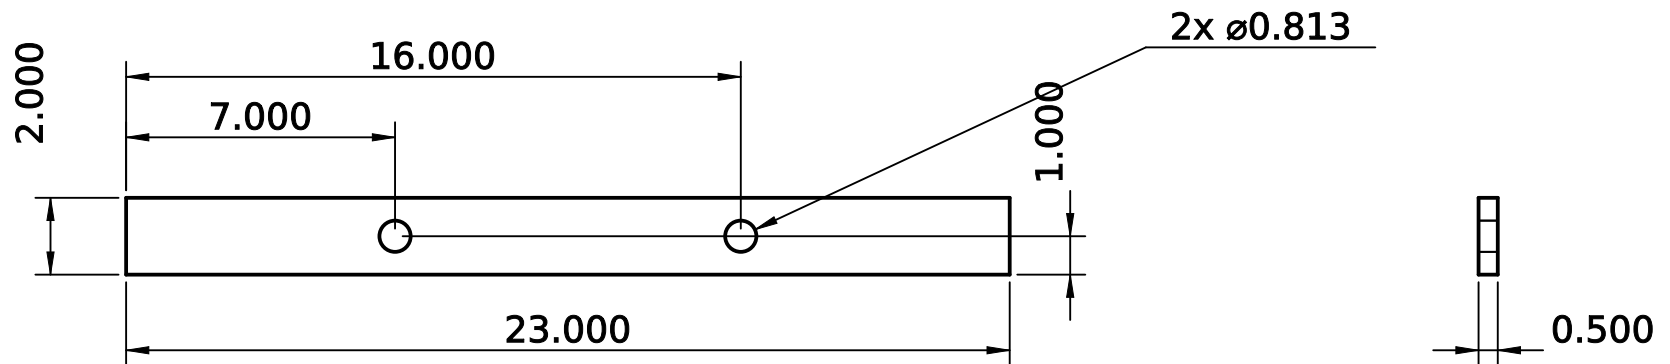


NOTES:

1. ALL DIMENSIONS IN INCHES. TOLERANCE $\pm 1/32$ UNLESS NOTED.
2. BREAK SHARP EDGES, REMOVE BURRS.
3. MATERIAL PER TITLE BLOCK. FILLET WELDS 1/4 UNLESS NOTED.
4. OSE 01-069-00-0 / WELDMENT 001-0069, IN GRATE ASSEMBLY. USED IN: GRATE 2.
5. DXF LIBRARY L-G1: 23.631 X 2 X 1/2 - MODEL 23 X 2 X 1/2; CHECK.
6. OSE 2015 WELDMENT REDRAW MAKES IT FROM ANGLE, STEEL, L2X2X1/4 INSTEAD.
7. GEOMETRY FROM OSE FULL_ASSEMBLY.STP (CEB PRESS 6); TITLE BLOCKS OF OSE'S 2D SET SAY 'CEB PRESS 5'.

Material 1/2" plate, 2 x 23		Qty 2	Scale 1:5	Units inch	Projection 	
Created by J. Clements III		Approved by -	Document type Detail drawing		Status Draft	
Legal owner J. Clements III CEB Project	Title Grate Angle L-G1 OSE CEB Press 6 (a-z Build 1.0)			Identification number OSEP6-P6-64		Sheet 74/94
				Rev A	Date of issue 2026-10-04	

2.000

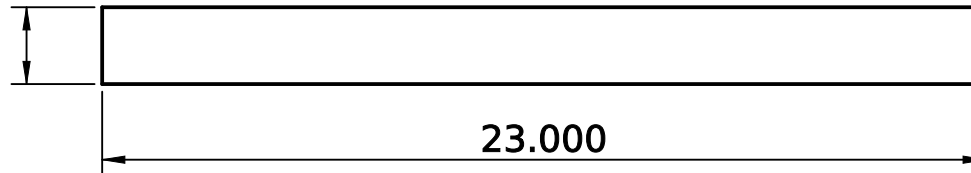

23.000




0.250

NOTES:

1. ALL DIMENSIONS IN INCHES. TOLERANCE $\pm 1/32$ UNLESS NOTED.
2. BREAK SHARP EDGES, REMOVE BURRS.
3. MATERIAL PER TITLE BLOCK. FILLET WELDS $1/4$ UNLESS NOTED.
4. OSE 01-071-00-0 / WELDMENT 001-0071, IN GRATE ASSEMBLY. USED IN: GRATE 31.
5. GEOMETRY FROM OSE FULL_ASSEMBLY.STP (CEB PRESS 6); TITLE BLOCKS OF OSE'S 2D SET SAY 'CEB PRESS 5'.

Material ROUND BAR, RB1/2		Qty 31	Scale 1:5	Units inch	Projection 
Created by J. Clements III		Approved by -		Document type Detail drawing	Status Draft
Legal owner J. Clements III CEB Project	Title Grate Rod OSE CEB Press 6 (a-z Build 1.0)			Identification number OSEP6-P6-65	Sheet 75/94
				Rev A	


2.000

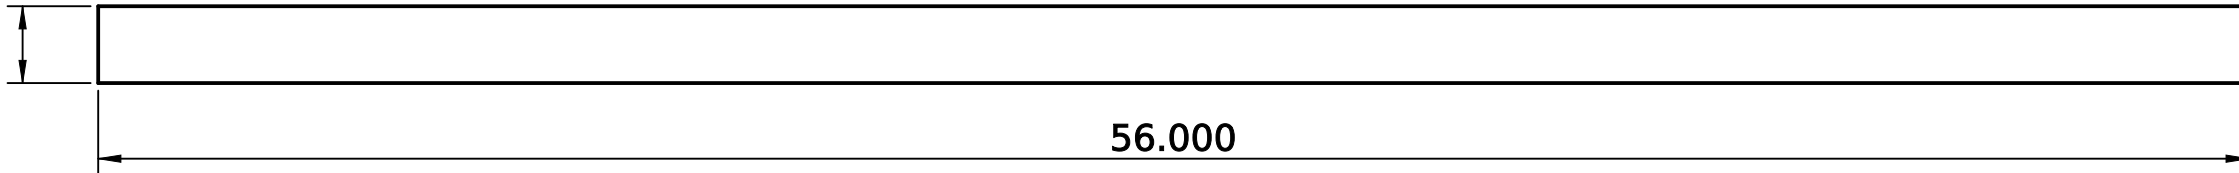

NOTES:

1. ALL DIMENSIONS IN INCHES. TOLERANCE $\pm 1/32$ UNLESS NOTED.
2. BREAK SHARP EDGES, REMOVE BURRS.
3. MATERIAL PER TITLE BLOCK. FILLET WELDS $1/4$ UNLESS NOTED.
4. OSE 01-118-00-0 / WELDMENT 001-0118, IN GRATE ASSEMBLY. USED IN: GRATE 1.
5. GEOMETRY FROM OSE FULL_ASSEMBLY.STP (CEB PRESS 6); TITLE BLOCKS OF OSE'S 2D SET SAY 'CEB PRESS 5'.


Material FLAT BAR, FB1/4X2		Qty 1	Scale 1:5	Units inch	Projection 	
Created by J. Clements III		Approved by -		Document type Detail drawing	Status Draft	
Legal owner J. Clements III CEB Project	Title Soil Grate - Cross piece OSE CEB Press 6 (a-z Build 1.0)			Identification number OSEP6-P6-66		Sheet 76/94
				Rev A	Date of issue 2026-10-04	

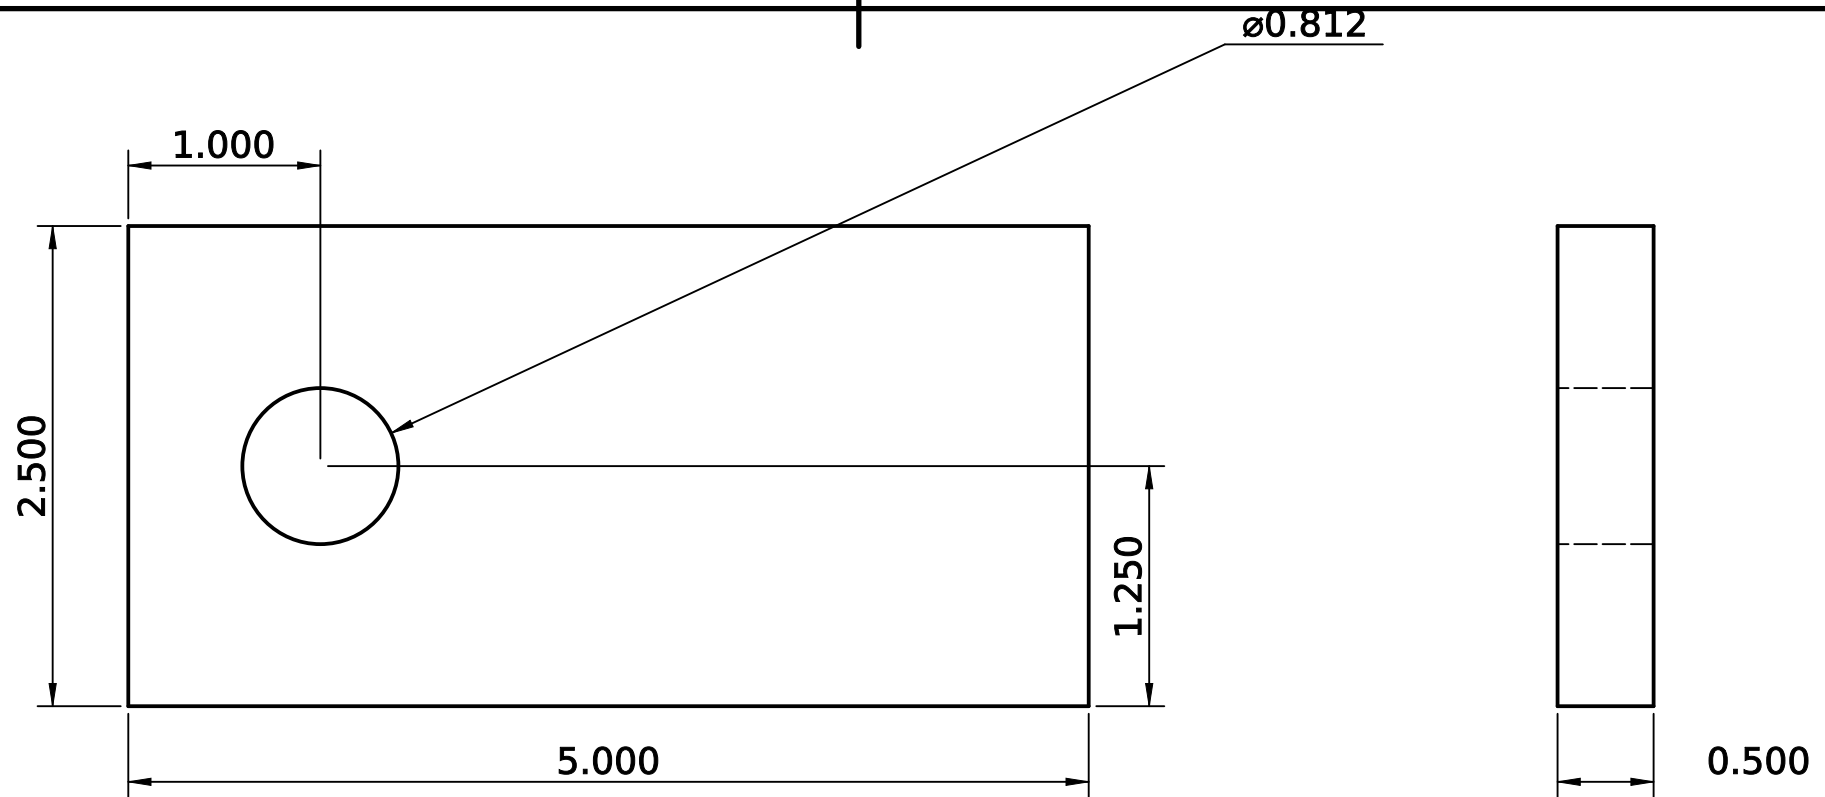

NOTES:

1. ALL DIMENSIONS IN INCHES. TOLERANCE $\pm 1/32$ UNLESS NOTED.
2. BREAK SHARP EDGES, REMOVE BURRS.
3. MATERIAL PER TITLE BLOCK. FILLET WELDS $1/4$ UNLESS NOTED.
4. OSE 01-252-00-0, IN GRATE BRACKET ASSEMBLY. USED IN: GRATE 8.
5. DXF LIBRARY L-O7: 5 X 2-1/2 X 1/2 - MATCHES THE MODEL.
6. GEOMETRY FROM OSE FULL_ASSEMBLY.STP (CEB PRESS 6); TITLE BLOCKS OF OSE'S 2D SET SAY 'CEB PRESS 5'.

Material 1/2" plate, 2-1/2 x 5		Qty 8	Scale 1:1	Units inch	Projection 	
Created by J. Clements III		Approved by -	Document type Detail drawing		Status Draft	
Legal owner J. Clements III CEB Project	Title Grate Bracket Plate L-O7 OSE CEB Press 6 (a-z Build 1.0)			Identification number OSEP6-P6-67		Sheet 77/94
				Rev A	Date of issue 2026-10-04	


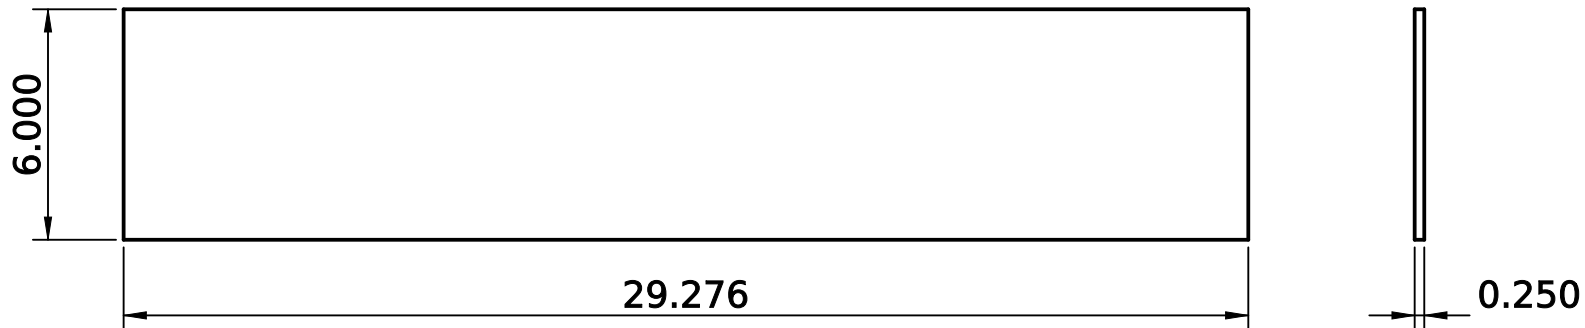


NOTES:

1. ALL DIMENSIONS IN INCHES. TOLERANCE $\pm 1/32$ UNLESS NOTED.
2. BREAK SHARP EDGES, REMOVE BURRS.
3. MATERIAL PER TITLE BLOCK. FILLET WELDS $1/4$ UNLESS NOTED.
4. OSE 01-254-00-0, IN REAR GRATE HINGE ASSEMBLY. USED IN: GRATE 1.
5. DXF LIBRARY L-Q13: 29.276 X 6 X $1/4$ - MATCHES THE MODEL.
6. GEOMETRY FROM OSE FULL_ASSEMBLY.STP (CEB PRESS 6); TITLE BLOCKS OF OSE'S 2D SET SAY 'CEB PRESS 5'.

Material 1/4" plate, 6 x 29.276		Qty 1	Scale 1:5	Units inch	Projection 	
Created by J. Clements III		Approved by -		Document type Detail drawing	Status Draft	
Legal owner J. Clements III CEB Project	Title Rear Grate Hinge Plate L-Q13 OSE CEB Press 6 (a-z Build 1.0)			Identification number OSEP6-P6-68		Sheet 78/94
				Rev A	Date of issue 2026-10-04	


2.500

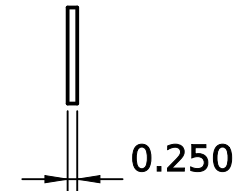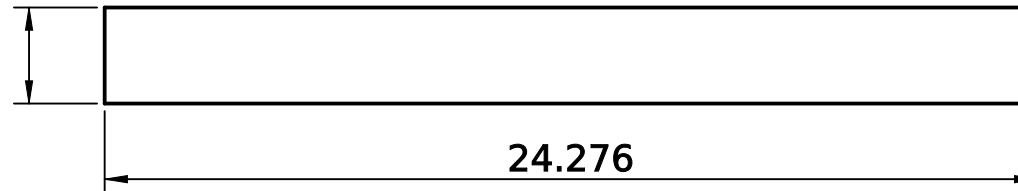

NOTES:

1. ALL DIMENSIONS IN INCHES. TOLERANCE $\pm 1/32$ UNLESS NOTED.
2. BREAK SHARP EDGES, REMOVE BURRS.
3. MATERIAL PER TITLE BLOCK. FILLET WELDS 1/4 UNLESS NOTED.
4. OSE 01-255-00-0, IN REAR GRATE HINGE ASSEMBLY. USED IN: GRATE 1.
5. DXF LIBRARY L-Q14: 24.276 X 2-1/2 X 1/4 - MATCHES THE MODEL.
6. GEOMETRY FROM OSE FULL_ASSEMBLY.STP (CEB PRESS 6); TITLE BLOCKS OF OSE'S 2D SET SAY 'CEB PRESS 5'.


Material 1/4" plate, 2-1/2 x 24.276		Qty 1	Scale 1:5	Units inch	Projection 	
Created by J. Clements III		Approved by -		Document type Detail drawing	Status Draft	
Legal owner J. Clements III CEB Project	Title Rear Grate Hinge Plate L-Q14 OSE CEB Press 6 (a-z Build 1.0)			Identification number OSEP6-P6-69		Sheet 79/94
				Rev A	Date of issue 2026-10-04	

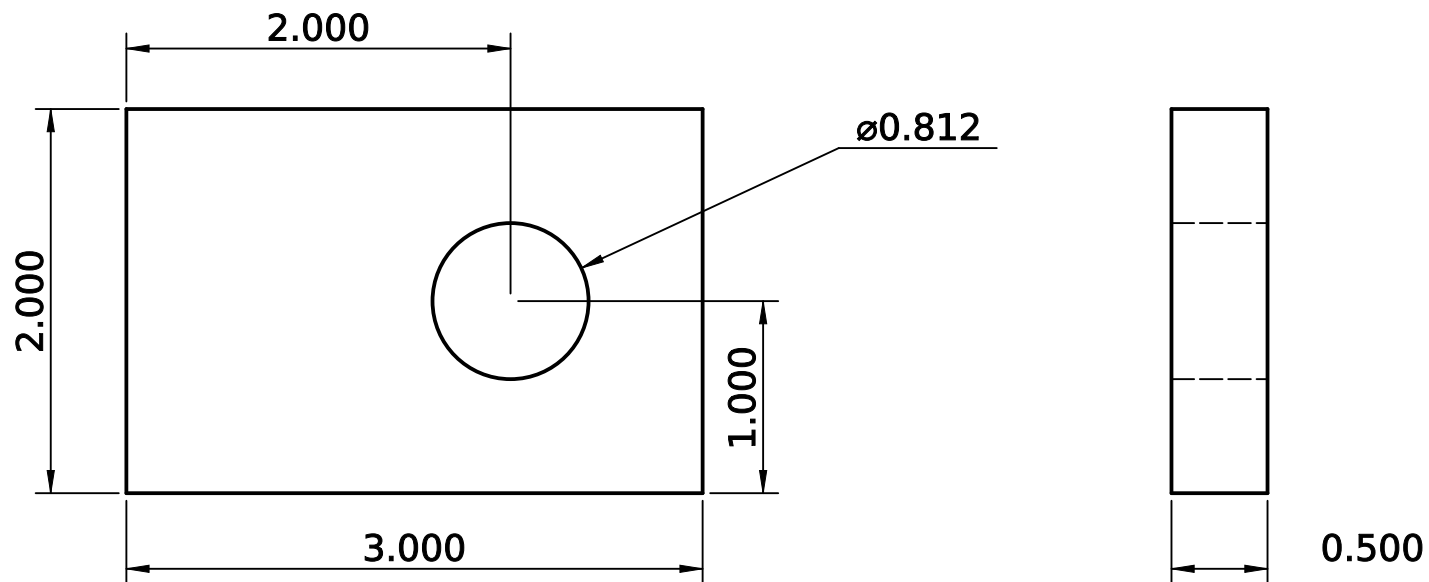

NOTES:

1. ALL DIMENSIONS IN INCHES. TOLERANCE $\pm 1/32$ UNLESS NOTED.
2. BREAK SHARP EDGES, REMOVE BURRS.
3. MATERIAL PER TITLE BLOCK. FILLET WELDS 1/4 UNLESS NOTED.
4. OSE 01-261-00-0, IN GRATE ASSEMBLY. USED IN: GRATE 4.
5. DXF LIBRARY L-G3: 3 X 2 X 1/2 - MATCHES THE MODEL.
6. GEOMETRY FROM OSE FULL_ASSEMBLY.STP (CEB PRESS 6); TITLE BLOCKS OF OSE'S 2D SET SAY 'CEB PRESS 5'.


Material 1/2" plate, 2 x 3		Qty 4	Scale 1:1	Units inch	Projection 
Created by J. Clements III		Approved by -		Document type Detail drawing	Status Draft
Legal owner J. Clements III CEB Project	Title Grate Plate L-G3 OSE CEB Press 6 (a-z Build 1.0)			Identification number OSEP6-P6-70	Sheet 80/94
				Rev A	

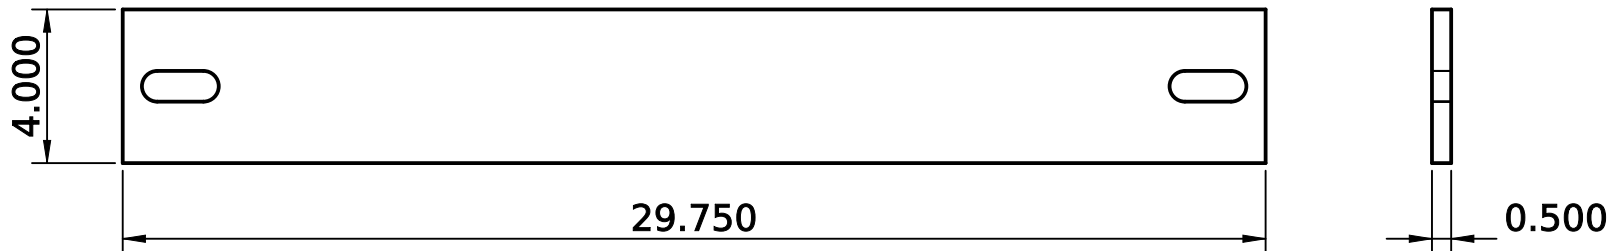

NOTES:

1. ALL DIMENSIONS IN INCHES. TOLERANCE $\pm 1/32$ UNLESS NOTED.
2. BREAK SHARP EDGES, REMOVE BURRS.
3. MATERIAL PER TITLE BLOCK. FILLET WELDS $1/4$ UNLESS NOTED.
4. OSE 01-042-00-0 / WELDMENT 001-0042, IN SHAKER FRAME ASSEMBLY. USED IN:
SOIL SHAKER 1.
5. DXF LIBRARY L-O2: $29-3/4 \times 4 \times 1/2$ - MATCHES THE MODEL.
6. OSE 2015 WELDMENT REDRAW MAKES IT FROM ANGLE, $L4 \times 4 \times 1/2$, STEEL INSTEAD.
7. GEOMETRY FROM OSE FULL_ASSEMBLY.STP (CEB PRESS 6); TITLE BLOCKS OF OSE'S 2D
SET SAY 'CEB PRESS 5'.


Material 1/2" plate, 4 x 29-3/4		Qty 1	Scale 1:5	Units inch	Projection 	
Created by J. Clements III		Approved by -		Document type Detail drawing	Status Draft	
Legal owner J. Clements III CEB Project	Title Shaker Mount Plate L-O2 OSE CEB Press 6 (a-z Build 1.0)			Identification number OSEP6-P6-71		Sheet 81/94
				Rev A	Date of issue 2026-10-04	

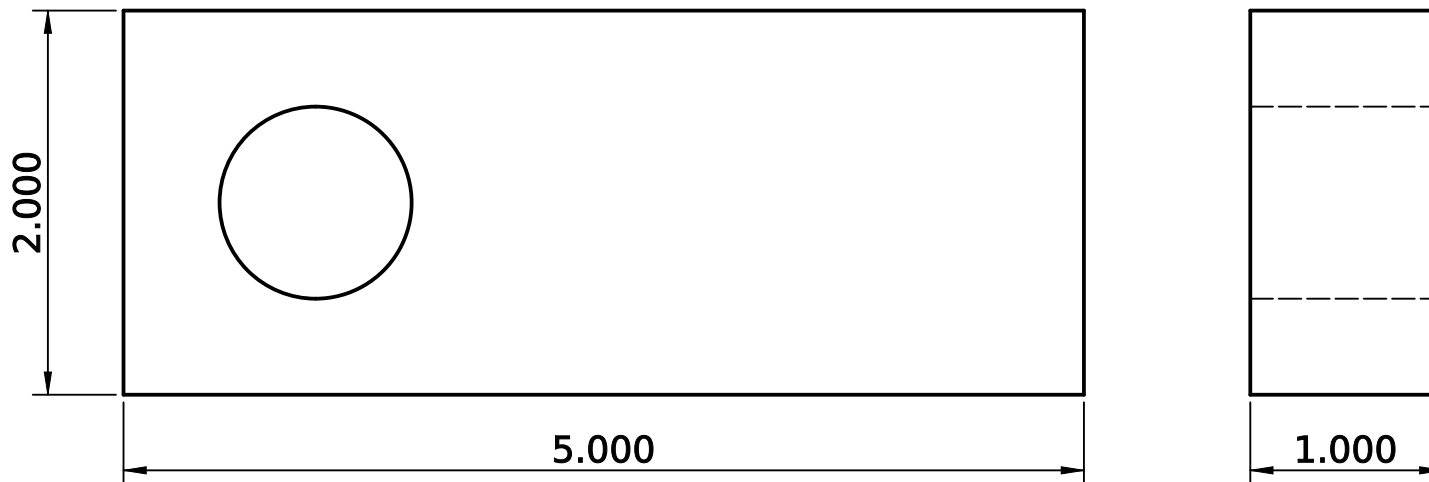

NOTES:

1. ALL DIMENSIONS IN INCHES. TOLERANCE $\pm 1/32$ UNLESS NOTED.
2. BREAK SHARP EDGES, REMOVE BURRS.
3. MATERIAL PER TITLE BLOCK. FILLET WELDS $1/4$ UNLESS NOTED.
4. OSE 01-044-00-0, IN SHAKER WEIGHT ASSEMBLY. USED IN: SOIL SHAKER 1.
5. GEOMETRY FROM OSE FULL_ASSEMBLY.STP (CEB PRESS 6); TITLE BLOCKS OF OSE'S 2D SET SAY 'CEB PRESS 5'.



Material 1 X 2 FLAT X 5		Qty 1	Scale 1:1	Units inch	Projection 
Created by J. Clements III		Approved by -		Document type Detail drawing	Status Draft
Legal owner J. Clements III CEB Project	Title Soil Shaker - Hammer OSE CEB Press 6 (a-z Build 1.0)			Identification number OSEP6-P6-72	Sheet 82/94
				Rev A	

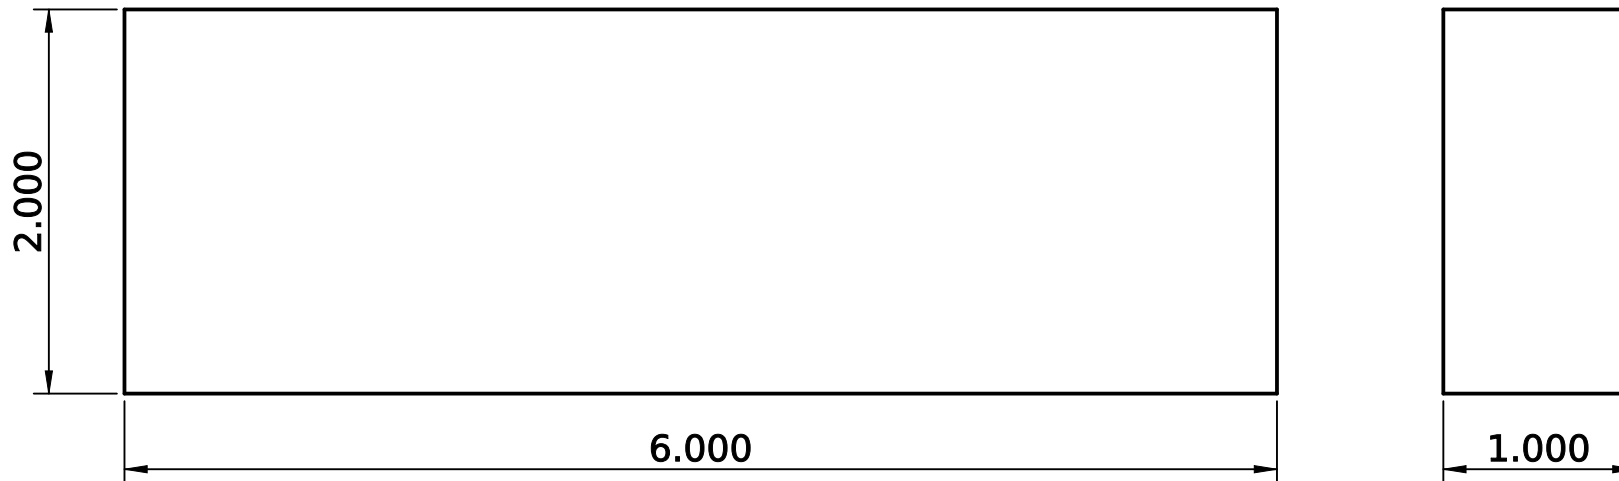

NOTES:

1. ALL DIMENSIONS IN INCHES. TOLERANCE $\pm 1/32$ UNLESS NOTED.
2. BREAK SHARP EDGES, REMOVE BURRS.
3. MATERIAL PER TITLE BLOCK. FILLET WELDS $1/4$ UNLESS NOTED.
4. OSE 01-045-00-0 / WELDMENT 001-0045, IN SHAKER WEIGHT ASSEMBLY. USED IN:
SOIL SHAKER 1.
5. GEOMETRY FROM OSE FULL_ASSEMBLY.STP (CEB PRESS 6); TITLE BLOCKS OF OSE'S 2D
SET SAY 'CEB PRESS 5'.


Material FLAT BAR, FB1X2		Qty 1	Scale 1:1	Units inch	Projection 	
Created by J. Clements III		Approved by -		Document type Detail drawing	Status Draft	
Legal owner J. Clements III CEB Project	Title Soil Shaker - Hammer OSE CEB Press 6 (a-z Build 1.0)			Identification number OSEP6-P6-73		Sheet 83/94
				Rev A	Date of issue 2026-10-04	

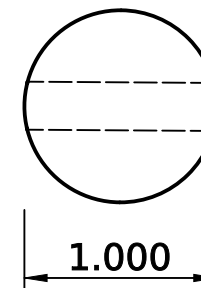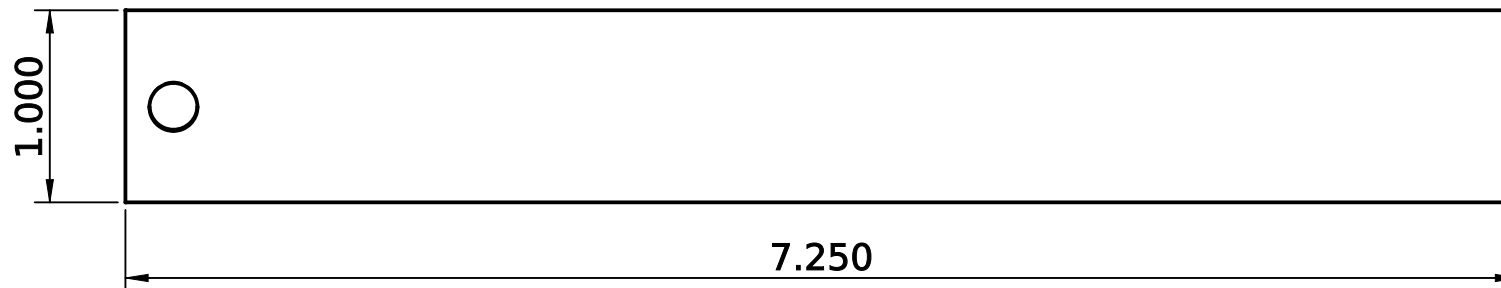

NOTES:

1. ALL DIMENSIONS IN INCHES. TOLERANCE $\pm 1/32$ UNLESS NOTED.
2. BREAK SHARP EDGES, REMOVE BURRS.
3. MATERIAL PER TITLE BLOCK. FILLET WELDS $1/4$ UNLESS NOTED.
4. OSE 01-046-00-0 / WELDMENT 001-0046, IN SHAKER WEIGHT ASSEMBLY. USED IN: SOIL SHAKER 1.
5. GEOMETRY FROM OSE FULL_ASSEMBLY.STP (CEB PRESS 6); TITLE BLOCKS OF OSE'S 2D SET SAY 'CEB PRESS 5'.


Material ROUND BAR, RB1		Qty 1	Scale 1:1	Units inch	Projection 	
Created by J. Clements III		Approved by -		Document type Detail drawing	Status Draft	
Legal owner J. Clements III CEB Project	Title Shaker Shaft OSE CEB Press 6 (a-z Build 1.0)			Identification number OSEP6-P6-74		Sheet 84/94
				Rev A	Date of issue 2026-10-04	

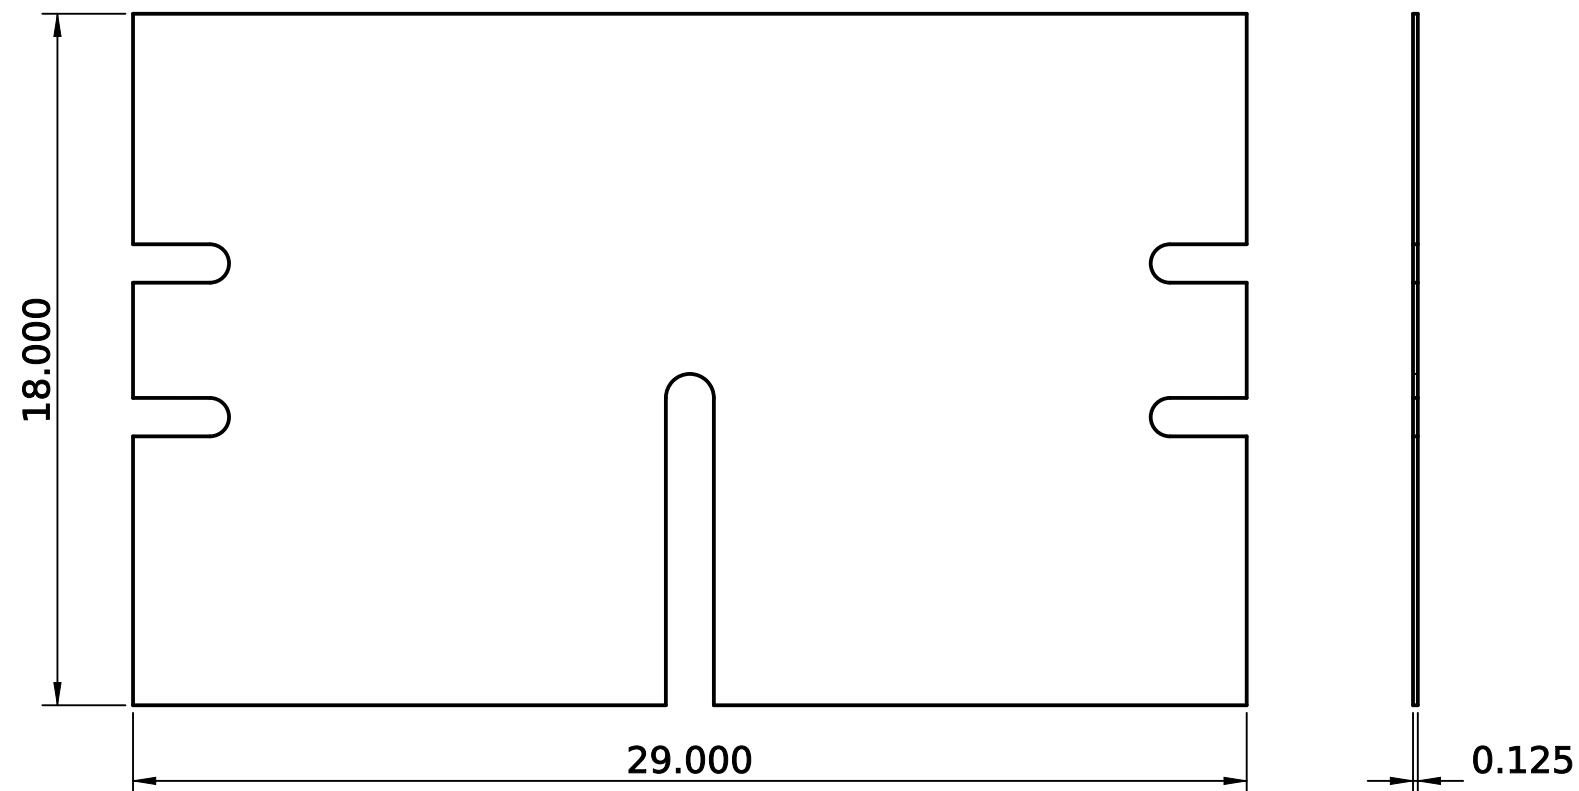

NOTES:

1. ALL DIMENSIONS IN INCHES. TOLERANCE $\pm 1/32$ UNLESS NOTED.
2. BREAK SHARP EDGES, REMOVE BURRS.
3. MATERIAL PER TITLE BLOCK. FILLET WELDS $1/4$ UNLESS NOTED.
4. OSE 01-074-00-0, IN SHAKER ASSEMBLY. USED IN: SOIL SHAKER 1.
5. DXF LIBRARY L-H6: 29 X 18 X $1/8$ - MATCHES THE MODEL.
6. GEOMETRY FROM OSE FULL_ASSEMBLY.STP (CEB PRESS 6); TITLE BLOCKS OF OSE'S 2D SET SAY 'CEB PRESS 5'.


Material 1/8" plate, 18 x 29		Qty 1	Scale 1:5	Units inch	Projection 	
Created by J. Clements III		Approved by -		Document type Detail drawing	Status Draft	
Legal owner J. Clements III CEB Project	Title Shaker Motor Guard L-H6 OSE CEB Press 6 (a-z Build 1.0)			Identification number OSEP6-P6-75		Sheet 85/94
				Rev A	Date of issue 2026-10-04	

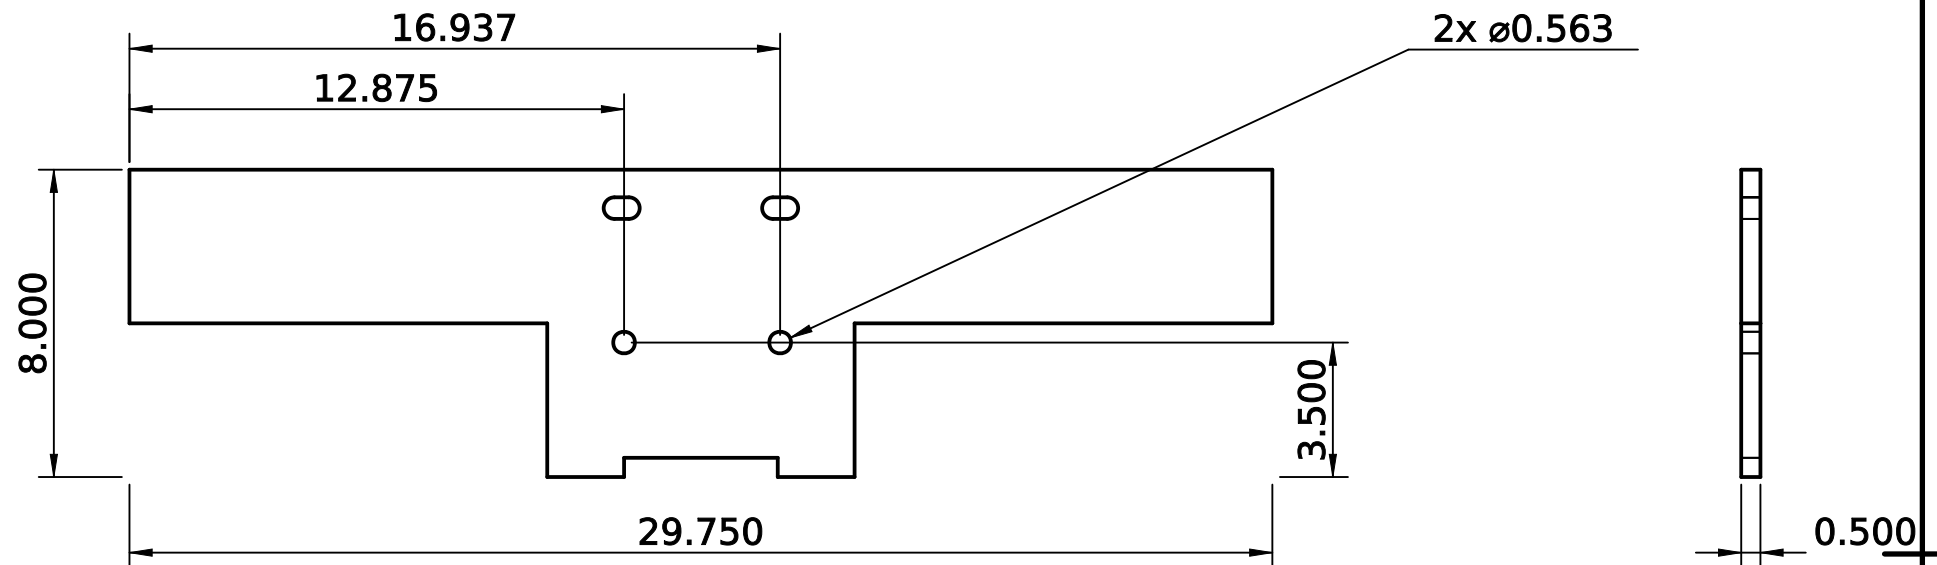

NOTES:

1. ALL DIMENSIONS IN INCHES. TOLERANCE $\pm 1/32$ UNLESS NOTED.
2. BREAK SHARP EDGES, REMOVE BURRS.
3. MATERIAL PER TITLE BLOCK. FILLET WELDS $1/4$ UNLESS NOTED.
4. OSE 01-144-00-0, IN SHAKER FRAME ASSEMBLY. USED IN: SOIL SHAKER 1.
5. DXF LIBRARY L-O3: 29-3/4 X 8 X 1/2 - MATCHES THE MODEL.
6. GEOMETRY FROM OSE FULL_ASSEMBLY.STP (CEB PRESS 6); TITLE BLOCKS OF OSE'S 2D SET SAY 'CEB PRESS 5'.


Material 1/2" plate, 8 x 29-3/4		Qty 1	Scale 1:5	Units inch	Projection 
Created by J. Clements III		Approved by -		Document type Detail drawing	Status Draft
Legal owner J. Clements III CEB Project	Title Shaker Frame Plate L-O3 OSE CEB Press 6 (a-z Build 1.0)	Identification number OSEP6-P6-76		Sheet 86/94	
		Rev A	Date of issue 2026-10-04		

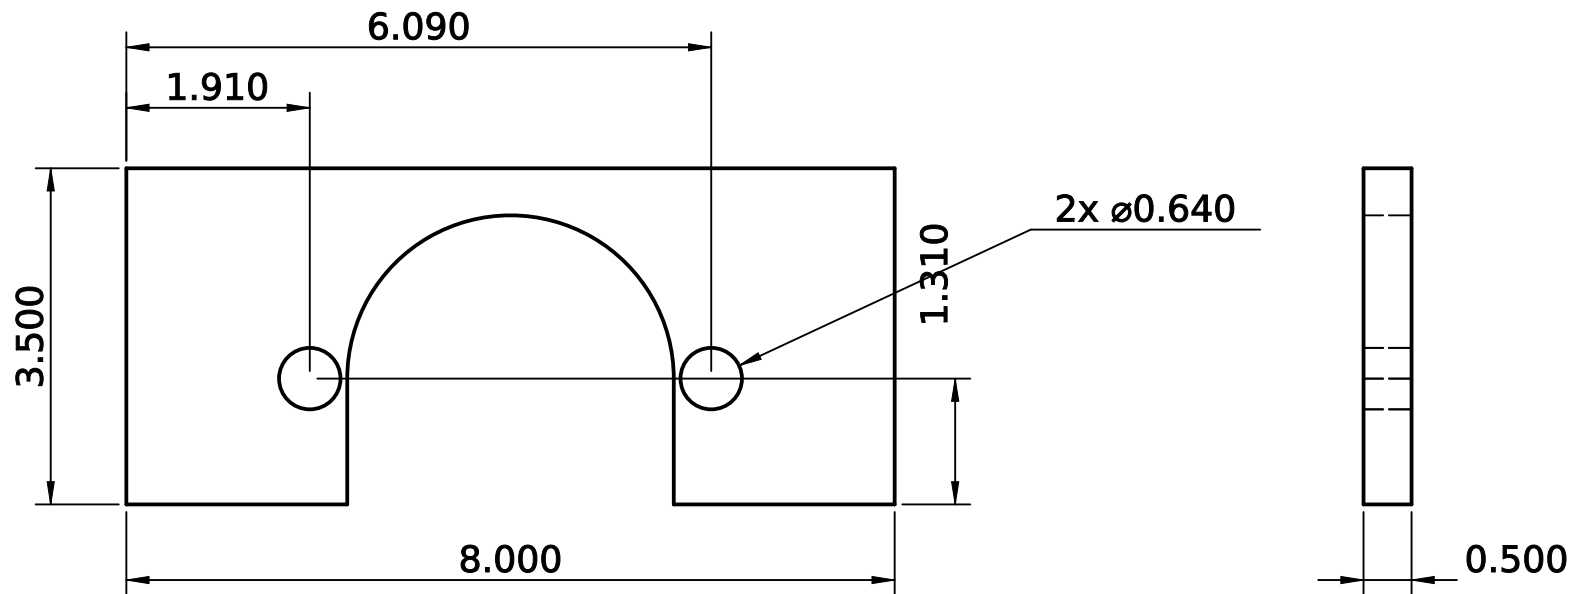

NOTES:

1. ALL DIMENSIONS IN INCHES. TOLERANCE $\pm 1/32$ UNLESS NOTED.
2. BREAK SHARP EDGES, REMOVE BURRS.
3. MATERIAL PER TITLE BLOCK. FILLET WELDS $1/4$ UNLESS NOTED.
4. OSE 01-145-00-0, IN SHAKER FRAME ASSEMBLY. USED IN: SOIL SHAKER 1.
5. DXF LIBRARY L-O4: 8 X 3-1/2 X 1/2 - MATCHES THE MODEL.
6. GEOMETRY FROM OSE FULL_ASSEMBLY.STP (CEB PRESS 6); TITLE BLOCKS OF OSE'S 2D SET SAY 'CEB PRESS 5'.


Material 1/2" plate, 3-1/2 x 8		Qty 1	Scale 1:2	Units inch	Projection 
Created by J. Clements III		Approved by -		Document type Detail drawing	Status Draft
Legal owner J. Clements III CEB Project	Title Shaker Frame Plate L-O4 OSE CEB Press 6 (a-z Build 1.0)			Identification number OSEP6-P6-77	Sheet 87/94
			Rev A	Date of issue 2026-10-04	

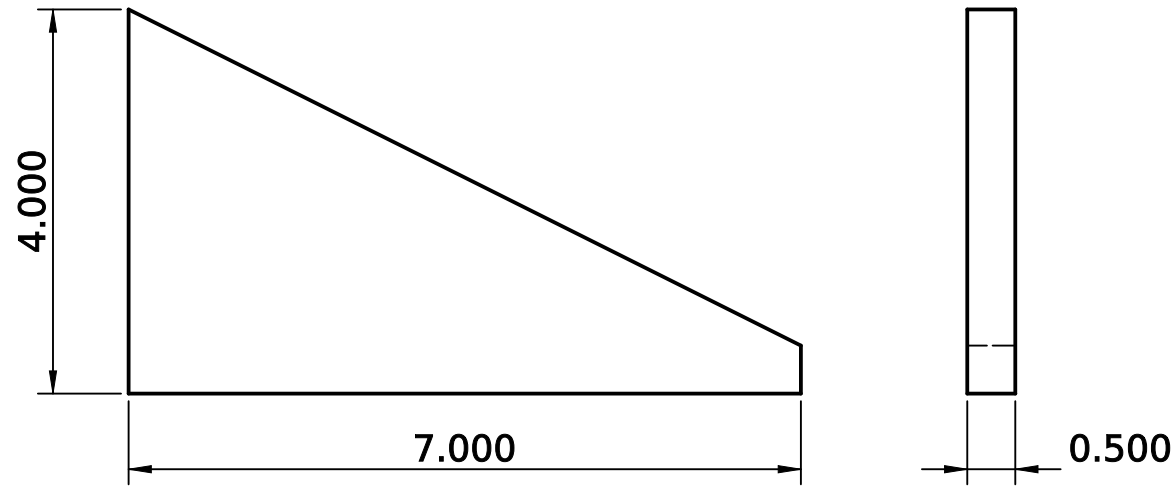

NOTES:

1. ALL DIMENSIONS IN INCHES. TOLERANCE $\pm 1/32$ UNLESS NOTED.
2. BREAK SHARP EDGES, REMOVE BURRS.
3. MATERIAL PER TITLE BLOCK. FILLET WELDS $1/4$ UNLESS NOTED.
4. OSE 01-146-00-0, IN SHAKER FRAME ASSEMBLY. USED IN: SOIL SHAKER 1.
5. DXF LIBRARY L-O5: 7 X 4 X $1/2$ - MATCHES THE MODEL.
6. GEOMETRY FROM OSE FULL_ASSEMBLY.STP (CEB PRESS 6); TITLE BLOCKS OF OSE'S 2D SET SAY 'CEB PRESS 5'.


Material 1/2" plate, 4 x 7		Qty 1	Scale 1:2	Units inch	Projection 
Created by J. Clements III		Approved by -	Document type Detail drawing		Status Draft
Legal owner J. Clements III CEB Project	Title Shaker Frame Plate L-O5 OSE CEB Press 6 (a-z Build 1.0)			Identification number OSEP6-P6-78	Sheet 88/94
				Rev A	

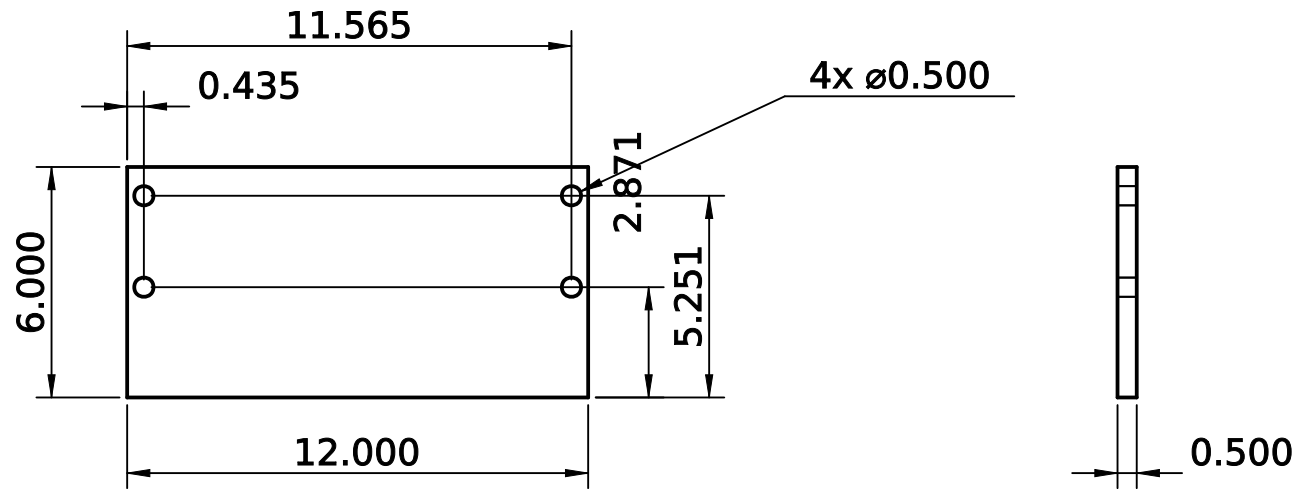

NOTES:

1. ALL DIMENSIONS IN INCHES. TOLERANCE $\pm 1/32$ UNLESS NOTED.
2. BREAK SHARP EDGES, REMOVE BURRS.
3. MATERIAL PER TITLE BLOCK. FILLET WELDS $1/4$ UNLESS NOTED.
4. OSE 01-051-00-0 / WELDMENT 001-0051, IN VALVE BRACKET ASSEMBLY. USED IN: CONTROLS 1.
5. DXF LIBRARY L-O1: 12 X 6 X $1/2$ - MATCHES THE MODEL.
6. GEOMETRY FROM OSE FULL_ASSEMBLY.STP (CEB PRESS 6); TITLE BLOCKS OF OSE'S 2D SET SAY 'CEB PRESS 5'.


Material 1/2" plate, 6 x 12		Qty 1	Scale 1:5	Units inch	Projection 	
Created by J. Clements III		Approved by -		Document type Detail drawing	Status Draft	
Legal owner J. Clements III CEB Project	Title Valve Plate L-O1 OSE CEB Press 6 (a-z Build 1.0)			Identification number OSEP6-P6-79		Sheet 89/94
				Rev A	Date of issue 2026-10-04	

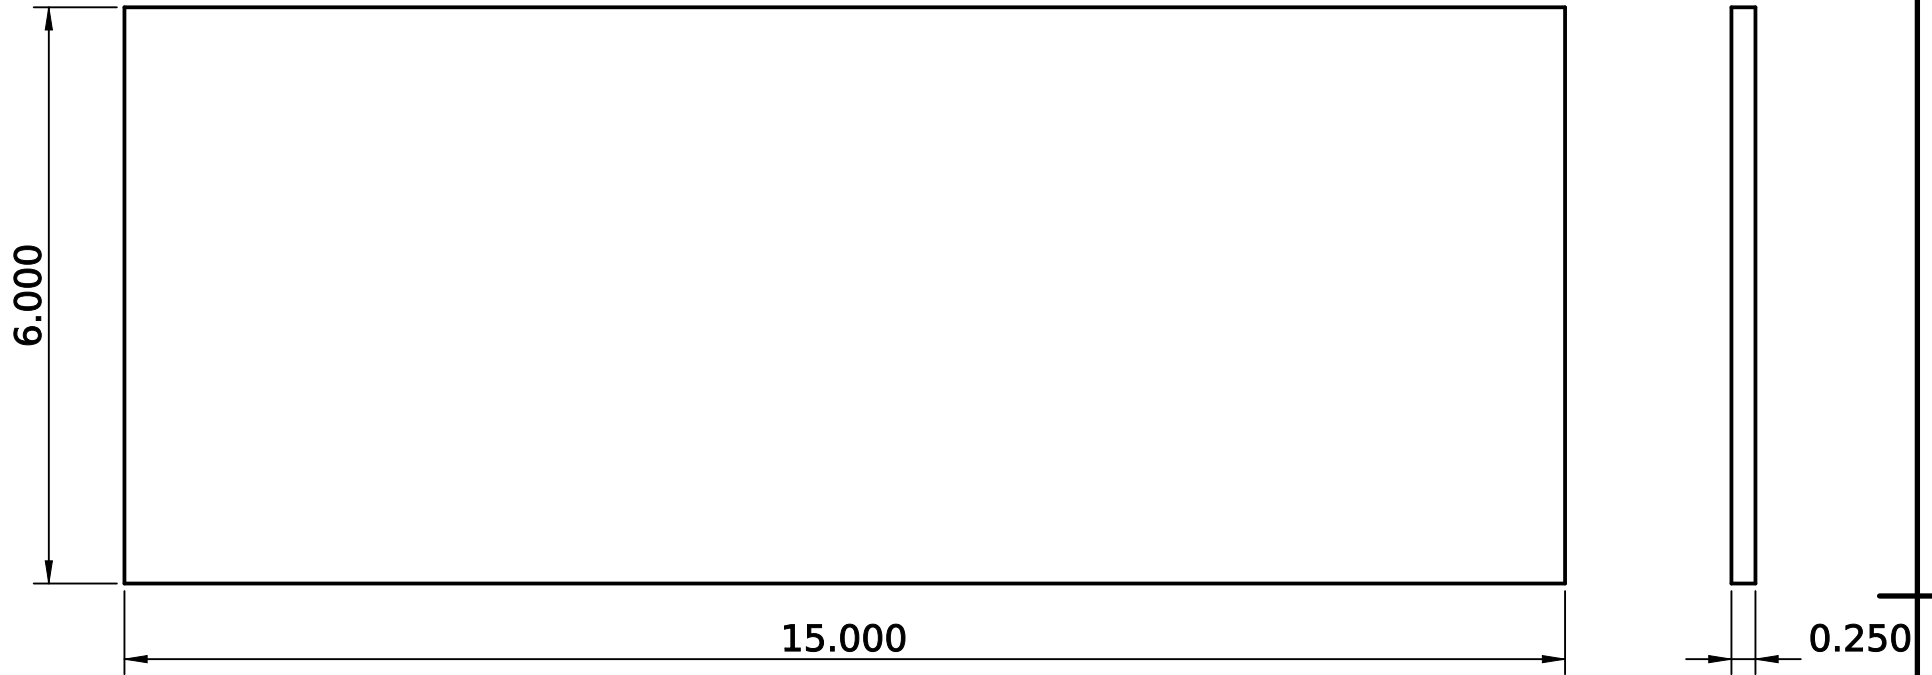

NOTES:

1. ALL DIMENSIONS IN INCHES. TOLERANCE $\pm 1/32$ UNLESS NOTED.
2. BREAK SHARP EDGES, REMOVE BURRS.
3. MATERIAL PER TITLE BLOCK. FILLET WELDS $1/4$ UNLESS NOTED.
4. OSE 01-081-00-0 / WELDMENT 001-0081, IN CONTROLLER MOUNT WELDMENT. USED IN: CONTROLS 1.
5. DXF LIBRARY L-Q6: 15 X 6 X $1/4$ - MATCHES THE MODEL.
6. GEOMETRY FROM OSE FULL_ASSEMBLY.STP (CEB PRESS 6); TITLE BLOCKS OF OSE'S 2D SET SAY 'CEB PRESS 5'.


Material 1/4" plate, 6 x 15		Qty 1	Scale 1:2	Units inch	Projection 
Created by J. Clements III		Approved by -		Document type Detail drawing	Status Draft
Legal owner J. Clements III CEB Project	Title Controller Plate L-Q6 OSE CEB Press 6 (a-z Build 1.0)			Identification number OSEP6-P6-80	Sheet 90/94
				Rev A	

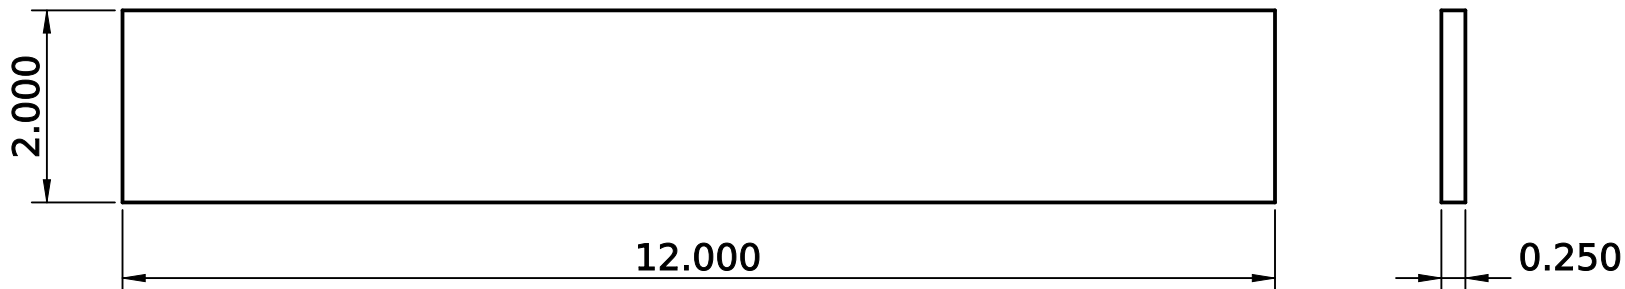

NOTES:

1. ALL DIMENSIONS IN INCHES. TOLERANCE $\pm 1/32$ UNLESS NOTED.
2. BREAK SHARP EDGES, REMOVE BURRS.
3. MATERIAL PER TITLE BLOCK. FILLET WELDS $1/4$ UNLESS NOTED.
4. OSE 01-082-00-0 / WELDMENT 001-0082, IN CONTROLLER MOUNT WELDMENT. USED IN: CONTROLS 1.
5. DXF LIBRARY L-Q8: 12 X 2 X $1/4$ - MATCHES THE MODEL.
6. GEOMETRY FROM OSE FULL_ASSEMBLY.STP (CEB PRESS 6); TITLE BLOCKS OF OSE'S 2D SET SAY 'CEB PRESS 5'.


Material 1/4" plate, 2 x 12		Qty 1	Scale 1:2	Units inch	Projection 	
Created by J. Clements III		Approved by -		Document type Detail drawing	Status Draft	
Legal owner J. Clements III CEB Project	Title Controller Mount Back L-Q8 OSE CEB Press 6 (a-z Build 1.0)			Identification number OSEP6-P6-81		Sheet 91/94
				Rev A	Date of issue 2026-10-04	

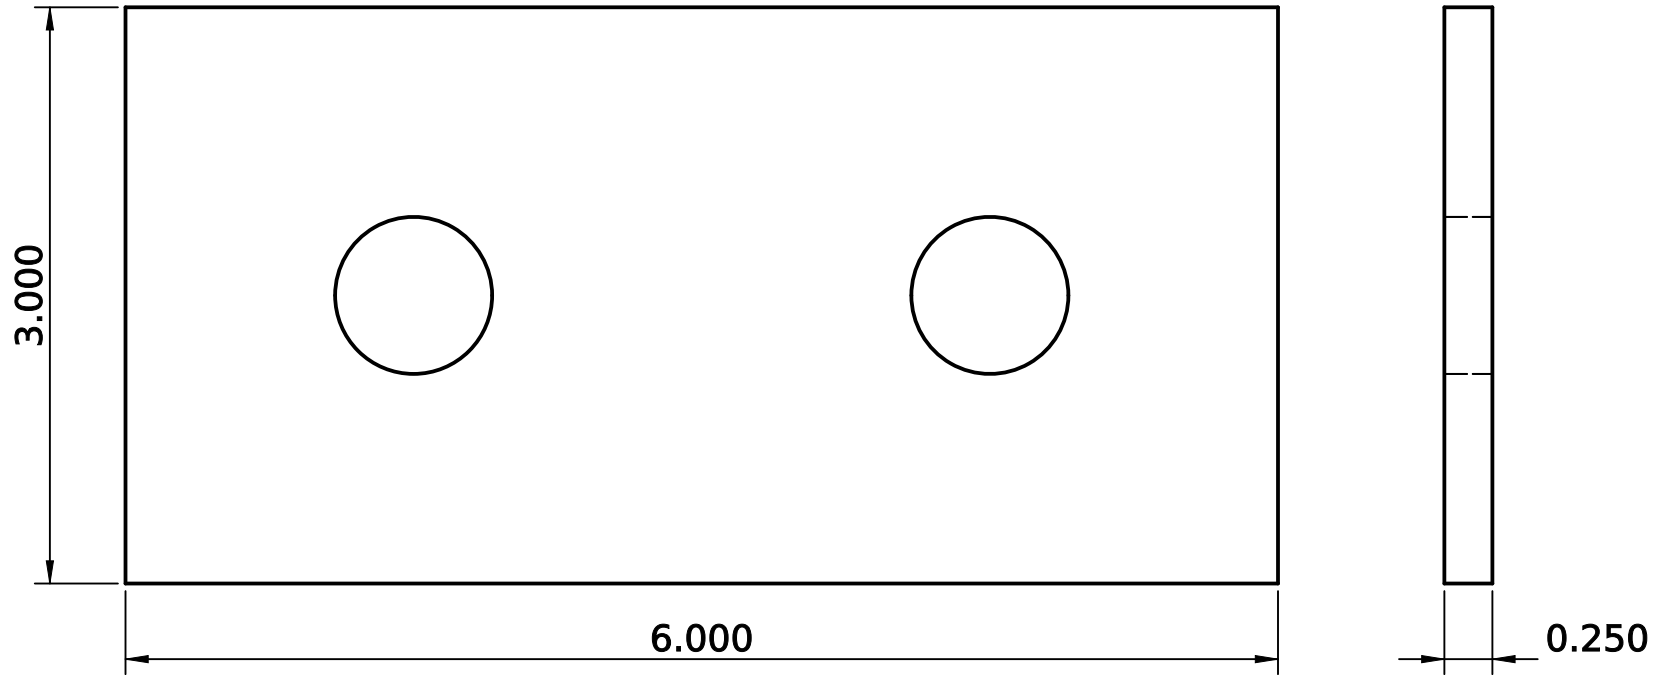

NOTES:

1. ALL DIMENSIONS IN INCHES. TOLERANCE $\pm 1/32$ UNLESS NOTED.
2. BREAK SHARP EDGES, REMOVE BURRS.
3. MATERIAL PER TITLE BLOCK. FILLET WELDS $1/4$ UNLESS NOTED.
4. OSE 01-083-00-0 / WELDMENT 001-0083, IN CONTROLLER MOUNT WELDMENT. USED IN: CONTROLS 1.
5. DXF LIBRARY L-Q7: 6 X 3 X $1/4$ - MATCHES THE MODEL.
6. GEOMETRY FROM OSE FULL_ASSEMBLY.STP (CEB PRESS 6); TITLE BLOCKS OF OSE'S 2D SET SAY 'CEB PRESS 5'.


Material 1/4" plate, 3 x 6		Qty 1	Scale 1:1	Units inch	Projection 	
Created by J. Clements III		Approved by -		Document type Detail drawing	Status Draft	
Legal owner J. Clements III CEB Project	Title Controller Mount - Bottom piece OSE CEB Press 6 (a-z Build 1.0)			Identification number OSE P6-82		Sheet 92/94
				Rev A	Date of issue 2026-10-04	

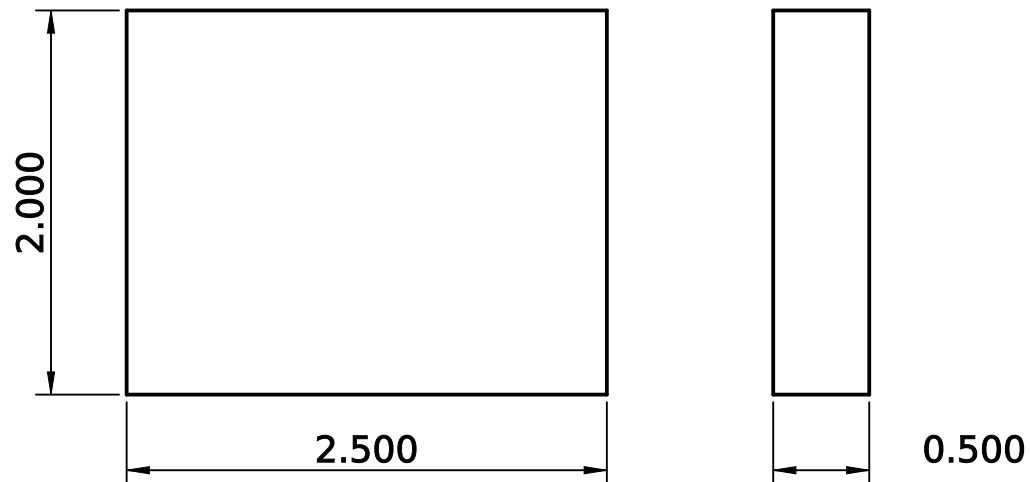

NOTES:

1. ALL DIMENSIONS IN INCHES. TOLERANCE $\pm 1/32$ UNLESS NOTED.
2. BREAK SHARP EDGES, REMOVE BURRS.
3. MATERIAL PER TITLE BLOCK. FILLET WELDS $1/4$ UNLESS NOTED.
4. OSE 01-143-00-0, IN VALVE BRACKET ASSEMBLY. USED IN: CONTROLS 2.
5. DXF LIBRARY L-O9: $2-1/2 \times 2 \times 1/2$ - MATCHES THE MODEL.
6. GEOMETRY FROM OSE FULL_ASSEMBLY.STP (CEB PRESS 6); TITLE BLOCKS OF OSE'S 2D SET SAY 'CEB PRESS 5'.

Material 1/2" plate, 2 x 2-1/2		Qty 2	Scale 1:1	Units inch	Projection 
Created by J. Clements III		Approved by -		Document type Detail drawing	Status Draft
Legal owner J. Clements III CEB Project	Title Valve Bracket Plate L-09 OSE CEB Press 6 (a-z Build 1.0)			Identification number OSEP6-P6-83	Sheet 93/94
				Rev A	

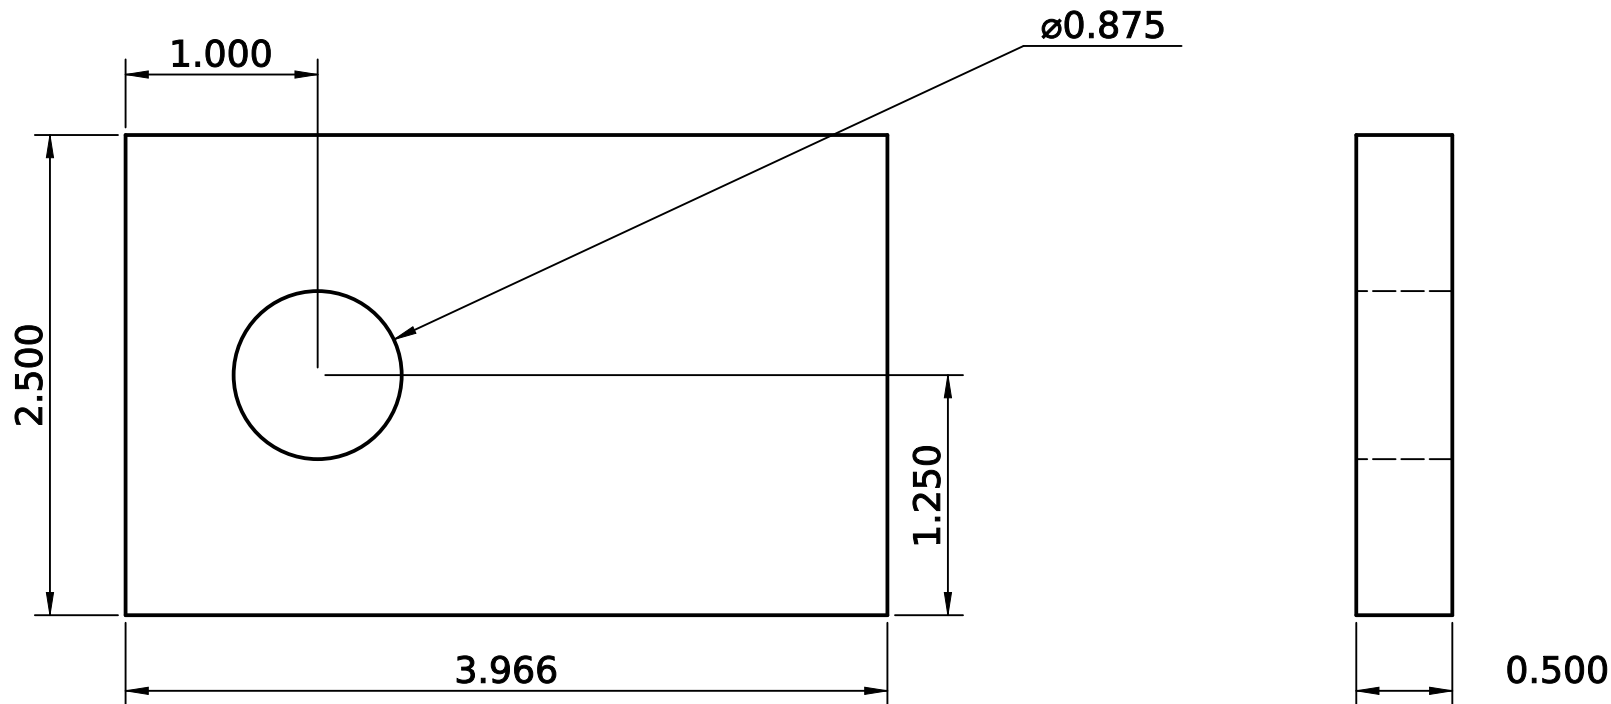

NOTES:

1. ALL DIMENSIONS IN INCHES. TOLERANCE $\pm 1/32$ UNLESS NOTED.
2. BREAK SHARP EDGES, REMOVE BURRS.
3. MATERIAL PER TITLE BLOCK. FILLET WELDS $1/4$ UNLESS NOTED.
4. OSE 01-246-00-0, IN VALVE BRACKET ASSEMBLY. USED IN: CONTROLS 2.
5. DXF LIBRARY L-O8: 3.966 X 2-1/2 X 1/2 - MATCHES THE MODEL.
6. GEOMETRY FROM OSE FULL_ASSEMBLY.STP (CEB PRESS 6); TITLE BLOCKS OF OSE'S 2D SET SAY 'CEB PRESS 5'.

Material 1/2" plate, 2-1/2 x 3.966		Qty 2	Scale 1:1	Units inch	Projection 	
Created by J. Clements III		Approved by -		Document type Detail drawing	Status Draft	
Legal owner J. Clements III CEB Project	Title Valve Bracket Plate L-O8 OSE CEB Press 6 (a-z Build 1.0)			Identification number OSEP6-P6-84		Sheet 94/94
				Rev A	Date of issue 2026-10-04	