



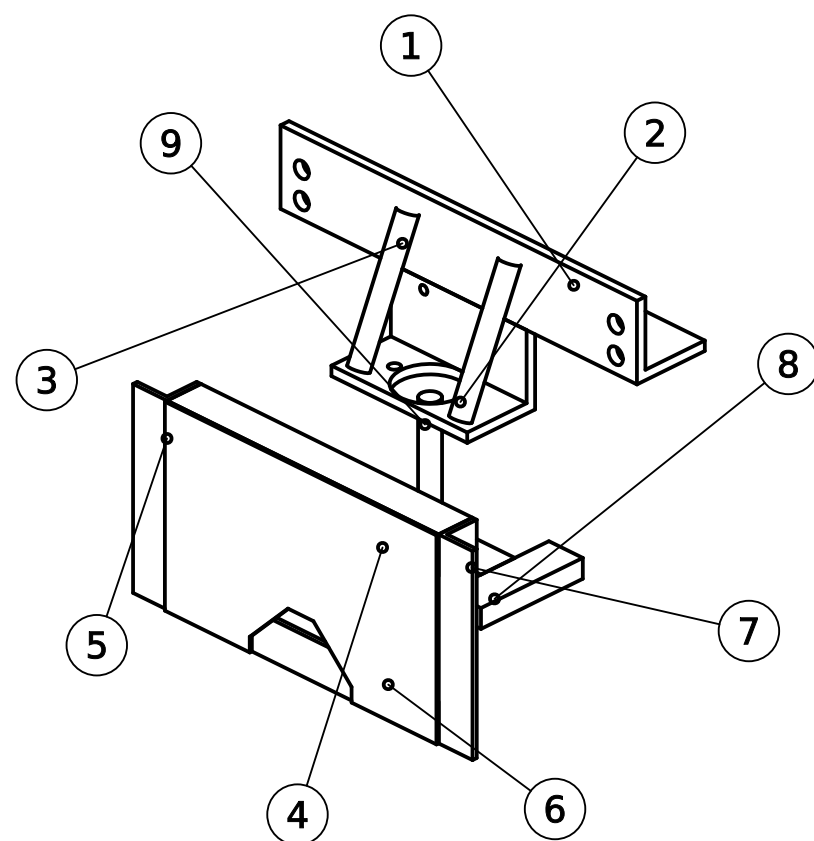

ISOMETRIC VIEW (ARRANGEMENT INDICATIVE)

NOTES:
1. ALL DIMENSIONS IN INCHES. TOLERANCE $\pm 1/32$ UNLESS NOTED.
2. BREAK SHARP EDGES, REMOVE BURRS.
3. MATERIAL PER TITLE BLOCK. FILLET WELDS $1/4$ UNLESS NOTED.
4. STEEL WEIGHT ABOUT 59 LB, LESS MOTOR AND COUPLER.
5. BUY: HYDRAULIC MOTOR (2-BOLT SAE A, 3-3/8 PILOT), 1 IN KEYED COUPLER CUT TO 2 LONG, $1/4 \times 2$ BOLT, $1/2$ NPT NEEDLE VALVE, TEE, HOSES PER A-Z STEP 5.
6. SOURCES: OSE CEB A-Z BUILD 1.0 PP. 15-20; OSE WELDMENTS 001-0042..0048, 001-0077.




9	1	Shaft	1" CRS x 7-1/4	1.6	OSESH-shaker-09
8	1	Hammer Head	1 x 2 flat x 6	3.4	OSESH-shaker-08
7	1	Hammer Arm	1 x 2 flat x 5	2.6	OSESH-shaker-07
6	2	Guard Top / Bottom Angle	L2 x 2 x 1/4 x 16	4.3	OSESH-shaker-06
5	2	Guard Side Angle	L2 x 2 x 1/4 x 10	2.7	OSESH-shaker-05
4	1	Guard	1/8" sheet, 10 x 16	5.2	OSESH-shaker-04
3	2	Brace Rod	1" round (or #8 rebar) x 7	1.6	OSESH-shaker-03
2	1	Motor Angle 8	L4 x 4 x 1/2 x 8	7.1	OSESH-shaker-02
1	1	Mount Angle 21	L4 x 4 x 1/2 x 21	21.9	OSESH-shaker-01
Item	Qty	Title	Stock	lb ea	Drawing no.
Material		Qty	Scale	Units	Projection
See parts list		1	1:8	inch	
Created by		Approved by	Document type		Status
J. Clements III		-	Assembly drawing		Draft
Legal owner		Title		Identification number	Sheet
J. Clements III		OSE CEB Soil Shaker		OSESH-00	1/10
CEB Project		Assembly		Rev A	
				Date of issue	
				2026-10-03	

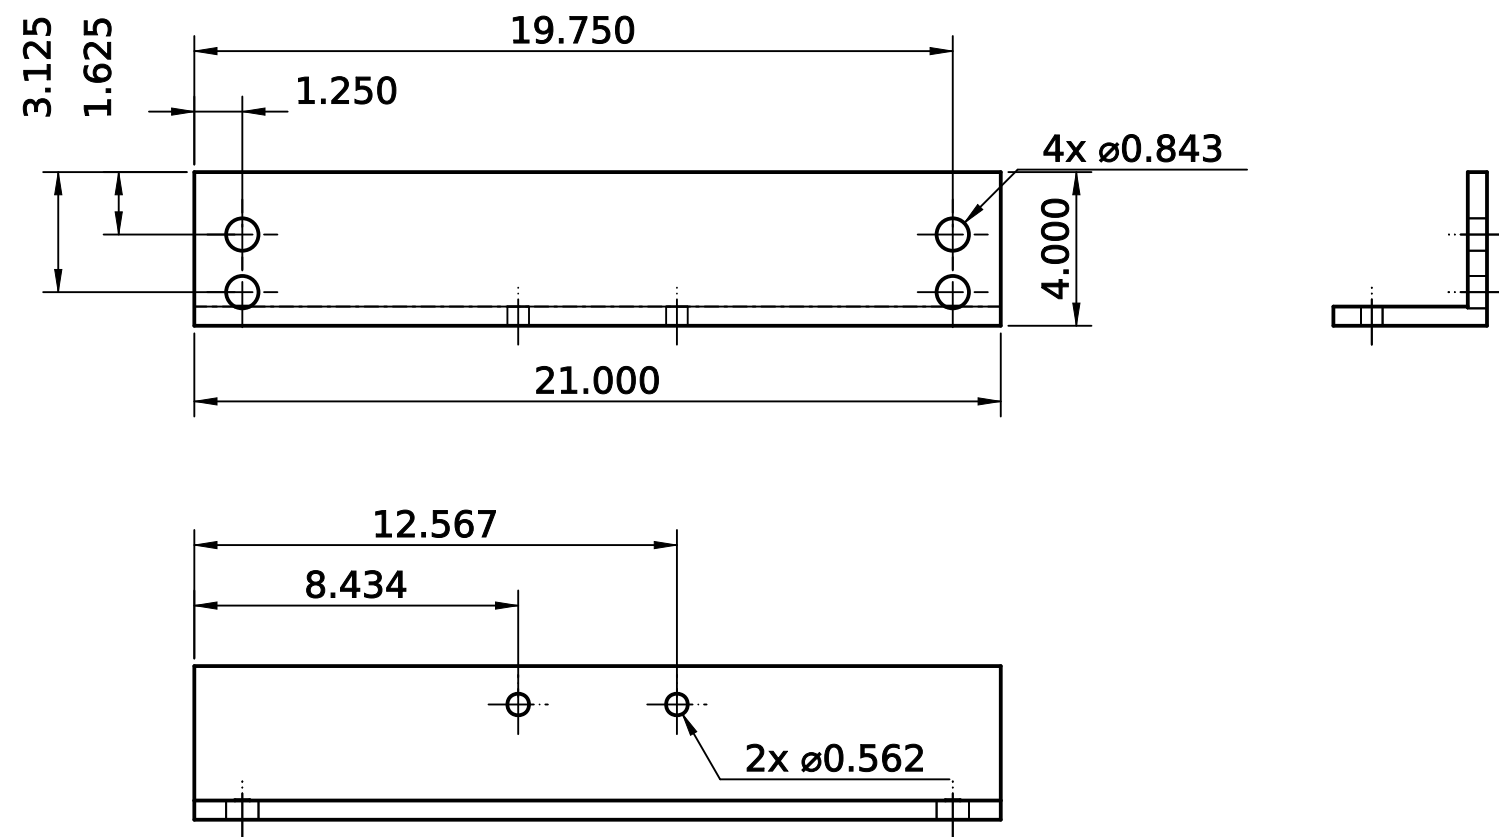

NOTES:

1. ALL DIMENSIONS IN INCHES. TOLERANCE $\pm 1/32$ UNLESS NOTED.
2. BREAK SHARP EDGES, REMOVE BURRS.
3. MATERIAL PER TITLE BLOCK. FILLET WELDS $1/4$ UNLESS NOTED.
4. OSE 001-0042. BOLTS TO THE HOPPER SUPPORTS ON $3/4$ BOLTS WELDED TO THEM (A-Z STEP 6).
5. GRIND THE TOP WELD TO THE 8 IN ANGLE FLUSH SO THE MOTOR SEATS FLAT.


Material L4 x 4 x 1/2 x 21		Qty 1	Scale 1:5	Units inch	Projection 
Created by J. Clements III		Approved by -		Document type Detail drawing	Status Draft
Legal owner J. Clements III CEB Project		Title Mount Angle 21 OSE CEB Soil Shaker, shaker brick		Identification number OSES-shaker-01	Sheet 2/10
		Rev A	Date of issue 2026-10-03		

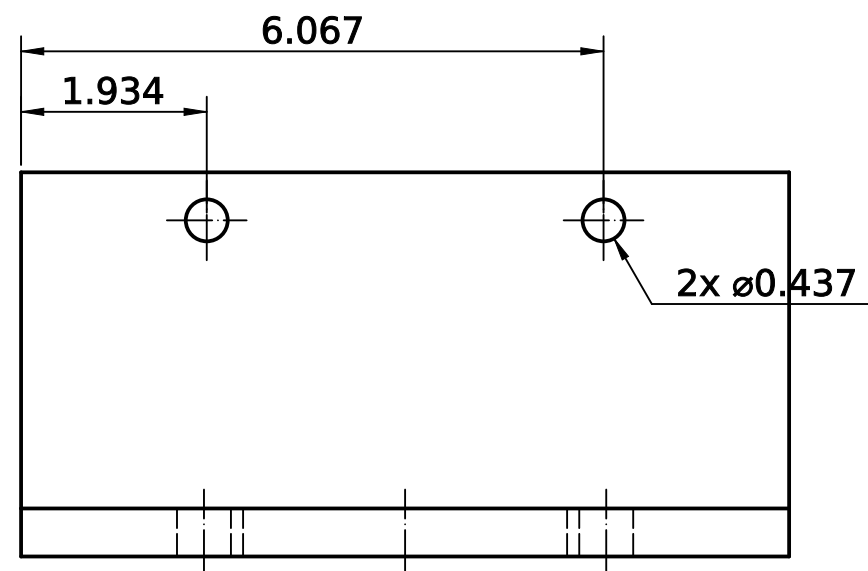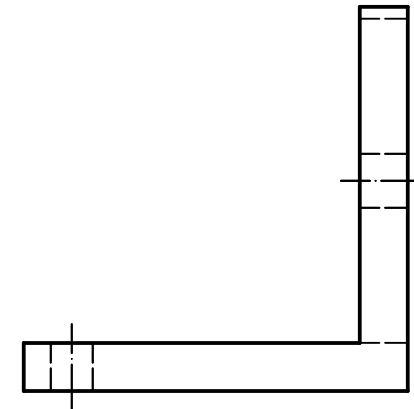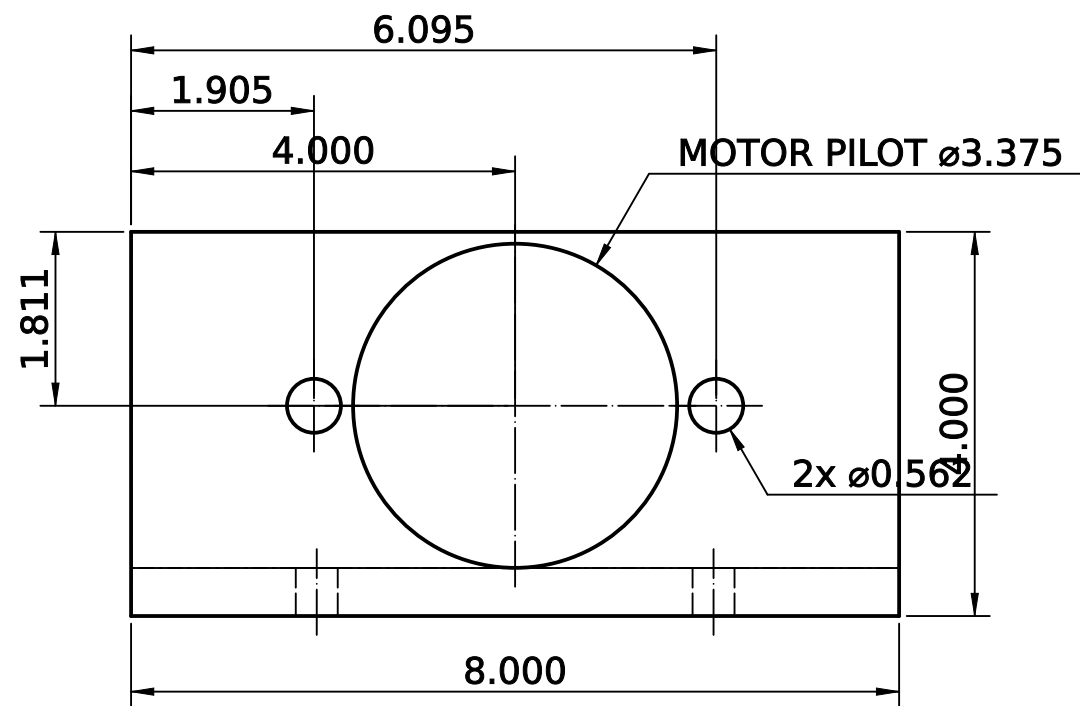

NOTES:

1. ALL DIMENSIONS IN INCHES. TOLERANCE $\pm 1/32$ UNLESS NOTED.
2. BREAK SHARP EDGES, REMOVE BURRS.
3. MATERIAL PER TITLE BLOCK. FILLET WELDS $1/4$ UNLESS NOTED.
4. OSE 001-0043. TORCH THE PILOT; THE MOTOR'S RAISED CENTRE MUST PASS RIGHT THROUGH.
5. MANUAL P. 17 ALLOWS ONE SHAPED CUTOUT FOR PILOT AND BOTH BOLTS INSTEAD.


Material L4 x 4 x 1/2 x 8		Qty 1	Scale 1:2	Units inch	Projection 
Created by J. Clements III		Approved by -		Document type Detail drawing	
Legal owner J. Clements III CEB Project		Title Motor Angle 8 OSE CEB Soil Shaker, shaker brick			Identification number OESH-shaker-02
		Rev A		Date of issue 2026-10-03	Sheet 3/10

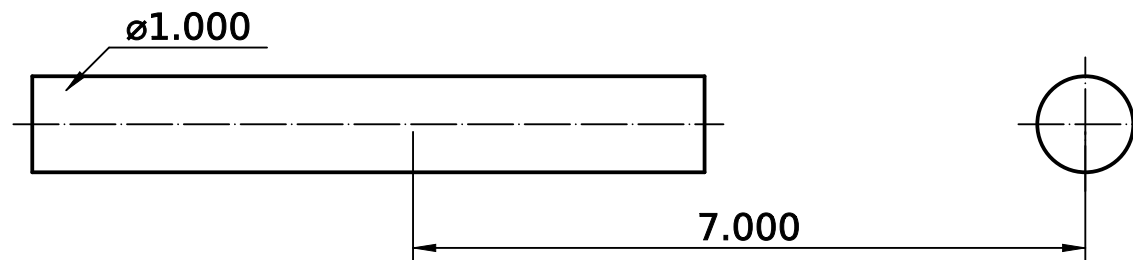

NOTES:

1. ALL DIMENSIONS IN INCHES. TOLERANCE $\pm 1/32$ UNLESS NOTED.
2. BREAK SHARP EDGES, REMOVE BURRS.
3. MATERIAL PER TITLE BLOCK. FILLET WELDS $1/4$ UNLESS NOTED.
4. OSE 001-0047. ENDS CUT TO FIT; WELD FROM THE 8 IN ANGLE TO THE 21 IN ANGLE.


Material 1" round (or #8 rebar) x 7		Qty 2	Scale 1:2	Units inch	Projection 
Created by J. Clements III		Approved by -		Document type Detail drawing	Status Draft
Legal owner J. Clements III CEB Project	Title Brace Rod OSE CEB Soil Shaker, shaker brick			Identification number OESH-shaker-03	
				Rev A	Date of issue 2026-10-03
					Sheet 4/10

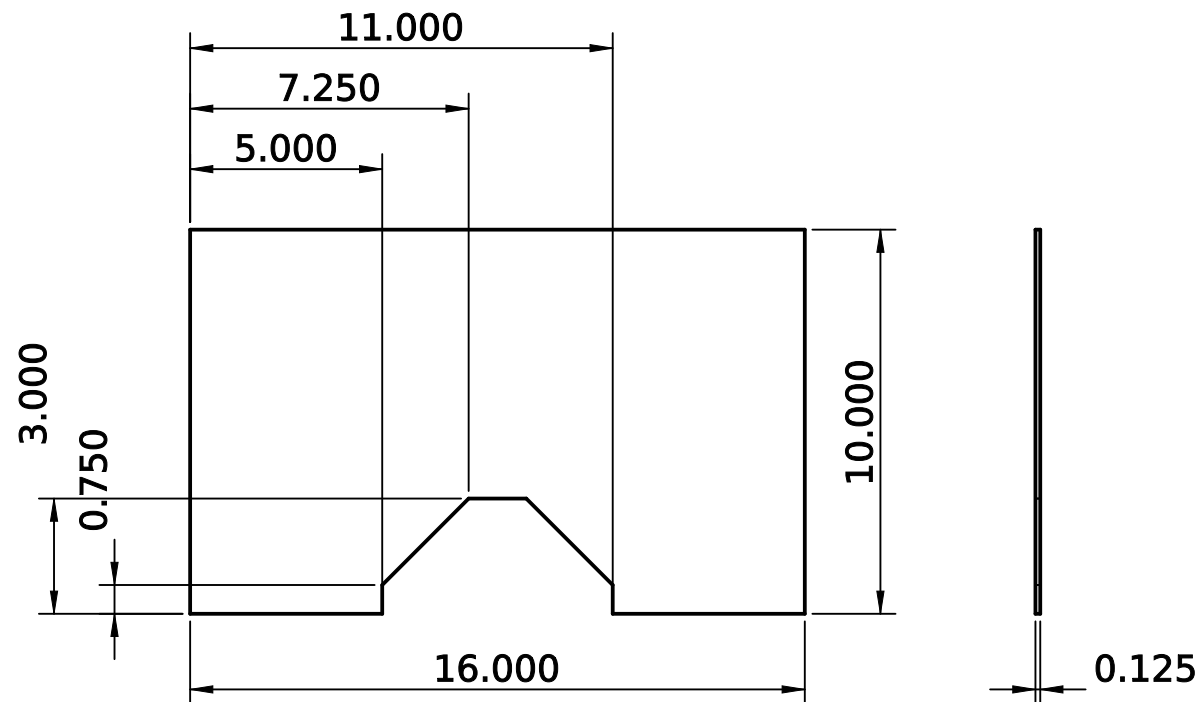

NOTES:

1. ALL DIMENSIONS IN INCHES. TOLERANCE $\pm 1/32$ UNLESS NOTED.
2. BREAK SHARP EDGES, REMOVE BURRS.
3. MATERIAL PER TITLE BLOCK. FILLET WELDS $1/4$ UNLESS NOTED.
4. MANUAL P. 15 (OSE 001-0074). NOTCH CENTRED; IT CLEARS THE HAMMER.
5. THE GUARD CATCHES THE HAMMER IF ITS WELD FAILS: WELD THE FRAME ANGLES ALL ROUND.


Material 1/8" sheet, 10 x 16		Qty 1	Scale 1:5	Units inch	Projection 
Created by J. Clements III		Approved by -		Document type Detail drawing	Status Draft
Legal owner J. Clements III CEB Project	Title Guard OSE CEB Soil Shaker, shaker brick	Identification number OESH-shaker-04			Sheet 5/10
		Rev A	Date of issue 2026-10-03		

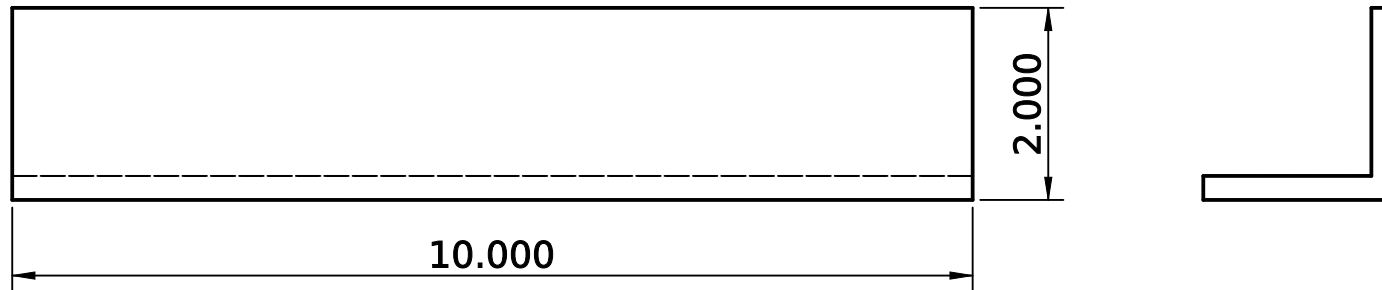

NOTES:

1. ALL DIMENSIONS IN INCHES. TOLERANCE $\pm 1/32$ UNLESS NOTED.
2. BREAK SHARP EDGES, REMOVE BURRS.
3. MATERIAL PER TITLE BLOCK. FILLET WELDS $1/4$ UNLESS NOTED.
4. OSE 001-0105.


Material L2 x 2 x 1/4 x 10		Qty 2	Scale 1:2	Units inch	Projection 	
Created by J. Clements III		Approved by -		Document type Detail drawing	Status Draft	
Legal owner J. Clements III CEB Project	Title Guard Side Angle OSE CEB Soil Shaker, shaker brick			Identification number OESH-shaker-05		Sheet 6/10
				Rev A	Date of issue 2026-10-03	

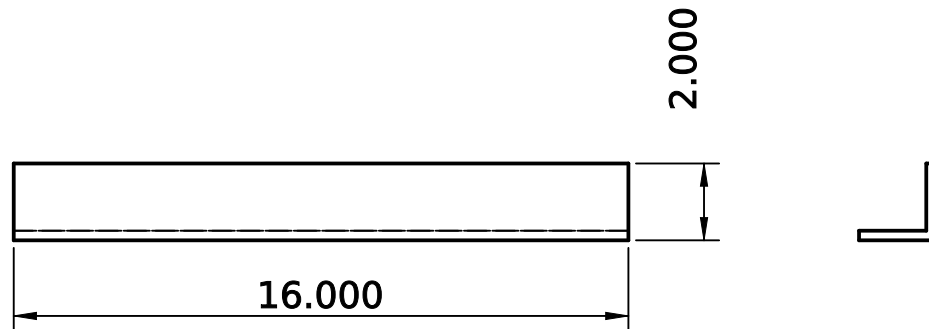

NOTES:

1. ALL DIMENSIONS IN INCHES. TOLERANCE $\pm 1/32$ UNLESS NOTED.
2. BREAK SHARP EDGES, REMOVE BURRS.
3. MATERIAL PER TITLE BLOCK. FILLET WELDS $1/4$ UNLESS NOTED.
4. OSE 001-0106. THE BOTTOM ONE WELDS TO THE 21 IN ANGLE.


Material L2 x 2 x 1/4 x 16		Qty 2	Scale 1:5	Units inch	Projection 
Created by J. Clements III		Approved by -		Document type Detail drawing	Status Draft
Legal owner J. Clements III CEB Project	Title Guard Top / Bottom Angle OSE CEB Soil Shaker, shaker brick			Identification number OSES-shaker-06	
				Rev A	Date of issue 2026-10-03
					Sheet 7/10

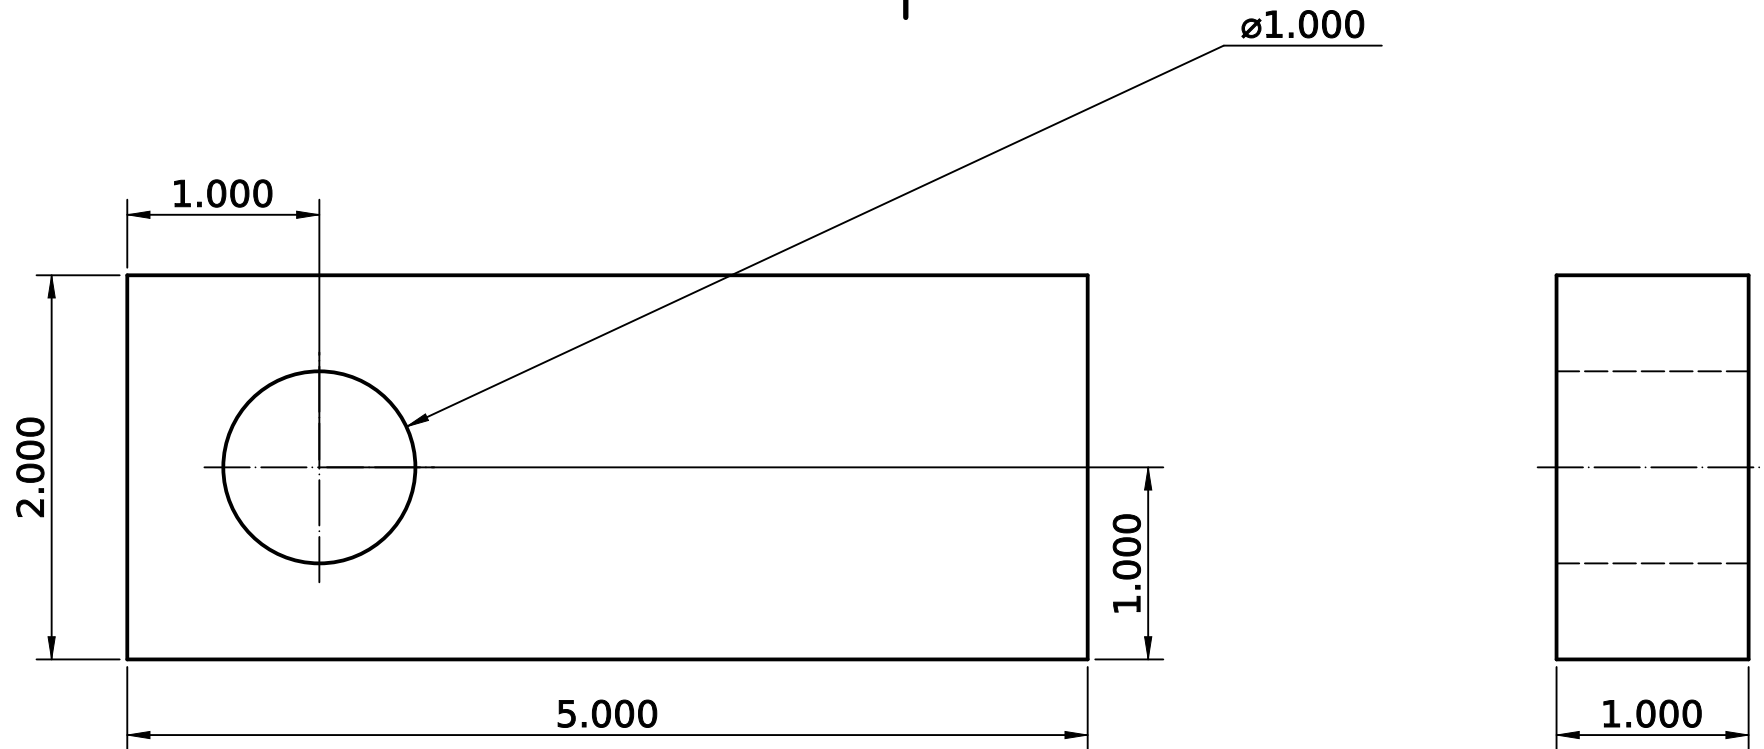

NOTES:

1. ALL DIMENSIONS IN INCHES. TOLERANCE $\pm 1/32$ UNLESS NOTED.
2. BREAK SHARP EDGES, REMOVE BURRS.
3. MATERIAL PER TITLE BLOCK. FILLET WELDS $1/4$ UNLESS NOTED.
4. OSE 001-0044. WELD TO THE HAMMER HEAD 0.41 FILLET BOTH SIDES; IT MUST NOT COME OFF.


Material 1 x 2 flat x 5	Qty 1	Scale 1:1	Units inch	Projection 
Created by J. Clements III	Approved by -	Document type Detail drawing	Status Draft	
Legal owner J. Clements III CEB Project	Title Hammer Arm OSE CEB Soil Shaker, shaker brick	Identification number OESH-shaker-07	Rev A	Sheet 8/10
		Date of issue 2026-10-03		

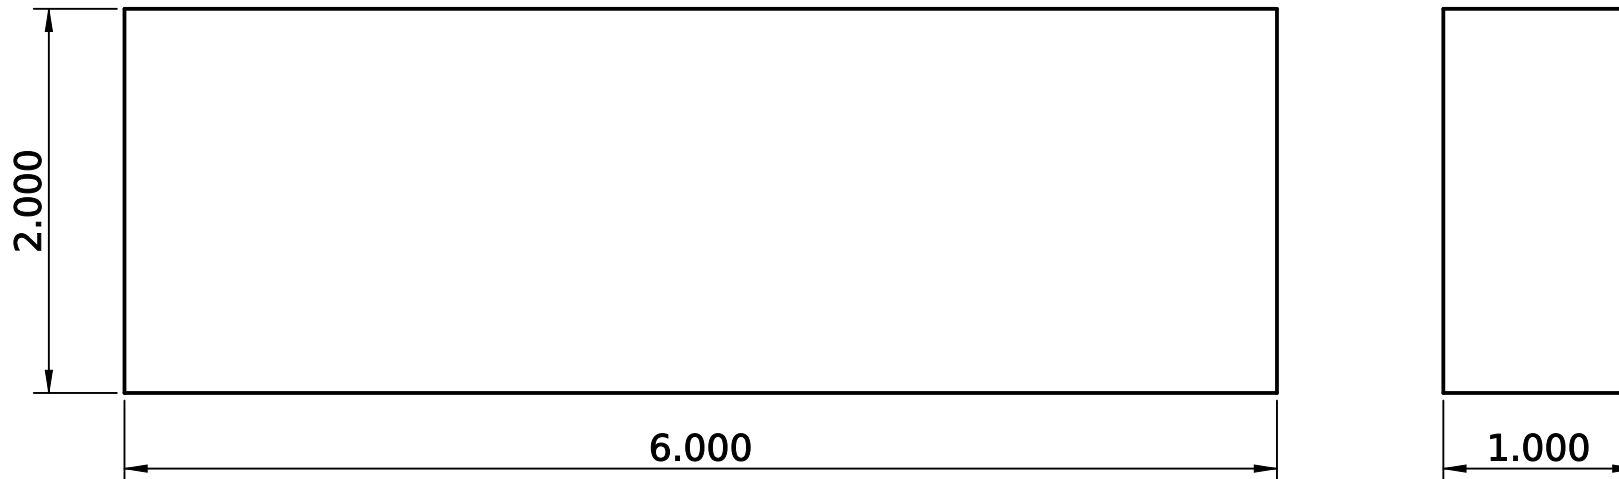

NOTES:

1. ALL DIMENSIONS IN INCHES. TOLERANCE $\pm 1/32$ UNLESS NOTED.
2. BREAK SHARP EDGES, REMOVE BURRS.
3. MATERIAL PER TITLE BLOCK. FILLET WELDS $1/4$ UNLESS NOTED.
4. OSE 001-0045.

Material 1 x 2 flat x 6		Qty 1	Scale 1:1	Units inch	Projection 
Created by J. Clements III		Approved by -		Document type Detail drawing	Status Draft
Legal owner J. Clements III CEB Project	Title Hammer Head OSE CEB Soil Shaker, shaker brick			Identification number OESH-shaker-08	Sheet 9/10
				Rev A	

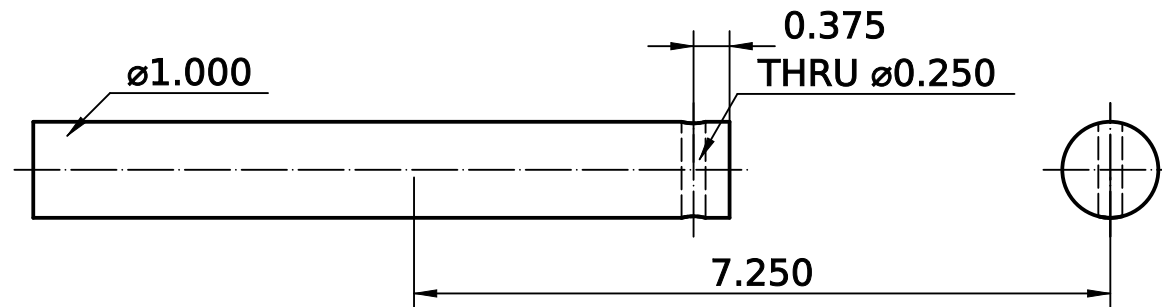

NOTES:

1. ALL DIMENSIONS IN INCHES. TOLERANCE $\pm 1/32$ UNLESS NOTED.
2. BREAK SHARP EDGES, REMOVE BURRS.
3. MATERIAL PER TITLE BLOCK. FILLET WELDS 1/4 UNLESS NOTED.
4. OSE 001-0046. SHAFT END 1/4 SHORT OF THE HAMMER ARM'S FAR FACE; 1/4 BOLT HOLE DRILLED WITH THE COUPLER ON, 3/8 FROM THE COUPLER'S EDGE (MANUAL P. 19).
5. COUPLER: 1 IN KEYED, CUT TO 2 LONG. HAMMER 5/8 CLEAR OF THE MOUNT.

Material 1" CRS x 7-1/4		Qty 1	Scale 1:2	Units inch	Projection 
Created by J. Clements III		Approved by -		Document type Detail drawing	Status Draft
Legal owner J. Clements III CEB Project	Title Shaft OSE CEB Soil Shaker, shaker brick	Identification number OESH-shaker-09		Sheet 10/10	
		Rev A	Date of issue 2026-10-03		